



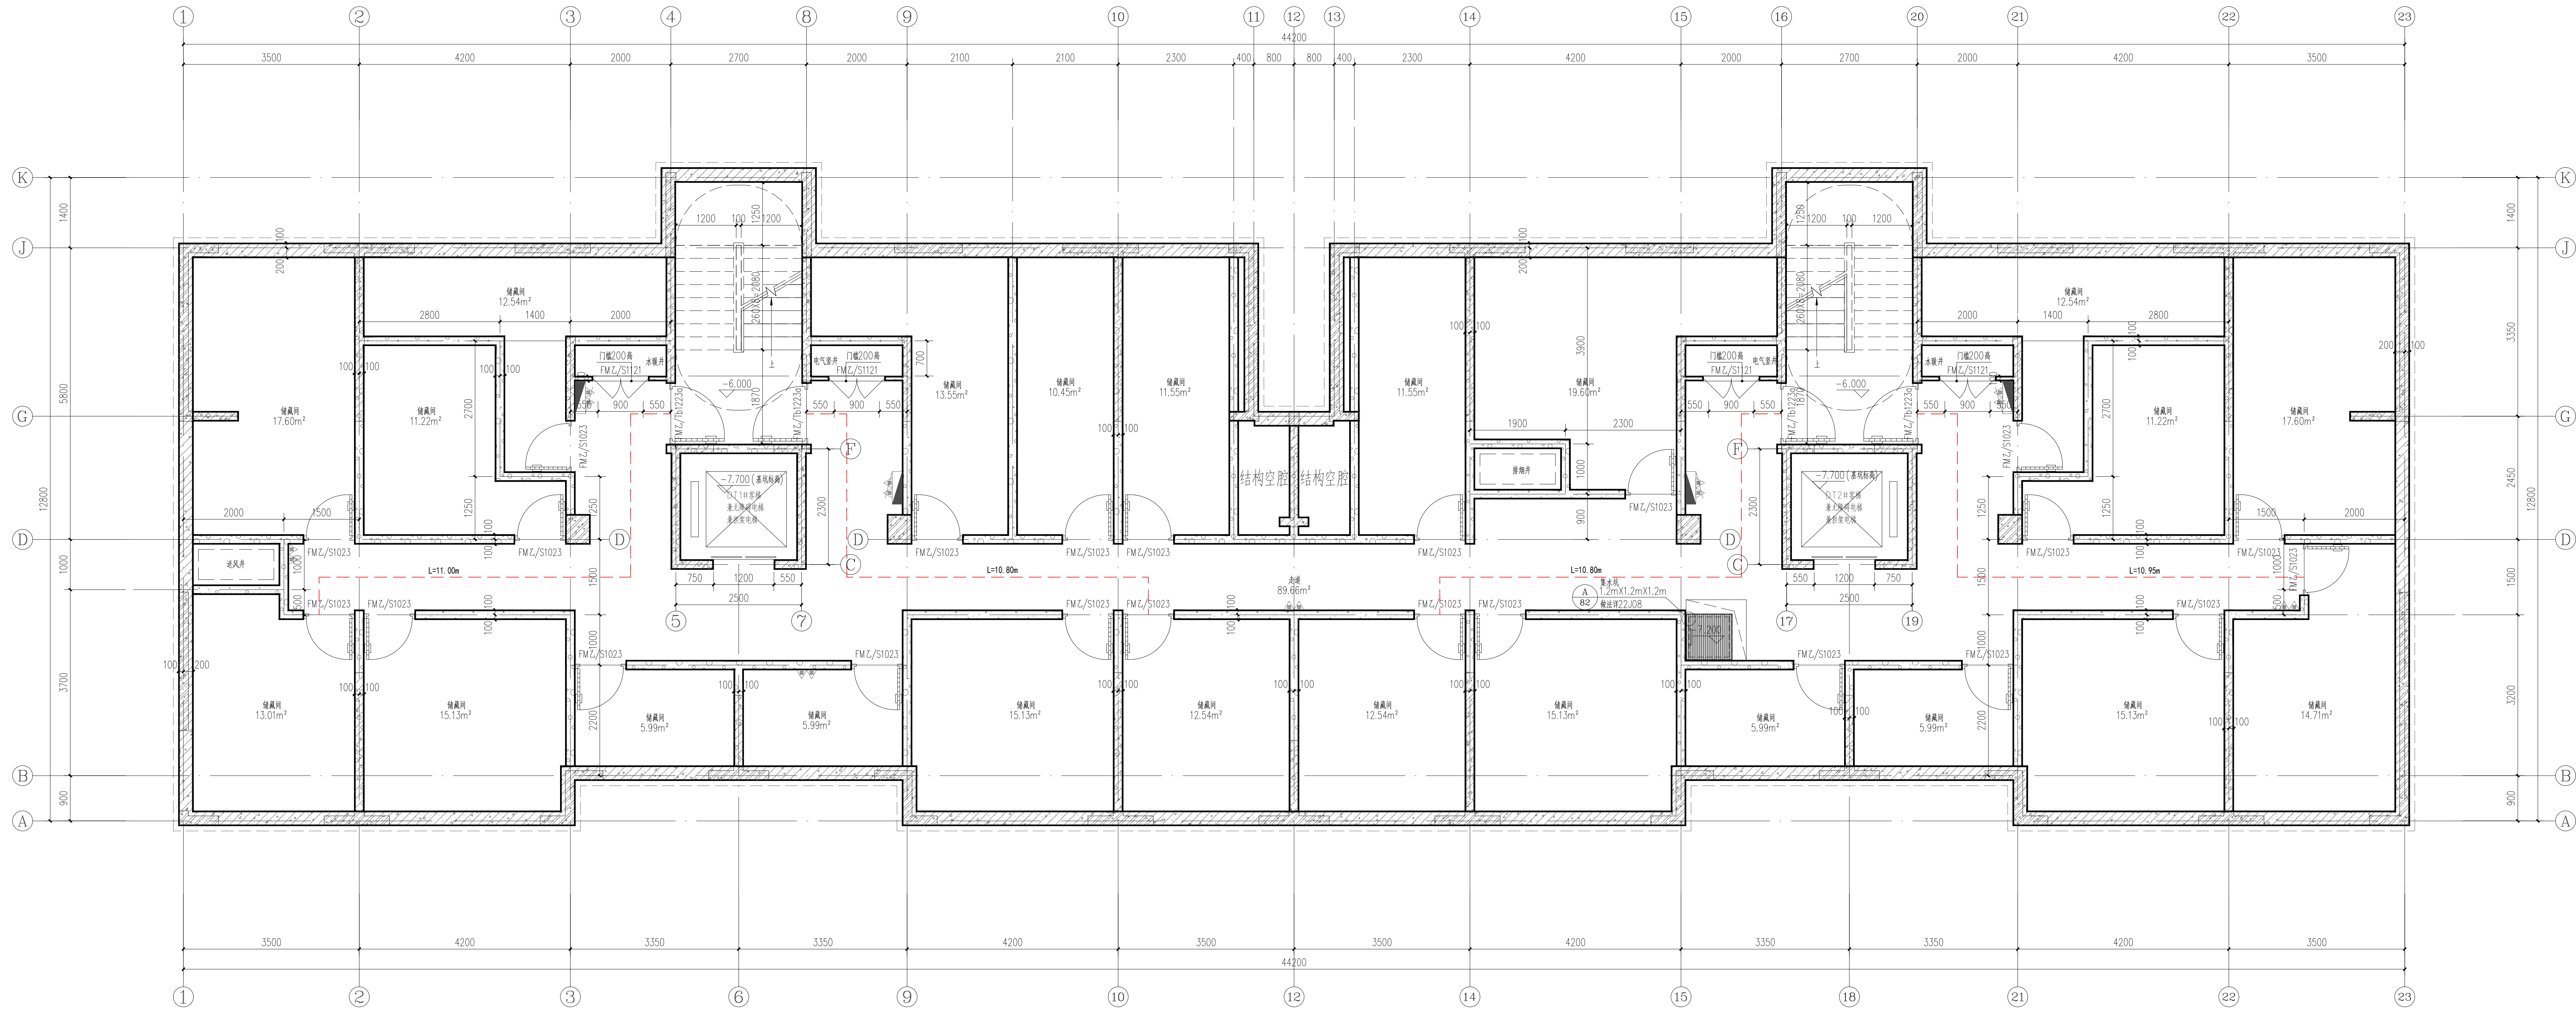

地下二层平面图 1:50

本层建筑面积: 498.48m²

总建筑面积: 6248.29m²

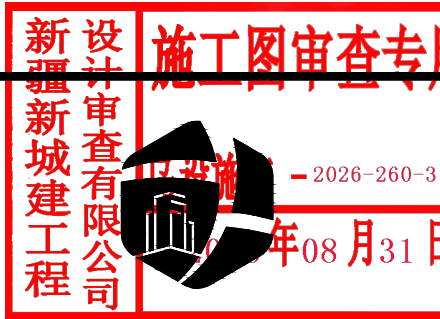

永忠工程管理(集团)有限公司
Yong Zhong Engineering Management (Group) Co., Ltd.

甲级工程设计证书编号:A151027583

合作设计顾问单位 CONSULTING ARCHITECT

设计部门 新疆分公司

电 话 18999878562

说 明:

- 1、本图版权为本设计院拥有, 任何人士如未获允许不得翻印任何部分。
- 2、所有尺寸均以标注为准, 图上自行量取无效。
- 3、本图需加盖本设计院工程设计出图专用章及注册章方有效。
- 4、本套图需经国家有关部门批准方可施工。

平面示意:

注册执业章

姓 名: 李 亮

注册证书号码: 2024500624

注册印章号码: 51A0246-002

建设单位: 新疆知筑房地产开发有限公司

工程名称: 阿勒泰市御景园商住一期建设项目

子项名称: 10#住宅楼

设计号: YXJ-2023-07-10

图 名: 地下二层平面图

项目负责人

审 定

审 核

专业负责人

校 对

设 计

中华人民共和国一级注册建筑师

姓 名: 李 亮

注册号: 51A0246-002

有效期: 至2028年05月

四川省建设工程设计出图专用章

永忠工程管理(集团)有限公司

水利部水利行业(河道整治、引调水、

城市防洪、灌溉排涝)专业乙级、

建筑行业(建筑工程)甲级

资质证书编号:A151A02463 有效期至:2031年02月11日

出图日期: 2023-08

比例: 1:100

版本号: 第一版