


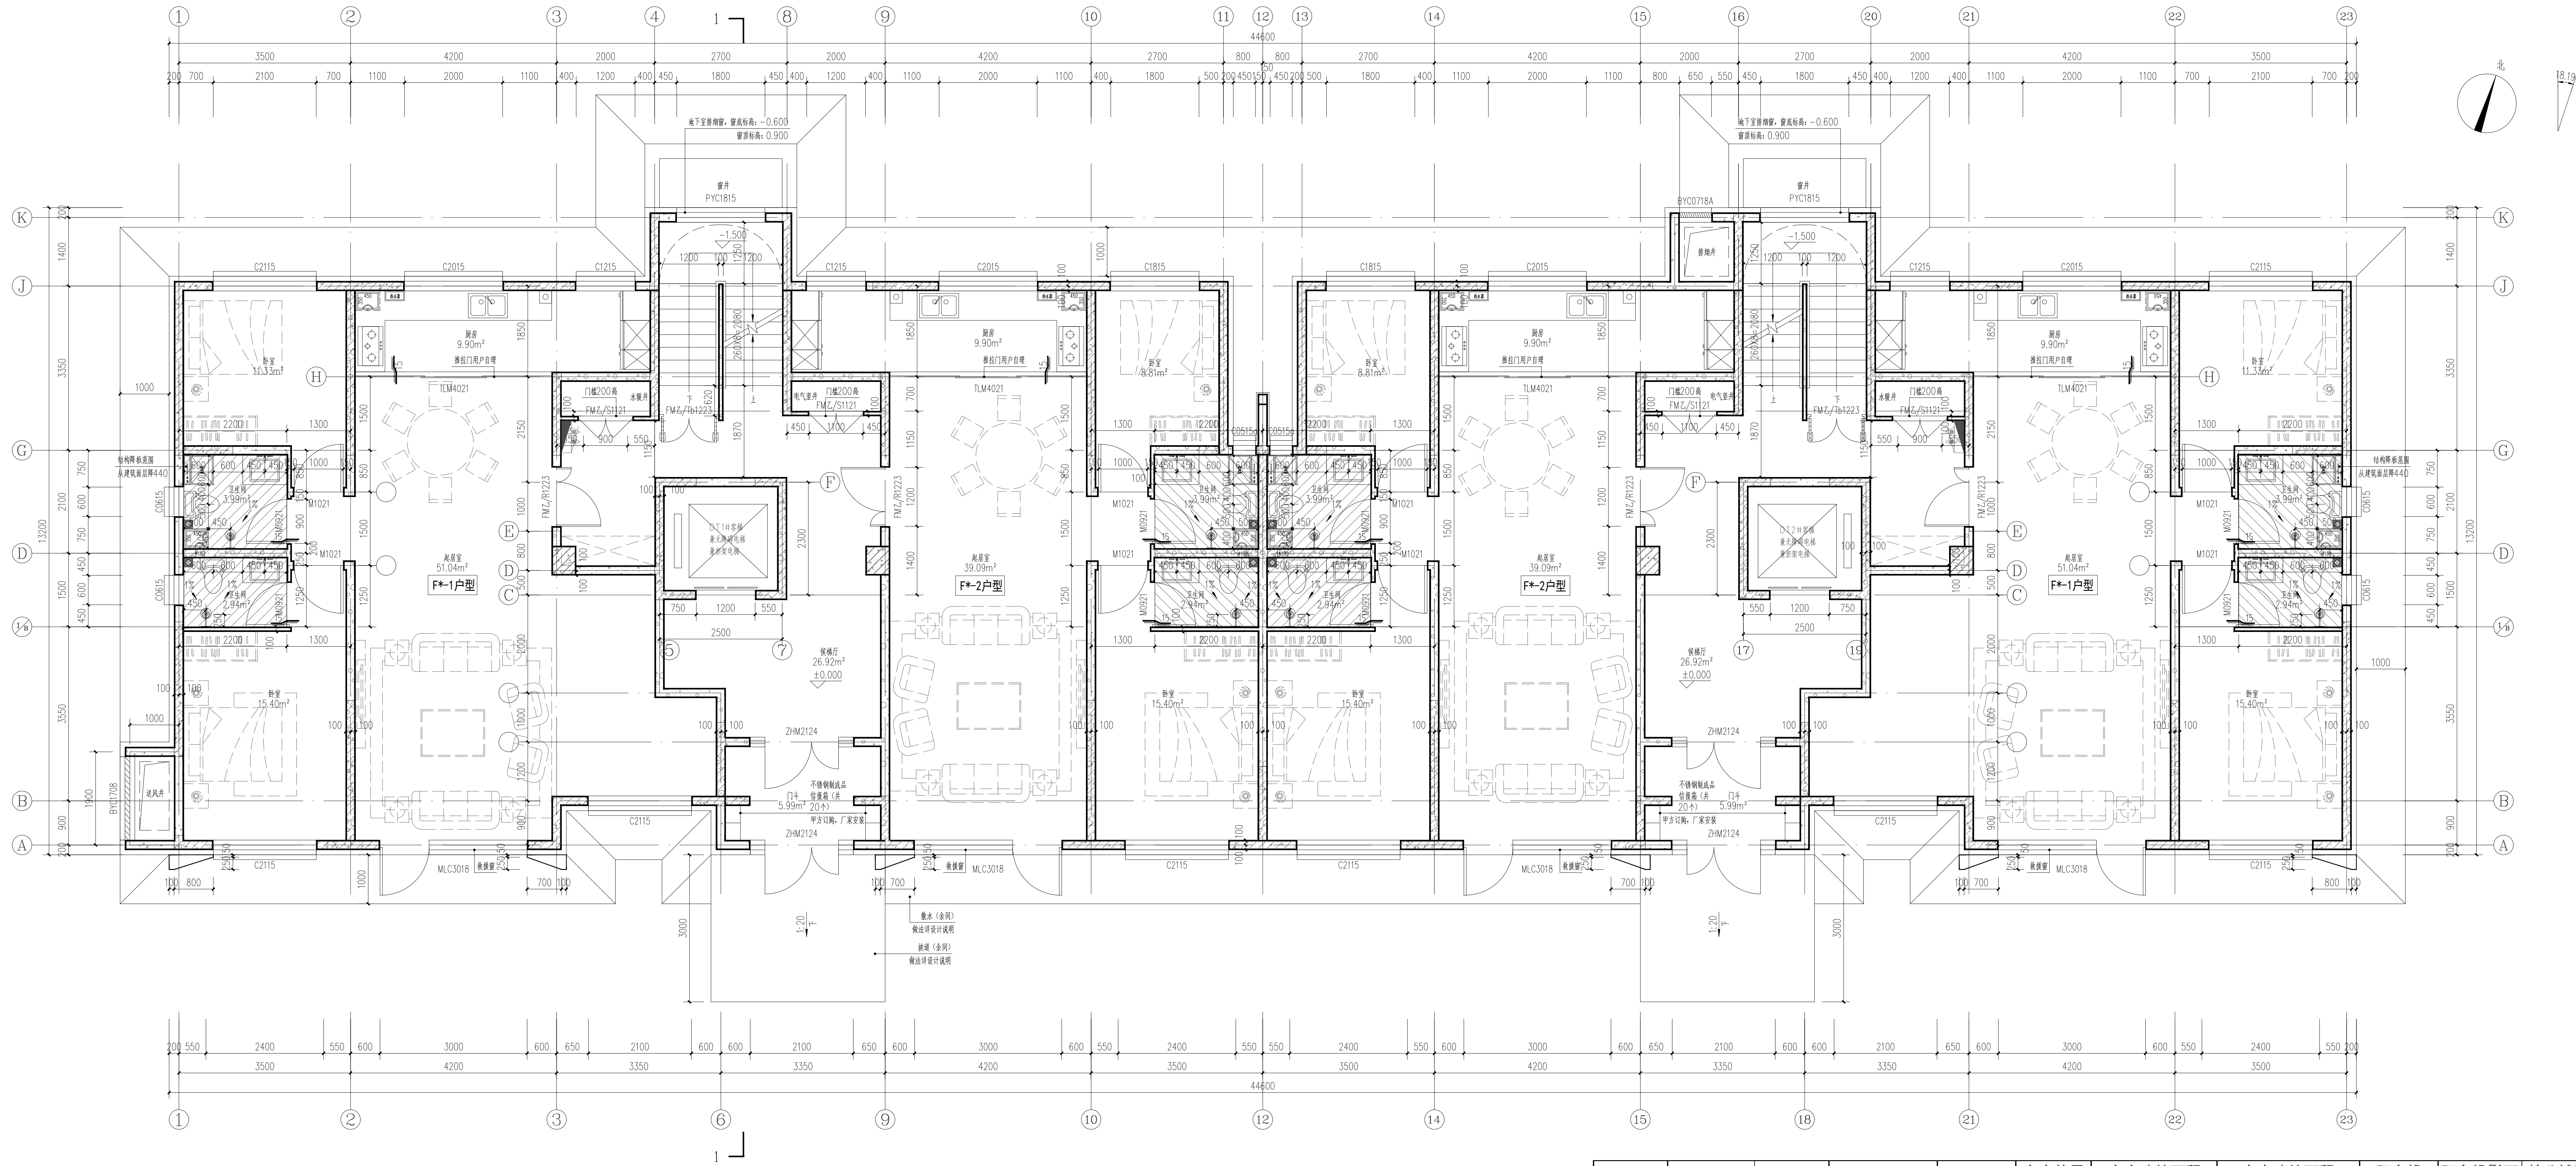

一层平面图 1:50

本层建筑面积: 525.63m²
总建筑面积: 6248.29m²
地上建筑面积: 5251.33m²
地下建筑面积: 996.96m²

栋公摊面 积计算	套型编号	户数	套型	建筑面积	套内使用 建筑面积	套内建筑面积 (含阳台面积)	套内建筑面积 (不含阳台面积)	阳台投 影面积	阳台投影面 积比	栋公摊面 积	栋公摊
	F*-1户型	2	两房两厅两卫	131.99	94.60	110.75	110.75	0.00	0.00%	21.24	
	F*-2户型	2	两房两厅两卫	110.74	80.13	92.92	92.92	0.00	0.00%	17.82	
	F*-3户型	18	两房两厅两卫	134.99	97.10	113.27	113.27	0.00	0.00%	21.72	
	F*-4户型	18	两房两厅两卫	129.78	94.58	108.90	108.90	0.00	0.00%	20.88	
	合计	40	/	5251.33	/	4406.40	4406.40	0.00	0.00%	844.93	16.09

中华人民共和国一级注册建筑师
姓名: 李亮
注册号: 51A0246-002
有效期至: 2028年05月

四川省建设工程设计出图专用章
Yong Zhong Engineering Management (Group) Co., Ltd.
甲级工程设计证书编号:A151027583
有效期: 2022-05-08
比例: 1:100
图号: 建筑-08
版本号: 第一版