


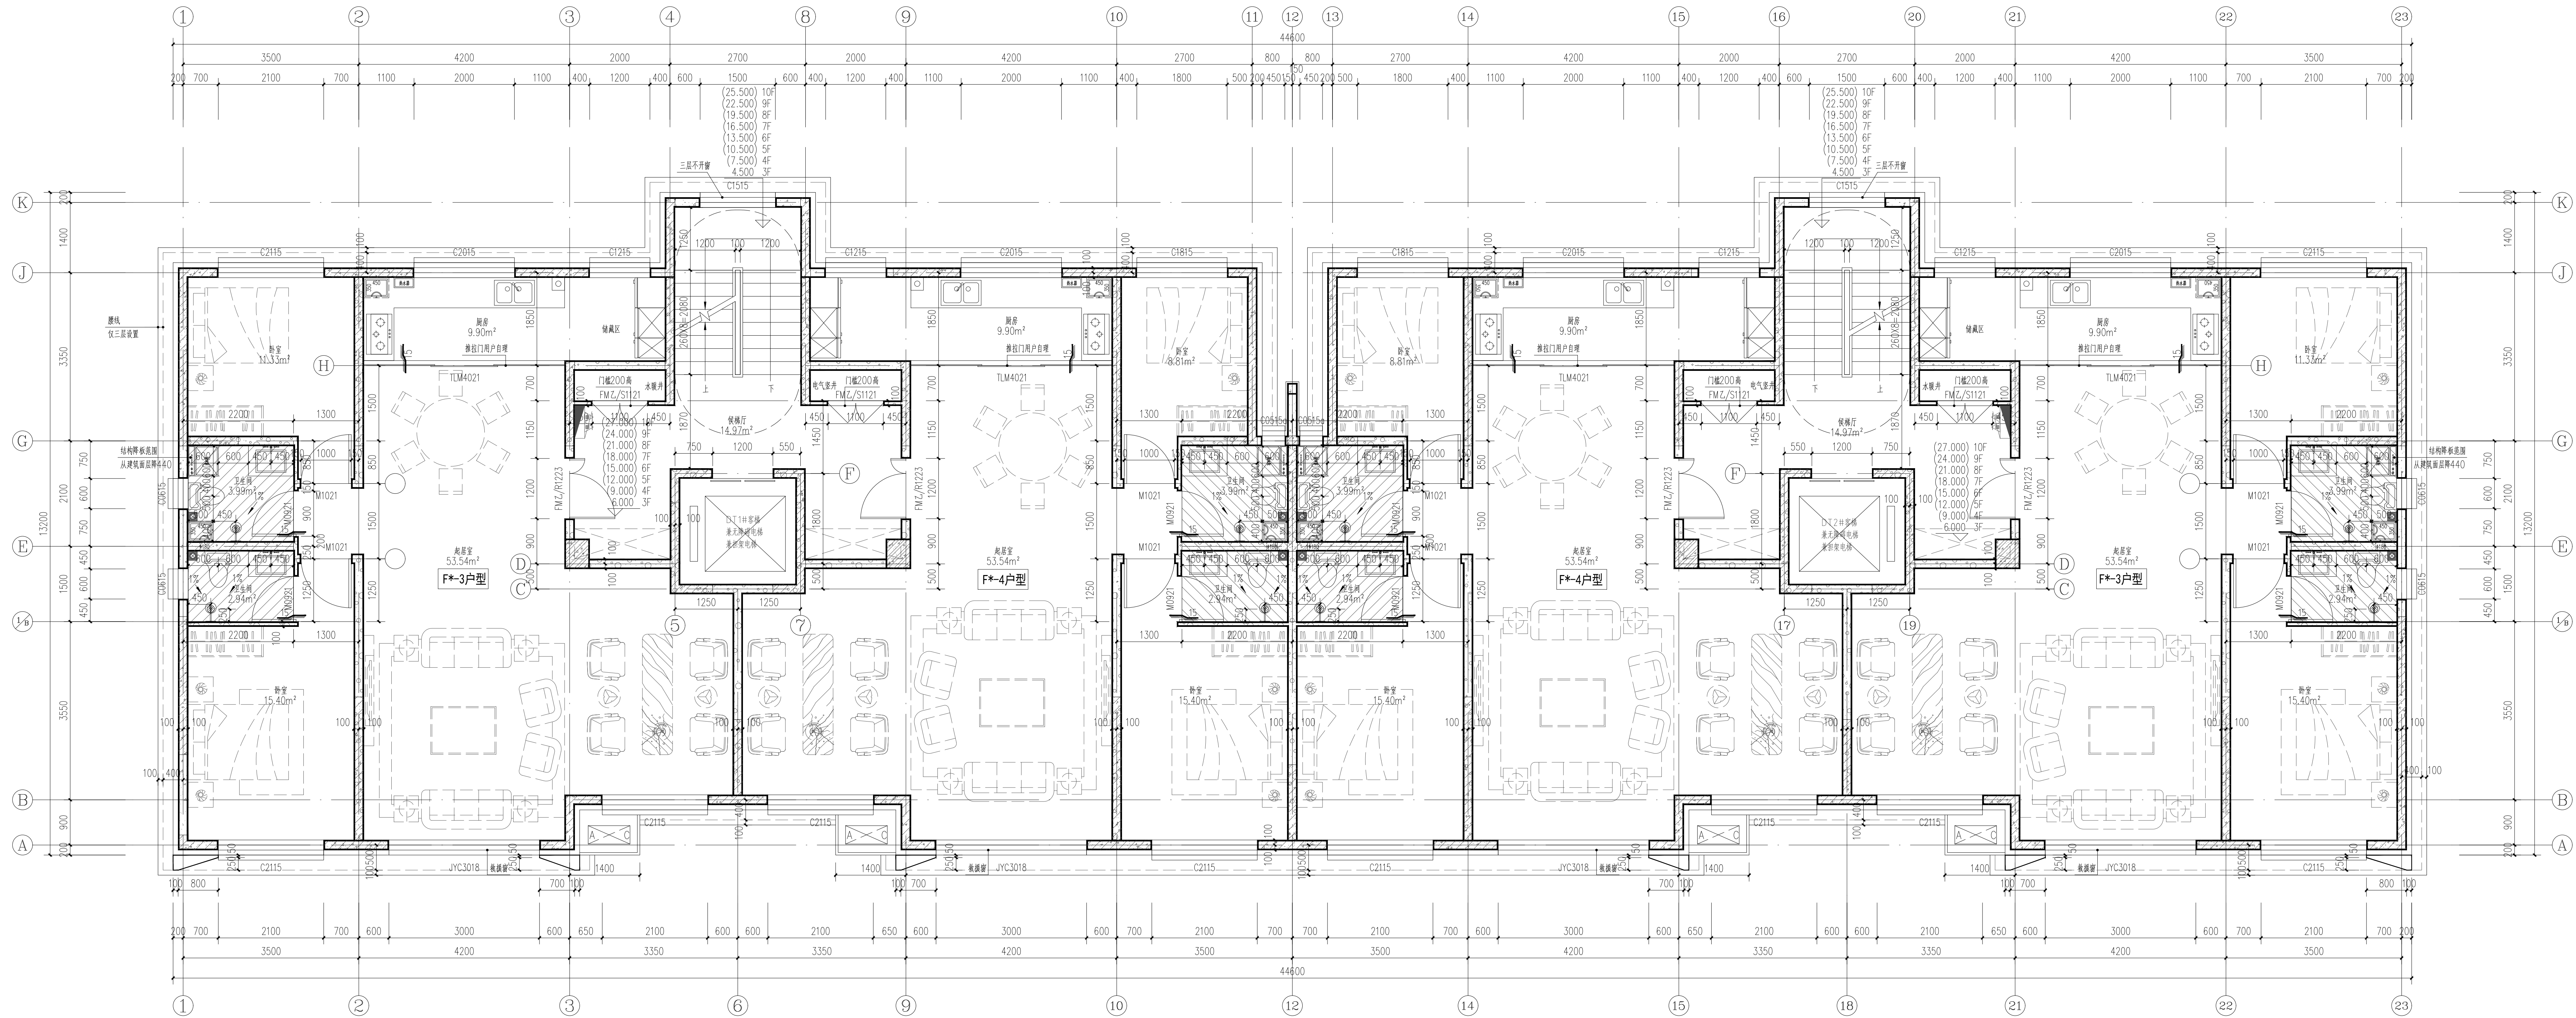

三层至十层平面图 1:50

本层建筑面积: 519.60m²
总建筑面积: 6248.29m²

注册执业章	
姓名: 李 亮	NAME
注册证书号码: 20246500624	REGISTRATION CERTIFICATE NO.
注册印章号码: 51A0246-002	REGISTERED SEAL NO.
建设单位: 新疆知度房地产开发有限公司	CLIENT
工程名称: 阿勒泰市御景园商住一期建设项目	PROJECT
子项名称: 10#住宅楼	SUB ITEM
设计号: YXJ-2023-07-10	PROJECT NO.
图名: 三层至十层平面图	IMG. TITLE

项目负责人	李 亮	李 亮
审 定	吴林英	吴林英
审 核	王 江	王 江
专业负责人	李 亮	李 亮
校 对	朱沪祺	朱沪祺
设 计	吴 迪	吴 迪

中华人民共和国一级注册建筑师
姓名: 李 亮
注册号: 51A0246-002
有效期至: 2028年05月

四川省建设工程设计出图专用章
永忠工程管理（集团）有限公司
勘察设计行业（河道整治、引调水、
城市防洪、灌溉排涝）专业乙级、
建筑行业（建筑工程）甲级
证书编号:A151A02463 有效期至:2031年02月11日