


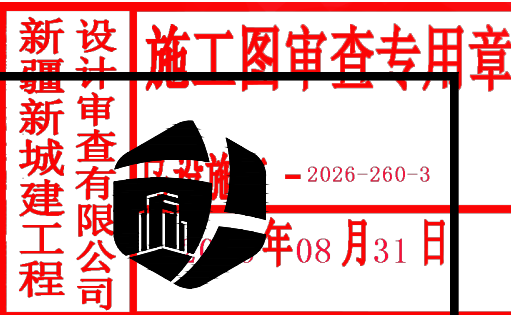

永忠工程管理（集团）有限公司

Yong Zhong Engineering Management (Group) Co., Ltd.

甲级工程设计证书编号:A151027583

合作设计-顾问单位 CONSULTING ARCHITECT

设计部门 新疆分公司

电 话 18999878562

说 明:

1、本图版权为本设计院拥有，任何人士如未获允许不得翻印任何部分。

2、所有尺寸均以标注为准，图上自行量取无效。

3、本图需加盖本设计院工程设计出图专用章及注册章方有效。

4、本套图纸需经国家有关部门批准方可施工。

平面示意: KEY PLAN


注册执业章	
姓 名: 李 亮	NAME
注册证书号码:20246500624	REGISTRATION CERTIFICATE NO.
注册印章号码:51A0246-002	REGISTERED SIGNATURE NO.
建设单位:新疆知茂房地产开发有限公司	CLIENT
工程名称:阿勒泰市御景园商住一期建设项目	PROJECT
子项名称:10#住宅楼	SUB ITEM
设计号:YZXJ-2023-07-10	PROJECT NO.
图 名:	FIG. TITLE
1-1剖面图	

项目负责人	李 亮	李亮
审 定	莫林英	莫林英
审 核	王 江	王江
专业负责人	李 亮	李亮
校 对	朱沪凯	朱沪凯
设 计	吴 迪	吴迪

中华人民共和国一级注册建筑师	
姓 名: 李 亮	姓名: 李亮
注册号: 51A0246-002	注册号: 51A0246-002
有效期: 至2028年05月	有效期: 至2028年05月

四川省建设工程设计出图专用章	
永忠工程管理（集团）有限公司	
专业类别:水利行业（河道整治、引调水、城市防洪、灌溉排涝）专业乙级；建筑行业（建筑工程）甲级	
章编号:A151A02463 有效期至:2031年02月11日	

比例:1:100	SCALE	图号: 建施-15	FIG. NO.
版本号:	第一版	VERSION	

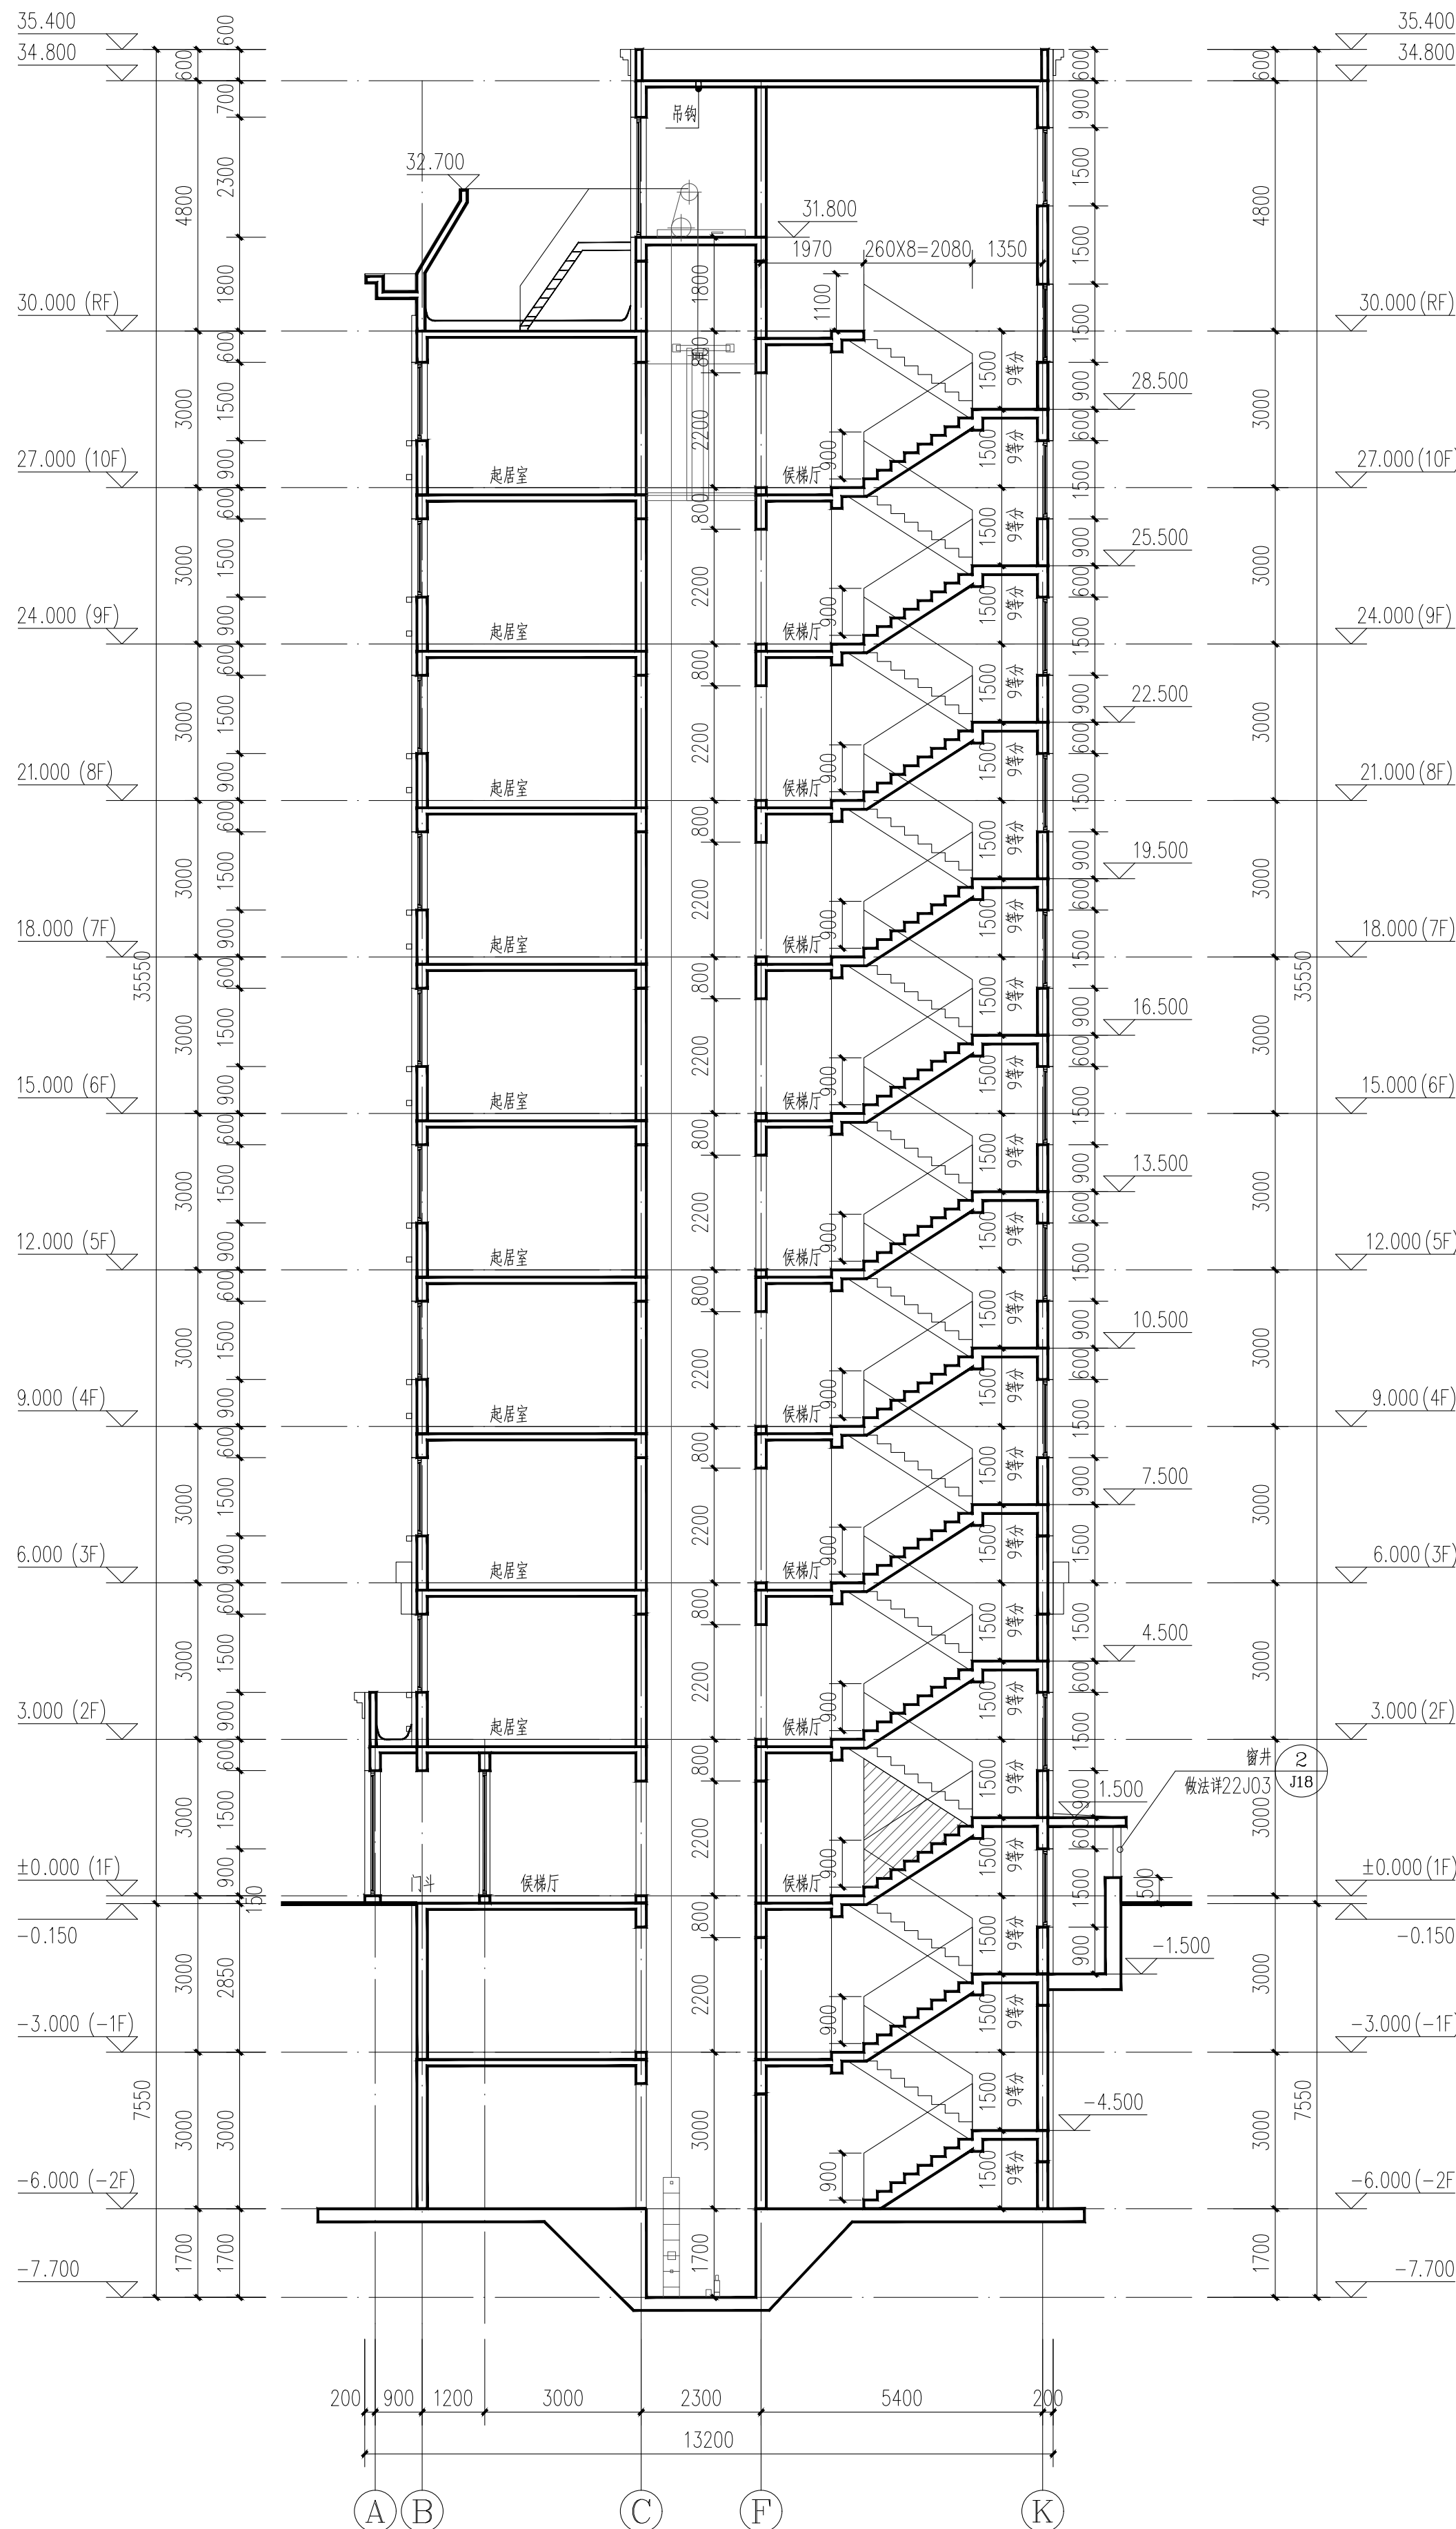

1-1剖面图 1:100