

新疆
设计
审查
有限
公司
工程

施工图审查专用章

乌设施审 - 2026-260-3

2026年08月31日



永忠工程管理（集团）有限公司

Yong Zhong Engineering Management (Group)
Co., Ltd.

建设部设计证书编号：★ NO:A151027583

暖通计算书

建设单位：新疆如茂房地产开发有限公司

工程名称：阿勒泰市御景园商住一期建设项目-10#住宅楼

工号：YZXJ-2023-07-1

审核：张玉
注册号：5102758-CN005
有效期：至2027年12月

校对：张玉

设计：张玉

2026年08月

四川省建设工程设计出图专用章

永忠工程管理（集团）有限公司
资质等级范围：水利行业（河道整治、引调水、
城市防洪、灌溉排涝）专业乙级；
建筑行业（建筑工程）甲级

资质证书编号：A151A02463 有效期至：2031年02月11日

新建工程1 热负荷计算书_工程信息及计算依据

一. 工程概况

工程名称	新建工程1
工程编号	XJGC001
建设单位	房地产开发公司
设计单位	设计院
工程地点	新疆-阿勒泰0
工程总面积 (m2)	4760.76
工程总热负荷 (KW)	318.23
工程热指标 (w/m2)	66.84
编制人	
校对入	
日期	2026年8月27日

二. 室外参数

冬季室外供暖计算干球温度 (℃)	冬季室外空调计算干球温度 (℃)	冬季最多风向平均风速 (m/s)
-26.4	-29.5	1.2
冬季室外空调相对湿度 (%)	冬季室外大气压 (Pa)	
74	94110	

三. 建筑信息

楼号	总层数	总高度 (m)	总面积 (m2)	总热负荷 (KW)	非空调热负荷 (KW)	非空调热指标 (W/m2)
1号楼	10	30	4760.76	318.23	318.23	66.84

四. 计算依据

1. 通过围护结构的基本耗热量计算公式	
$Q_j = \alpha FK(t_n - t_{wn})$	
Q_j	—基本耗热量, W
K	—传热系数, W/(m² · °C)
F	—计算传热面积, m²
t_n	—冬季室内设计温度, °C
t_{wn}	—采暖室外计算温度, °C
α	—温差修正系数

2. 附加耗热量计算公式	
$Q = Q_j(1 + \beta_{ch} + \beta_f + \beta_{lang} + \beta_m) \cdot (1 + \beta_{fg}) \cdot (1 + \beta_{jan})$	
Q	—考虑各项附加后，某围护的耗热量, W
Q_j	—某围护的基本耗热量, W
β_{ch}	—朝向修正
β_f	—风力修正
β_{lang}	—两面外墙修正
β_m	—窗墙面积比过大修正
β_{fg}	—房高附加
β_{jan}	—间歇附加率
3. 冷风渗透计算	
$Q = 0.28 \cdot C_p \cdot p_{wn} \cdot V \cdot (t_n - t_{wn})$	
Q	—通过门窗冷风渗透耗热量，W
C_p	—干空气的定压质量比热容=1.0056kJ/(kg·℃)
p_{wn}	—采暖室外计算温度下的空气密度，kg/m ³
V	—渗透冷空气量，m ³ /h
t_n	—冬季室内设计温度，℃
t_{wn}	—采暖室外计算温度，℃
(1) 通过门窗缝隙的冷风渗透耗热量计算	
$V = \Sigma (L_0 \cdot l_i \cdot m_b)$	
L_0	—在基准高度单纯风压作用下，不考虑朝向修正和内部隔断的情况时，每米门窗缝隙的理论渗透冷空气量，m ³ /(m·h)
$L_0 = a_l \cdot (p_{wn} \cdot v_0^2/2)^b$	
	a_l —外门窗缝隙渗风系数，m ³ /(m·h·Pa ^b)当无实测数据时，可根据建筑外窗空气渗透性能分级标准采用
	v_0 —基准高度冬季室外最多方向的平均风速，m/s
l_i	—外门窗缝隙长度，应分别按各朝向计算，m
b	—门窗缝隙渗风指数，b = 0.56~0.78。当无实测数据时，可取b=0.67
m	—风压与热压共同作用下，考虑建筑体型、内部隔断和空气流通因素后，不同朝向、不同高度的门窗冷风渗透压差综合修正系数
$m = C_r \cdot C_f \cdot (n^{1/b} + C) \cdot c_h$	
	C_r —热压系数
	C_f —风压差系数，当无实测数据时，可取0.7
	n—渗透冷空气量的朝向修正系数

	C_h —高度修正系数
	$c_h = 0.3 \cdot h^{0.4}$
	h —计算门窗的中心线标高
	C —作用于门窗上的有效热压差与有效风压差之比，按下式计算：
	$C = 70 \cdot (h_z - h) / (c_f \cdot v_0^2 \cdot h^{0.4}) \cdot (t'_n - t_{wn}) / (273 + t'_n)$
	h_z —单纯热压作用下，建筑物中和界标高（m），可取建筑物总高度的二分之一
	t'_n —建筑物内形成热压作用的竖井计算温度（楼梯间温度），℃
(2) 忽略热压及室外风速沿房高的递增，只计入风压作用时的渗风量	
$V = \sum(l \cdot L \cdot n)$	
l	—房间某朝向上的可开启门、窗缝隙的长度，m
L	—每米门窗缝隙的渗风量， $m^3/(m \cdot h)$ ，见表5.1-7（详见实用供热空调设计手册）
n	—渗风量的朝向修正系数，见表5.1-8（详见实用供热空调设计手册）
(3) 换气次数法	
$L = K \cdot Vf$	
L	—房间冷风渗透量， m^3/h
K	—换气次数， $1/h$ ，见表5.1-13（详见实用供热空调设计手册）
Vf	—房间净体积， m^3
(4) 百分比法计算冷风渗透耗热量	
$Q = Q_o \cdot n$	
Q	—通过外门窗冷风渗透耗热量，W
Q_o	—围护结构总耗热量，W
n	—渗透耗热量占围护结构总耗热量的百分率，%
4. 外门开启冲入冷风耗热量计算公式	
$Q = Q_j \cdot \beta_{kq}$	
Q	—通过外门冷风侵入耗热量，W
Q_j	—某围护的基本耗热量，W


鉴定情况: 建设部科技计划项目验收证书 建科验字[2008]第053号

新疆
设计
审查
有限
公司
新城
建
工
程

施工图审查专用章
乌设施审 - 2026-260-3
2026年08月31日

新建工程1 热负荷计算书_简略表

楼号	楼层	房间	面积m2	供暖总热负荷W	供暖室内热负荷(不含户间传热)W	供暖户间传热负荷W	供暖总热指标W/m2	供暖室内热指标(不含户间传热)W/m2			
1	层	1001[卫生]	7.92	783.75	783.75	0.00	98.96	98.96			
		1002[卧室]	12.83	1297.80	1297.80	0.00	101.15	101.15			
		1003[卧室]	17.20	1174.67	1174.67	0.00	68.29	68.29			
		1004[起居]	54.68	3108.88	3108.88	0.00	56.86	56.86			
		1005[厨房]	11.47	1260.75	1260.75	0.00	109.92	109.92			
		1006[楼梯]	41.34	1854.31	1854.31	0.00	44.86	44.86			
		1007[厨房]	11.47	1260.75	1260.75	0.00	109.92	109.92			
		1008[起居]	42.06	2169.90	2169.90	0.00	51.59	51.59			
		1009[卧室]	10.15	1104.54	1104.54	0.00	108.82	108.82			
		1010[卧室]	17.20	965.54	965.54	0.00	56.14	56.14			
		1011[卫生]	7.92	450.12	450.12	0.00	56.83	56.83			
		1012[卫生]	7.92	450.12	450.12	0.00	56.83	56.83			
		1013[卧室]	17.20	965.54	965.54	0.00	56.14	56.14			
		1014[卧室]	10.15	1104.54	1104.54	0.00	108.82	108.82			
		1015[起居]	42.06	2169.90	2169.90	0.00	51.59	51.59			
		1016[厨房]	11.47	973.54	973.54	0.00	84.88	84.88			
		1017[楼梯]	41.34	1757.44	1757.44	0.00	42.51	42.51			
		1018[厨房]	11.47	1260.75	1260.75	0.00	109.92	109.92			
		1019[起居]	54.68	3108.88	3108.88	0.00	56.86	56.86			
		1020[卧室]	12.83	1297.80	1297.80	0.00	101.15	101.15			
		1021[卧室]	17.20	1403.03	1403.03	0.00	81.57	81.57			
		1022[卫生]	7.92	785.45	785.45	0.00	99.17	99.17			
		1层小计	468.48	30707.99	30707.99	0.00	65.55	65.55			
		2001[卫生]	7.92	755.69	755.69	0.00	95.42	95.42			
		2002[卧室]	12.83	1276.61	1276.61	0.00	99.50	99.50			
		2003[卧室]	17.20	1383.92	1383.92	0.00	80.46	80.46			
		2004[起居]	57.18	3084.90	3084.90	0.00	53.95	53.95			
		2005[厨房]	11.47	1226.48	1226.48	0.00	106.93	106.93			
		2006[楼梯]	27.94	1420.14	1420.14	0.00	50.83	50.83			

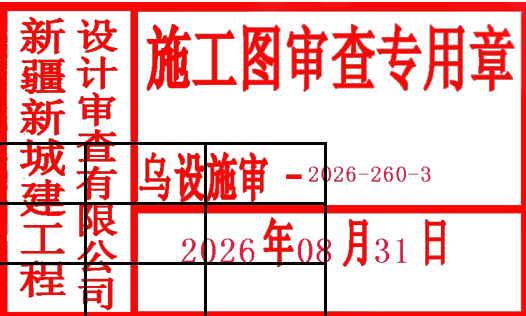

1号楼	2-9层*8	2007[厨房]	11.47	1226.48	1226.48	0.00	106.93	106.93			
		2008[起居]	57.18	3084.90	3084.90	0.00	53.95	53.95			
		2009[卧室]	10.15	1084.81	1084.81	0.00	106.88	106.88			
		2010[卧室]	17.20	1025.94	1025.94	0.00	59.65	59.65			
		2011[卫生]	7.92	436.97	436.97	0.00	55.17	55.17			
		2012[卫生]	7.92	436.97	436.97	0.00	55.17	55.17			
		2013[卧室]	17.20	1025.94	1025.94	0.00	59.65	59.65			
		2014[卧室]	10.15	1084.81	1084.81	0.00	106.88	106.88			
	10层	2015[起居]	57.18	3084.90	3084.90	0.00	53.95	53.95			
		2016[厨房]	11.47	1226.48	1226.48	0.00	106.93	106.93			
		2017[楼梯]	27.94	1420.14	1420.14	0.00	50.83	50.83			
		2018[厨房]	11.47	1226.48	1226.48	0.00	106.93	106.93			
		2019[起居]	57.18	3084.90	3084.90	0.00	53.95	53.95			
		2020[卧室]	12.83	1276.61	1276.61	0.00	99.50	99.50			
		2021[卧室]	17.20	1383.92	1383.92	0.00	80.46	80.46			
		2022[卫生]	7.92	758.38	758.38	0.00	95.76	95.76			
		2-9层小计	476.92	32016.35	32016.35	0.00	67.13	67.13			
		10001[卫生]	7.92	652.52	652.52	0.00	82.39	82.39			
		10002[卧室]	12.83	1238.21	1238.21	0.00	96.51	96.51			
		10003[卧室]	17.20	1366.21	1366.21	0.00	79.43	79.43			
		10004[起居]	57.18	3146.54	3146.54	0.00	55.03	55.03			
		10005[厨房]	11.47	1102.40	1102.40	0.00	96.11	96.11			
		10006[楼梯]	27.94	1482.93	1482.93	0.00	53.08	53.08			
		10007[厨房]	11.47	1102.40	1102.40	0.00	96.11	96.11			
		10008[起居]	57.18	3146.54	3146.54	0.00	55.03	55.03			
		10009[卧室]	10.15	1038.23	1038.23	0.00	102.29	102.29			
		10010[卧室]	17.20	1008.23	1008.23	0.00	58.62	58.62			
		10011[卫生]	7.92	412.87	412.87	0.00	52.13	52.13			
		10012[卫生]	7.92	412.87	412.87	0.00	52.13	52.13			
		10013[卧室]	17.20	1008.23	1008.23	0.00	58.62	58.62			
		10014[卧室]	10.15	1038.23	1038.23	0.00	102.29	102.29			
		10015[起居]	57.18	3146.54	3146.54	0.00	55.03	55.03			
		10016[厨房]	11.47	1102.40	1102.40	0.00	96.11	96.11			

新疆
设计审查有限公司
新城建设工程

施工图审查专用章
乌设施审 - 2026-260-3
2026年08月31日

	10017[楼梯]	27.94	1482.93	1482.93	0.00	53.08	53.08			
	10018[厨房]	11.47	1102.40	1102.40	0.00	96.11	96.11			
	10019[起居]	57.18	3146.54	3146.54	0.00	55.03	55.03			
	10020[卧室]	12.83	1238.21	1238.21	0.00	96.51	96.51			
	10021[卧室]	17.20	1366.21	1366.21	0.00	79.43	79.43			
	10022[卫生]	7.92	652.52	652.52	0.00	82.39	82.39			
	10层小计	476.92	31394.18	31394.18	0.00	65.83	65.83			
	1号楼小计	4760.76	318232.96	318232.96	0.00	66.84	66.84			
	工程合计	4760.76	318232.96	318232.96	0.00	66.84	66.84			

新建工程1 热负荷计算书_详尽表

楼号	楼层	房间	负荷源		总热负荷 (W)	户间传热 量	总热指标 (W/m2)	围护结构 基本耗热 量	朝向修正 率	风力附加 率	附加率	修正后热 负荷	附加率			
					围护结构 耗热量	间歇附加 率	冷风渗透 量	冷风渗透 耗热量	外门冷风 侵入耗热 量							
		1001[卫生间]	房间参数		面积(m2)	高度(m)	室内设计 温度(℃)	室内设计 相对湿度 (%)	放大系数							
					7.92	3.0	20.00	60.00	1.00							
			西外墙	参数	长(m)	宽 (高)(m)	外墙面积 (m2)	外墙净面 积(m2)	传热系数	温差修正 系数						
				5.76	3.0	17.28	15.48	0.34	1.0							
				负荷	232.00	0.0	0.0	244.21	-0.05	0.00	0.0	232.00	0.00			
				统计	232.00	0.00	0.0	0.0	0.0							
			西外墙_嵌	参数	长(m)	宽 (高)(m)	面积(m2)	传热系数	缝隙长度 (m)	渗透系数	安装高度 (m)	温差修正 系数				
				0.45	2.000	0.90	1.4	5.7	0.3	0.90	1.0					
				负荷	145.04	0.0	0.0	58.46	-0.05	0.00	0.0	55.54	0.00			
				统计	145.04	0.00	5.16	89.50	0.0							
			西外墙_嵌	参数	长(m)	宽 (高)(m)	面积(m2)	传热系数	缝隙长度 (m)	渗透系数	安装高度 (m)	温差修正 系数				
				0.45	2.000	0.90	1.4	5.7	0.3	0.90	1.0					
				负荷	145.04	0.0	0.0	58.46	-0.05	0.00	0.0	55.54	0.00			
				统计	145.04	0.00	5.16	89.50	0.0							
			新风 (热)	参数	新风量 m3/h	新风机送 风状态点	热回收方 式									
				9.50	20.0℃ /60.0%	没有热回 收										
				负荷	261.67	0.0	0.0	0.0	0.0	0.0	0.0	261.67	0.0			
				统计	0.0	0.0	0.0	0.0	0.0							
			1001[卫生间]房间小计					783.75	0.00	98.96	361.14	0.0	0.0	0.0	604.75	0.0
								522.08	0.0	10.31	179.00	0.00				
		1002[卧室]	房间参数		面积(m2)	高度(m)	室内设计 温度(℃)	室内设计 相对湿度 (%)	放大系数							
					12.83	3.0	20.00	60.00	1.00							
			西外墙	参数	长(m)	宽 (高)(m)	外墙面积 (m2)	外墙净面 积(m2)	传热系数	温差修正 系数						
				5.36	3.0	16.08	16.08	0.34	1.0							
				负荷	253.68	0.0	0.0	253.68	-0.05	0.00	0.05	253.68	0.00			
				统计	253.68	0.00	0.0	0.0	0.0							
			北外墙	参数	长(m)	宽 (高)(m)	外墙面积 (m2)	外墙净面 积(m2)	传热系数	温差修正 系数						
				5.60	3.0	16.80	13.65	0.34	1.0							
				负荷	247.64	0.0	0.0	215.34	0.10	0.00	0.05	247.64	0.00			
				统计	247.64	0.00	0.0	0.0	0.0							
			北外墙_嵌	参数	长(m)	宽 (高)(m)	面积(m2)	传热系数	缝隙长度 (m)	渗透系数	安装高度 (m)	温差修正 系数				
				1.57	2.000	3.15	1.4	8.7	0.3	0.90	1.0					
				负荷	372.30	0.0	0.0	204.62	0.10	0.00	0.05	235.32	0.00			
				统计	372.30	0.00	7.89	136.98	0.0							
			新风 (热)	参数	新风量 m3/h	新风机送 风状态点	热回收方 式									
				15.40	20.0℃ /60.0%	没有热回 收										
				负荷	424.18	0.0	0.0	0.0	0.0	0.0	0.0	424.18	0.0			
				统计	0.0	0.0	0.0	0.0	0.0							
			1002[卧室]房间小计					1297.80	0.00	101.15	673.64	0.0	0.0	0.0	1160.82	0.0
								873.62	0.0	7.89	136.98	0.00				

1003[卧室]	房间参数		面积(m2)	高度(m)	室内设计温度(℃)	室内设计相对湿度(%)	放大系数	城 建 工 程 有 限 公 司	乌 设 施 审 -2024	2026	年08月	
			17.20	3.0	20.00	60.00	1.00					
	南外墙	参数	长(m)	宽(高)(m)	外墙面积(m2)	外墙净面积(m2)	传热系数	温差修正系数				
			3.50	3.0	10.50	7.35	0.34	1.0				
		负荷统计	98.56	0.0	0.0	115.95	-0.20	0.00	0.05	98.56	0.00	
	98.56		0.00	0.0	0.0	0.0						
	南外窗_嵌	参数	长(m)	宽(高)(m)	面积(m2)	传热系数	缝隙长度(m)	渗透系数	安装高度(m)	温差修正系数		
			1.57	2.000	3.15	1.4	8.7	0.3	0.90	1.0		
		负荷统计	314.50	0.0	0.0	204.62	-0.20	0.00	0.05	173.93	0.00	
			314.50	0.00	8.10	140.57	0.0					
	西外墙	参数	长(m)	宽(高)(m)	外墙面积(m2)	外墙净面积(m2)	传热系数	温差修正系数				
			4.08	3.0	12.24	12.24	0.34	1.0				
		负荷统计	193.10	0.0	0.0	193.10	-0.05	0.00	0.05	193.10	0.00	
			193.10	0.00	0.0	0.0	0.0					
	新风(热)	参数	新风量m3/h	新风机送风状态点	热回收方式							
			20.64	20.0℃/60.0%	没有热回收							
		负荷统计	568.51	0.0	0.0	0.0	0.0	0.0	0.0	568.51	0.0	
			0.0	0.0	0.0	0.0	0.0					
	1003[卧室]房间小计			1174.67	0.00	68.29	513.68	0.0	0.0	0.0	1034.10	0.0
				606.16	0.0	8.10	140.57	0.00				
1004[起居室]	房间参数		面积(m2)	高度(m)	室内设计温度(℃)	室内设计相对湿度(%)	放大系数					
			54.68	3.0	20.00	60.00	1.00					
	南外墙	参数	长(m)	宽(高)(m)	外墙面积(m2)	外墙净面积(m2)	传热系数	温差修正系数				
			7.55	3.0	22.65	15.45	0.34	1.0				
		负荷统计	207.18	0.0	0.0	243.74	-0.20	0.00	0.05	207.18	0.00	
	207.18		0.00	0.0	0.0	0.0						
	南外窗_嵌	参数	长(m)	宽(高)(m)	面积(m2)	传热系数	缝隙长度(m)	渗透系数	安装高度(m)	温差修正系数		
			1.57	2.000	3.15	1.4	8.7	0.3	0.90	1.0		
		负荷统计	314.50	0.0	0.0	204.62	-0.20	0.00	0.05	173.93	0.00	
			314.50	0.00	8.10	140.57	0.0					
	组合负荷源	负荷统计	711.61	0.0	0.0	512.26	0.00	0.00	0.0	711.61	0.00	
			711.61	0.00	0.0	0.0	0.0					
	南外门_子	参数	长(m)	宽(高)(m)	面积(m2)	传热系数	缝隙长度(m)	渗透系数	安装高度(m)	外门开启附加率	温差修正系数	
			1.20	2.000	2.40	2.500	9.2	0.3	1.0	无附加	1.0	
		负荷统计	370.75	0.0	0.0	278.40	-0.20	0.00	0.0	222.72	0.00	
			370.75	0.00	8.53	148.03	0.00					
	南外窗_子	参数	长(m)	宽(高)(m)	面积(m2)	传热系数	缝隙长度(m)	渗透系数	安装高度(m)	温差修正系数		
			1.80	2.000	3.60	1.4	9.4	0.3	0.60	1.0		
		负荷统计	340.86	0.0	0.0	233.86	-0.20	0.00	0.0	187.08	0.00	
			340.86	0.00	8.86	153.77	0.0					
	东外墙	参数	长(m)	宽(高)(m)	外墙面积(m2)	外墙净面积(m2)	传热系数	温差修正系数				
			1.44	3.0	4.32	4.32	0.34	1.0				
		负荷统计	68.15	0.0	0.0	68.15	-0.05	0.00	0.05	68.15	0.00	
	68.15		0.00	0.0	0.0	0.0						
	新风(热)	参数	新风量m3/h	新风机送风状态点	热回收方式							
			65.62	20.0℃/60.0%	没有热回收							
		负荷统计	1807.44	0.0	0.0	0.0	0.0	0.0	0.0	1807.44	0.0	
			0.0	0.0	0.0	0.0	0.0					
	1004[起居室]房间小计			3108.88	0.00	56.86	1028.77	0.0	0.0	0.0	2968.30	0.0

1004[起居室]房间小计		1301.44		0.0		25.49		140.57		0.00				城建工程		有限公司		乌设施审-2024	
1005[厨房]	房间参数		面积(m2)	高度(m)	室内设计温度(℃)	室内设计相对湿度(%)	放大系数											2026年08月	
			11.47	3.0	16.00	60.00	1.00												
	北外墙	参数	长(m)	宽(高)(m)	外墙面积(m2)	外墙净面积(m2)	传热系数	温差修正系数											
			9.92	3.0	29.76	24.96	0.34	1.0											
		负荷统计	395.81	0.0	0.0	359.82	0.10	0.00	0.0	395.81	0.00								
			395.81	0.00	0.0	0.0	0.0												
	北外窗_嵌	参数	长(m)	宽(高)(m)	面积(m2)	传热系数	缝隙长度(m)	渗透系数	安装高度(m)	温差修正系数									
			0.90	2.000	1.80	1.4	6.9	0.3	0.90	1.0									
		负荷统计	216.81	0.0	0.0	106.85	0.10	0.00	0.0	117.53	0.00								
			216.81	0.00	6.26	99.27	0.0												
	北外窗_嵌	参数	长(m)	宽(高)(m)	面积(m2)	传热系数	缝隙长度(m)	渗透系数	安装高度(m)	温差修正系数									
			1.50	2.000	3.00	1.4	8.5	0.3	0.90	1.0									
		负荷统计	318.18	0.0	0.0	178.08	0.10	0.00	0.0	195.89	0.00								
			318.18	0.00	7.71	122.29	0.0												
	新风(热)	参数	新风量m3/h	新风机送风状态点	热回收方式														
			13.76	16.0℃/60.0%	没有热回收														
		负荷统计	329.96	0.0	0.0	0.0	0.0	0.0	0.0	329.96	0.0								
			0.0	0.0	0.0	0.0	0.0												
1005[厨房]房间小计			1260.75	0.00	109.92	644.75	0.0	0.0	0.0	1039.18	0.0								
			930.80	0.0	13.97	221.57	0.00												
1006[楼梯间]	房间参数		面积(m2)	高度(m)	室内设计温度(℃)	室内设计相对湿度(%)	放大系数												
			41.34	3.0	16.00	60.00	1.00												
	东外墙	参数	长(m)	宽(高)(m)	外墙面积(m2)	外墙净面积(m2)	传热系数	温差修正系数											
			2.24	3.0	6.72	6.72	0.34	1.0											
		负荷统计	96.88	0.0	0.0	96.88	-0.05	0.00	0.05	96.88	0.00								
			96.88	0.00	0.0	0.0	0.0												
	北外墙	参数	长(m)	宽(高)(m)	外墙面积(m2)	外墙净面积(m2)	传热系数	温差修正系数											
			4.32	3.0	12.96	10.26	0.34	1.0											
		负荷统计	170.09	0.0	0.0	147.91	0.10	0.00	0.05	170.09	0.00								
			170.09	0.00	0.0	0.0	0.0												
	北外窗_嵌	参数	长(m)	宽(高)(m)	面积(m2)	传热系数	缝隙长度(m)	渗透系数	安装高度(m)	温差修正系数									
			1.35	2.000	2.70	1.4	8.1	0.3	0.90	1.0									
		负荷统计	300.85	0.0	0.0	160.27	0.10	0.00	0.05	184.31	0.00								
			300.85	0.00	7.35	116.54	0.0												
	西外墙	参数	长(m)	宽(高)(m)	外墙面积(m2)	外墙净面积(m2)	传热系数	温差修正系数											
			2.24	3.0	6.72	6.72	0.34	1.0											
		负荷统计	96.88	0.0	0.0	96.88	-0.05	0.00	0.05	96.88	0.00								
			96.88	0.00	0.0	0.0	0.0												
新风(热)	参数	新风量m3/h	新风机送风状态点	热回收方式															
		49.61	16.0℃/60.0%	没有热回收															
	负荷统计	1189.61	0.0	0.0	0.0	0.0	0.0	0.0	1189.61	0.0									
		0.0	0.0	0.0	0.0	0.0													
1006[楼梯间]房间小计			1854.31	0.00	44.86	501.93	0.0	0.0	0.0	1737.77	0.0								
			664.70	0.0	7.35	116.54	0.00												
	房间参数		面积(m2)	高度(m)	室内设计温度(℃)	室内设计相对湿度(%)	放大系数												
			11.47	3.0	16.00	60.00	1.00												

1007[厨房]	北外墙	参数	长(m)	宽(高)(m)	外墙面积(m2)	外墙净面积(m2)	传热系数	温差修正系数	安装高度(m)	温差修正系数		
			9.92	3.0	29.76	24.96	0.34	1.0				
		负荷统计	395.81	0.0	0.0	359.82	0.10	0.00	0.0	395.81	0.00	
			395.81	0.00	0.0	0.0	0.0					
	北外窗_嵌	参数	长(m)	宽(高)(m)	面积(m2)	传热系数	缝隙长度(m)	渗透系数	安装高度(m)	温差修正系数		
			1.50	2.000	3.00	1.4	8.5	0.3				0.90
		负荷统计	318.18	0.0	0.0	178.08	0.10	0.00	0.0	195.89	0.00	
			318.18	0.00	7.71	122.29	0.0					
	北外窗_嵌	参数	长(m)	宽(高)(m)	面积(m2)	传热系数	缝隙长度(m)	渗透系数	安装高度(m)	温差修正系数		
			0.90	2.000	1.80	1.4	6.9	0.3	0.90	1.0		
		负荷统计	216.81	0.0	0.0	106.85	0.10	0.00	0.0	117.53	0.00	
			216.81	0.00	6.26	99.27	0.0					
	新风(热)	参数	新风量m3/h	新风机送风状态点	热回收方式							
			13.76	16.0℃/60.0%	没有热回收							
		负荷统计	329.96	0.0	0.0	0.0	0.0	0.0	0.0	329.96	0.0	
			0.0	0.0	0.0	0.0	0.0					
	1007[厨房]房间小计			1260.75	0.00	109.92	644.75	0.0	0.0	0.0	1039.18	0.0
				930.80	0.0	13.97	221.57	0.00				
1008[起居室]	房间参数		面积(m2)	高度(m)	室内设计温度(℃)	室内设计相对湿度(%)	放大系数					
			42.06	3.0	20.00	60.00	1.00					
	南外墙	参数	长(m)	宽(高)(m)	外墙面积(m2)	外墙净面积(m2)	传热系数	温差修正系数				
			4.20	3.0	12.60	5.40	0.34	1.0				
		负荷统计	68.15	0.0	0.0	85.19	-0.20	0.00	0.0	68.15	0.00	
	68.15		0.00	0.0	0.0	0.0						
	组合负荷源	负荷统计	711.61	0.0	0.0	512.26	0.00	0.00	0.0	711.61	0.00	
		711.61	0.00	0.0	0.0	0.0						
	南外门_子	参数	长(m)	宽(高)(m)	面积(m2)	传热系数	缝隙长度(m)	渗透系数	安装高度(m)	外门开启附加率	温差修正系数	
			1.20	2.000	2.40	2.500	9.2	0.3	1.0	无附加	1.0	
		负荷统计	370.75	0.0	0.0	278.40	-0.20	0.00	0.0	222.72	0.00	
	370.75		0.00	8.53	148.03	0.00						
	南外窗_子	参数	长(m)	宽(高)(m)	面积(m2)	传热系数	缝隙长度(m)	渗透系数	安装高度(m)	温差修正系数		
			1.80	2.000	3.60	1.4	9.4	0.3	0.60	1.0		
		负荷统计	340.86	0.0	0.0	233.86	-0.20	0.00	0.0	187.08	0.00	
	340.86		0.00	8.86	153.77	0.0						
	新风(热)	参数	新风量m3/h	新风机送风状态点	热回收方式							
			50.47	20.0℃/60.0%	没有热回收							
		负荷统计	1390.15	0.0	0.0	0.0	0.0	0.0	0.0	1390.15	0.0	
				0.0	0.0	0.0	0.0	0.0				
1008[起居室]房间小计			2169.90	0.00	51.59	597.45	0.0	0.0	0.0	2169.90	0.0	
			779.76	0.0	17.39	0.00	0.00					
1009[卧室]	房间参数		面积(m2)	高度(m)	室内设计温度(℃)	室内设计相对湿度(%)	放大系数					
			10.15	3.0	20.00	60.00	1.00					
	东外墙	参数	长(m)	宽(高)(m)	外墙面积(m2)	外墙净面积(m2)	传热系数	温差修正系数				
			5.36	3.0	16.08	16.08	0.34	1.0				
		负荷统计	253.68	0.0	0.0	253.68	-0.05	0.00	0.05	253.68	0.00	
	253.68		0.00	0.0	0.0	0.0						
	北外墙	参数	长(m)	宽(高)(m)	外墙面积(m2)	外墙净面积(m2)	传热系数	温差修正系数				
4.32			3.0	12.96	10.26	0.34	1.0					
负荷统计	186.14	0.0	0.0	161.86	0.10	0.00	0.05	186.14	0.00			

1 号 楼 1 层	1009[卧室]	统计	186.14	0.00	0.0	0.0	0.0				
			长(m)	宽 (高)(m)	面积(m2)	传热系数	缝隙长度 (m)	渗透系数	安装高度 (m)	温差修正 系数	
		参数	1.35	2.000	2.70	1.4	8.1	0.3	0.90	201.70	0.00
			329.23	0.0	0.0	175.39	0.10	0.00	0.00		
		负荷统计	329.23	0.00	7.35	127.53	0.0				
		新风 (热)	新风量 m3/h	新风机送 风状态点	热回收方 式						
			12.18	20.0℃ /60.0%	没有热回 收						
			335.49	0.0	0.0	0.0	0.0	0.0	0.0	335.49	0.0
			0.0	0.0	0.0	0.0	0.0				
	1009[卧室]房间小计		1104.54	0.00	108.82	590.93	0.0	0.0	0.0	977.01	0.0
			769.05	0.0	7.35	127.53	0.00				
	1010[卧室]	房间参数	面积(m2)	高度(m)	室内设计 温度(℃)	室内设计 相对湿度 (%)	放大系数				
			17.20	3.0	20.00	60.00	1.00				
		南外墙	参数	长(m)	宽 (高)(m)	外墙面积 (m2)	外墙净面 积(m2)	传热系数	温差修正 系数		
				3.50	3.0	10.50	7.35	0.34	1.0		
			负荷统计	92.76	0.0	0.0	115.95	-0.20	0.00	0.0	92.76
				92.76	0.00	0.0	0.0	0.0			
		南外窗_嵌	参数	长(m)	宽 (高)(m)	面积(m2)	传热系数	缝隙长度 (m)	渗透系数	安装高度 (m)	温差修正 系数
				1.57	2.000	3.15	1.4	8.7	0.3	0.90	1.0
			负荷统计	304.27	0.0	0.0	204.62	-0.20	0.00	0.0	163.70
				304.27	0.00	8.10	140.57	0.0			
		新风 (热)	新风量 m3/h	新风机送 风状态点	热回收方 式						
			20.64	20.0℃ /60.0%	没有热回 收						
			568.51	0.0	0.0	0.0	0.0	0.0	0.0	568.51	0.0
			0.0	0.0	0.0	0.0	0.0				
	1010[卧室]房间小计		965.54	0.00	56.14	320.58	0.0	0.0	0.0	824.97	0.0
			397.04	0.0	8.10	140.57	0.00				
	1011[卫生间]	房间参数	面积(m2)	高度(m)	室内设计 温度(℃)	室内设计 相对湿度 (%)	放大系数				
			7.92	3.0	20.00	60.00	1.00				
		北外墙	参数	长(m)	宽 (高)(m)	外墙面积 (m2)	外墙净面 积(m2)	传热系数	温差修正 系数		
				1.28	3.0	3.84	3.16	0.34	1.0		
			负荷统计	54.84	0.0	0.0	49.85	0.10	0.00	0.0	54.84
				54.84	0.00	0.0	0.0	0.0			
		北外窗_嵌	参数	长(m)	宽 (高)(m)	面积(m2)	传热系数	缝隙长度 (m)	渗透系数	安装高度 (m)	温差修正 系数
				0.34	2.000	0.68	1.4	5.4	0.3	0.90	1.0
			负荷统计	133.61	0.0	0.0	44.17	0.10	0.00	0.0	48.59
				133.61	0.00	4.90	85.02	0.0			
		新风 (热)	新风量 m3/h	新风机送 风状态点	热回收方 式						
			9.50	20.0℃ /60.0%	没有热回 收						
			261.67	0.0	0.0	0.0	0.0	0.0	0.0	261.67	0.0
			0.0	0.0	0.0	0.0	0.0				
	1011[卫生间]房间小计		450.12	0.00	56.83	94.02	0.0	0.0	0.0	365.10	0.0
			188.45	0.0	4.90	85.02	0.00				
		房间参数	面积(m2)	高度(m)	室内设计 温度(℃)	室内设计 相对湿度 (%)	放大系数				
			7.92	3.0	20.00	60.00	1.00				
		北外墙	参数	长(m)	宽 (高)(m)	外墙面积 (m2)	外墙净面 积(m2)	传热系数	温差修正 系数		
				1.28	3.0	3.84	3.16	0.34	1.0		

1012[卫生间]	北外窗_嵌	负荷统计	54.84	0.0	0.0	49.85	0.10	0.00	0.0	54.84	0.00
		参数	长(m)	宽(高)(m)	面积(m2)	传热系数	缝隙长度(m)	渗透系数	安装高度(m)	温差修正系数	
			0.34	2.000	0.68	1.4	5.4	0.3	0.90	1.0	
		负荷统计	133.61	0.0	0.0	44.17	0.10	0.00	0.0	48.59	0.00
	新风(热)	参数	新风量m3/h	新风机送风状态点	热回收方式						
			9.50	20.0℃/60.0%	没有热回收						
		负荷统计	261.67	0.0	0.0	0.0	0.0	0.0	0.0	261.67	0.0
			0.0	0.0	0.0	0.0	0.0				
	1012[卫生间]房间小计		450.12	0.00	56.83	94.02	0.0	0.0	0.0	365.10	0.0
			188.45	0.0	4.90	85.02	0.00				
1013[卧室]	房间参数		面积(m2)	高度(m)	室内设计温度(℃)	室内设计相对湿度(%)	放大系数				
			17.20	3.0	20.00	60.00	1.00				
	南外墙	参数	长(m)	宽(高)(m)	外墙面积(m2)	外墙净面积(m2)	传热系数	温差修正系数			
			3.50	3.0	10.50	7.35	0.34	1.0			
		负荷统计	92.76	0.0	0.0	115.95	-0.20	0.00	0.0	92.76	0.00
			92.76	0.00	0.0	0.0	0.0				
	南外窗_嵌	参数	长(m)	宽(高)(m)	面积(m2)	传热系数	缝隙长度(m)	渗透系数	安装高度(m)	温差修正系数	
			1.57	2.000	3.15	1.4	8.7	0.3	0.90	1.0	
		负荷统计	304.27	0.0	0.0	204.62	-0.20	0.00	0.0	163.70	0.00
			304.27	0.00	8.10	140.57	0.0				
	新风(热)	参数	新风量m3/h	新风机送风状态点	热回收方式						
			20.64	20.0℃/60.0%	没有热回收						
		负荷统计	568.51	0.0	0.0	0.0	0.0	0.0	0.0	568.51	0.0
			0.0	0.0	0.0	0.0	0.0				
	1013[卧室]房间小计		965.54	0.00	56.14	320.58	0.0	0.0	0.0	824.97	0.0
			397.04	0.0	8.10	140.57	0.00				
1014[卧室]	房间参数		面积(m2)	高度(m)	室内设计温度(℃)	室内设计相对湿度(%)	放大系数				
			10.15	3.0	20.00	60.00	1.00				
	西外墙	参数	长(m)	宽(高)(m)	外墙面积(m2)	外墙净面积(m2)	传热系数	温差修正系数			
			5.36	3.0	16.08	16.08	0.34	1.0			
		负荷统计	253.68	0.0	0.0	253.68	-0.05	0.00	0.05	253.68	0.00
			253.68	0.00	0.0	0.0	0.0				
	北外墙	参数	长(m)	宽(高)(m)	外墙面积(m2)	外墙净面积(m2)	传热系数	温差修正系数			
			4.32	3.0	12.96	10.26	0.34	1.0			
		负荷统计	186.14	0.0	0.0	161.86	0.10	0.00	0.05	186.14	0.00
			186.14	0.00	0.0	0.0	0.0				
	北外窗_嵌	参数	长(m)	宽(高)(m)	面积(m2)	传热系数	缝隙长度(m)	渗透系数	安装高度(m)	温差修正系数	
			1.35	2.000	2.70	1.4	8.1	0.3	0.90	1.0	
		负荷统计	329.23	0.0	0.0	175.39	0.10	0.00	0.05	201.70	0.00
			329.23	0.00	7.35	127.53	0.0				
	新风(热)	参数	新风量m3/h	新风机送风状态点	热回收方式						
			12.18	20.0℃/60.0%	没有热回收						
		负荷统计	335.49	0.0	0.0	0.0	0.0	0.0	0.0	335.49	0.0
			0.0	0.0	0.0	0.0	0.0				
	1014[卧室]房间小计		1104.54	0.00	108.82	590.93	0.0	0.0	0.0	977.01	0.0
			769.05	0.0	7.35	127.53	0.00				

1015[起居室]	房间参数		面积(m2)	高度(m)	室内设计温度(℃)	室内设计相对湿度(%)	放大系数	城 建 工 程 有 限 公 司	乌 设 施 审 -2024	2026年08月	
			42.06	3.0	20.00	60.00	1.00				
	南外墙	参数	长(m)	宽(高)(m)	外墙面积(m2)	外墙净面积(m2)	传热系数	温差修正系数			
			4.20	3.0	12.60	5.40	0.34	1.0			
		负荷统计	68.15	0.0	0.0	85.19	-0.20	0.00	0.0	68.15	0.00
			68.15	0.00	0.0	0.0	0.0				
	组合负荷源	负荷统计	711.61	0.0	0.0	512.26	0.00	0.00	0.0	711.61	0.00
			711.61	0.00	0.0	0.0	0.0				
	南外门_子	参数	长(m)	宽(高)(m)	面积(m2)	传热系数	缝隙长度(m)	渗透系数	安装高度(m)	外门开启附加率	温差修正系数
			1.20	2.000	2.40	2.500	9.2	0.3	1.0	无附加	1.0
		负荷统计	370.75	0.0	0.0	278.40	-0.20	0.00	0.0	222.72	0.00
			370.75	0.00	8.53	148.03	0.00				
	南外窗_子	参数	长(m)	宽(高)(m)	面积(m2)	传热系数	缝隙长度(m)	渗透系数	安装高度(m)	温差修正系数	
			1.80	2.000	3.60	1.4	9.4	0.3	0.60	1.0	
		负荷统计	340.86	0.0	0.0	233.86	-0.20	0.00	0.0	187.08	0.00
			340.86	0.00	8.86	153.77	0.0				
	新风(热)	参数	新风量m3/h	新风机送风状态点	热回收方式						
			50.47	20.0℃/60.0%	没有热回收						
		负荷统计	1390.15	0.0	0.0	0.0	0.0	0.0	0.0	1390.15	0.0
			0.0	0.0	0.0	0.0	0.0				
1015[起居室]房间小计			2169.90	0.00	51.59	597.45	0.0	0.0	0.0	2169.90	0.0
			779.76	0.0	17.39	0.00	0.00				
1016[厨房]	房间参数		面积(m2)	高度(m)	室内设计温度(℃)	室内设计相对湿度(%)	放大系数				
			11.47	3.0	16.00	60.00	1.00				
	北外墙	参数	长(m)	宽(高)(m)	外墙面积(m2)	外墙净面积(m2)	传热系数	温差修正系数			
			7.84	3.0	23.52	20.52	0.34	1.0			
		负荷统计	325.40	0.0	0.0	295.82	0.10	0.00	0.0	325.40	0.00
			325.40	0.00	0.0	0.0	0.0				
	北外窗_嵌	参数	长(m)	宽(高)(m)	面积(m2)	传热系数	缝隙长度(m)	渗透系数	安装高度(m)	温差修正系数	
			1.50	2.000	3.00	1.4	8.5	0.3	0.90	1.0	
		负荷统计	318.18	0.0	0.0	178.08	0.10	0.00	0.0	195.89	0.00
			318.18	0.00	7.71	122.29	0.0				
	新风(热)	参数	新风量m3/h	新风机送风状态点	热回收方式						
			13.76	16.0℃/60.0%	没有热回收						
		负荷统计	329.96	0.0	0.0	0.0	0.0	0.0	0.0	329.96	0.0
			0.0	0.0	0.0	0.0	0.0				
1016[厨房]房间小计			973.54	0.00	84.88	473.90	0.0	0.0	0.0	851.24	0.0
			643.58	0.0	7.71	122.29	0.00				
1017[楼梯间]	房间参数		面积(m2)	高度(m)	室内设计温度(℃)	室内设计相对湿度(%)	放大系数				
			41.34	3.0	16.00	60.00	1.00				
	北外墙	参数	长(m)	宽(高)(m)	外墙面积(m2)	外墙净面积(m2)	传热系数	温差修正系数			
			4.32	3.0	12.96	10.26	0.34	1.0			
		负荷统计	170.09	0.0	0.0	147.91	0.10	0.00	0.05	170.09	0.00
			170.09	0.00	0.0	0.0	0.0				
	北外窗_嵌	参数	长(m)	宽(高)(m)	面积(m2)	传热系数	缝隙长度(m)	渗透系数	安装高度(m)	温差修正系数	
			1.35	2.000	2.70	1.4	8.1	0.3	0.90	1.0	
负荷统计		300.85	0.0	0.0	160.27	0.10	0.00	0.05	184.31	0.00	
		300.85	0.00	7.35	116.54	0.0					

	东外墙	参数	长(m)	宽 (高)(m)	外墙面积 (m2)	外墙净面 积(m2)	传热系数	温差修正 系数	城建工程 有限公司	乌设施审 -2024	96.826 年08月	
			2.24	3.0	6.72	6.72	0.34	1.0				
		负荷 统计	96.88	0.0	0.0	96.88	-0.05	0.00				0.05
			96.88	0.00	0.0	0.0	0.0					
	新风 (热)	参数	新风量 m3/h	新风机送 风状态点	热回收方 式							
49.61			16.0℃ /60.0%	没有热回 收								
负荷 统计		1189.61	0.0	0.0	0.0	0.0	0.0	0.0	1189.61	0.0		
		0.0	0.0	0.0	0.0	0.0						
1017[楼梯间]房间小计			1757.44	0.00	42.51	405.06	0.0	0.0	0.0	1640.90	0.0	
			567.82	0.0	7.35	116.54	0.00					
1018[厨房]	房间参数		面积(m2)	高度(m)	室内设计 温度(℃)	室内设计 相对湿度 (%)	放大系数					
			11.47	3.0	16.00	60.00	1.00					
	北外墙	参数	长(m)	宽 (高)(m)	外墙面积 (m2)	外墙净面 积(m2)	传热系数	温差修正 系数				
			9.92	3.0	29.76	24.96	0.34	1.0				
		负荷 统计	395.81	0.0	0.0	359.82	0.10	0.00	0.0	395.81	0.00	
			395.81	0.00	0.0	0.0	0.0					
	北外窗_嵌	参数	长(m)	宽 (高)(m)	面积(m2)	传热系数	缝隙长度 (m)	渗透系数	安装高度 (m)	温差修正 系数		
			1.50	2.000	3.00	1.4	8.5	0.3	0.90	1.0		
		负荷 统计	318.18	0.0	0.0	178.08	0.10	0.00	0.0	195.89	0.00	
			318.18	0.00	7.71	122.29	0.0					
	北外窗_嵌	参数	长(m)	宽 (高)(m)	面积(m2)	传热系数	缝隙长度 (m)	渗透系数	安装高度 (m)	温差修正 系数		
			0.90	2.000	1.80	1.4	6.9	0.3	0.90	1.0		
		负荷 统计	216.81	0.0	0.0	106.85	0.10	0.00	0.0	117.53	0.00	
			216.81	0.00	6.26	99.27	0.0					
	新风 (热)	参数	新风量 m3/h	新风机送 风状态点	热回收方 式							
			13.76	16.0℃ /60.0%	没有热回 收							
负荷 统计		329.96	0.0	0.0	0.0	0.0	0.0	0.0	329.96	0.0		
		0.0	0.0	0.0	0.0	0.0						
1018[厨房]房间小计			1260.75	0.00	109.92	644.75	0.0	0.0	0.0	1039.18	0.0	
			930.80	0.0	13.97	221.57	0.00					
1019[起居 室]	房间参数		面积(m2)	高度(m)	室内设计 温度(℃)	室内设计 相对湿度 (%)	放大系数					
			54.68	3.0	20.00	60.00	1.00					
	南外墙	参数	长(m)	宽 (高)(m)	外墙面积 (m2)	外墙净面 积(m2)	传热系数	温差修正 系数				
			7.55	3.0	22.65	15.45	0.34	1.0				
		负荷 统计	207.18	0.0	0.0	243.74	-0.20	0.00	0.05	207.18	0.00	
			207.18	0.00	0.0	0.0	0.0					
	南外窗_嵌	参数	长(m)	宽 (高)(m)	面积(m2)	传热系数	缝隙长度 (m)	渗透系数	安装高度 (m)	温差修正 系数		
			1.57	2.000	3.15	1.4	8.7	0.3	0.90	1.0		
		负荷 统计	314.50	0.0	0.0	204.62	-0.20	0.00	0.05	173.93	0.00	
			314.50	0.00	8.10	140.57	0.0					
	组合负 荷源	负荷 统计	711.61	0.0	0.0	512.26	0.00	0.00	0.0	711.61	0.00	
			711.61	0.00	0.0	0.0	0.0					
	南外门_子	参数	长(m)	宽 (高)(m)	面积(m2)	传热系数	缝隙长度 (m)	渗透系数	安装高度 (m)	外门开启 附加率	温差修正 系数	
			1.20	2.000	2.40	2.500	9.2	0.3	1.0	无附加	1.0	
		负荷 统计	370.75	0.0	0.0	278.40	-0.20	0.00	0.0	222.72	0.00	
			370.75	0.00	8.53	148.03	0.00					
南外窗_子	参数	长(m)	宽 (高)(m)	面积(m2)	传热系数	缝隙长度 (m)	渗透系数	安装高度 (m)	温差修正 系数			
		1.80	2.000	3.60	1.4	9.4	0.3	0.60	1.0			
	负荷	340.86	0.0	0.0	233.86	-0.20	0.00	0.0	187.08	0.00		

	西外墙	统计	340.86	0.00	8.86	153.77	0.0	城 建 工 程 有 限 公 司	乌 设 施 审 计 有 限 公 司	2026年08月		
		参数	长(m)	宽 (高)(m)	外墙面积 (m2)	外墙净面 积(m2)	传热系数					温差修正 系数
			1.44	3.0	4.32	4.32	0.34					1.0
		负荷统计	68.15	0.0	0.0	68.15	-0.05					0.00
	68.15		0.00	0.0	0.0	0.0						
	新风 (热)	参数	新风量 m3/h	新风机送 风状态点	热回收方 式							
			65.62	20.0℃ /60.0%	没有热回 收							
		负荷统计	1807.44 0.0	0.0 0.0	0.0 0.0	0.0 0.0	0.0 0.0	0.0 0.0	0.0 0.0	1807.44	0.0	
	1019[起居室]房间小计			3108.88 1301.44	0.00 0.0	56.86 25.49	1028.77 140.57	0.0 0.00	0.0 0.0	0.0 0.0	2968.30	0.0

1020[卧室]	房间参数		面积(m2)	高度(m)	室内设计 温度(℃)	室内设计 相对湿度 (%)	放大系数				
			12.83	3.0	20.00	60.00	1.00				
	东外墙	参数	长(m)	宽 (高)(m)	外墙面积 (m2)	外墙净面 积(m2)	传热系数	温差修正 系数			
			5.36	3.0	16.08	16.08	0.34	1.0			
		负荷统计	253.68	0.0	0.0	253.68	-0.05	0.00	0.05	253.68	0.00
	253.68		0.00	0.0	0.0	0.0					
	北外墙	参数	长(m)	宽 (高)(m)	外墙面积 (m2)	外墙净面 积(m2)	传热系数	温差修正 系数			
			5.60	3.0	16.80	13.65	0.34	1.0			
		负荷统计	247.64	0.0	0.0	215.34	0.10	0.00	0.05	247.64	0.00
	247.64		0.00	0.0	0.0	0.0					
	北外窗_嵌	参数	长(m)	宽 (高)(m)	面积(m2)	传热系数	缝隙长度 (m)	渗透系数	安装高度 (m)	温差修正 系数	
			1.57	2.000	3.15	1.4	8.7	0.3	0.90	1.0	
		负荷统计	372.30	0.0	0.0	204.62	0.10	0.00	0.05	235.32	0.00
	372.30		0.00	7.89	136.98	0.0					
	新风 (热)	参数	新风量 m3/h	新风机送 风状态点	热回收方 式						
			15.40	20.0℃ /60.0%	没有热回 收						
		负荷统计	424.18 0.0	0.0 0.0	0.0 0.0	0.0 0.0	0.0 0.0	0.0 0.0	0.0 0.0	424.18	0.0
	1020[卧室]房间小计			1297.80 873.62	0.00 0.0	101.15 7.89	673.64 136.98	0.0 0.00	0.0 0.0	0.0 0.0	1160.82

1021[卧室]	房间参数		面积(m2)	高度(m)	室内设计 温度(℃)	室内设计 相对湿度 (%)	放大系数				
			17.20	3.0	20.00	60.00	1.00				
	南外墙	参数	长(m)	宽 (高)(m)	外墙面积 (m2)	外墙净面 积(m2)	传热系数	温差修正 系数			
			5.60	3.0	16.80	13.65	0.34	1.0			
		负荷统计	183.04	0.0	0.0	215.34	-0.20	0.00	0.05	183.04	0.00
	183.04		0.00	0.0	0.0	0.0					
	南外窗_嵌	参数	长(m)	宽 (高)(m)	面积(m2)	传热系数	缝隙长度 (m)	渗透系数	安装高度 (m)	温差修正 系数	
			1.57	2.000	3.15	1.4	8.7	0.3	0.90	1.0	
		负荷统计	314.50	0.0	0.0	204.62	-0.20	0.00	0.05	173.93	0.00
	314.50		0.00	8.10	140.57	0.0					
	东外墙	参数	长(m)	宽 (高)(m)	外墙面积 (m2)	外墙净面 积(m2)	传热系数	温差修正 系数			
			7.12	3.0	21.36	21.36	0.34	1.0			
		负荷统计	336.98	0.0	0.0	336.98	-0.05	0.00	0.05	336.98	0.00
	336.98		0.00	0.0	0.0	0.0					
	新风 (热)	参数	新风量 m3/h	新风机送 风状态点	热回收方 式						
			20.64	20.0℃ /60.0%	没有热回 收						
		负荷	568.51	0.0	0.0	0.0	0.0	0.0	0.0	568.51	0.0

		统计	0.0	0.0	0.0	0.0	0.0			2026年08月	
1021[卧室]房间小计			1403.03	0.00	81.57	756.94	0.0	0.0	0.0		
			834.52	0.0	8.10	140.57	0.00				
1022[卫生间]	房间参数		面积(m2)	高度(m)	室内设计温度(℃)	室内设计相对湿度(%)	放大系数				
			7.92	3.0	20.00	60.00	1.00				
	东外墙	参数	长(m)	宽(高)(m)	外墙面积(m2)	外墙净面积(m2)	传热系数	温差修正系数			
			5.76	3.0	17.28	15.48	0.34	1.0			
		负荷统计	232.00	0.0	0.0	244.21	-0.05	0.00	0.0	232.00	0.00
			232.00	0.00	0.0	0.0	0.0				
	东外墙_嵌	参数	长(m)	宽(高)(m)	面积(m2)	传热系数	缝隙长度(m)	渗透系数	安装高度(m)	温差修正系数	
			0.45	2.000	0.90	1.4	5.7	0.3	0.90	1.0	
		负荷统计	145.89	0.0	0.0	58.46	-0.05	0.00	0.0	55.54	0.00
			145.89	0.00	5.21	90.35	0.0				
	东外墙_嵌	参数	长(m)	宽(高)(m)	面积(m2)	传热系数	缝隙长度(m)	渗透系数	安装高度(m)	温差修正系数	
			0.45	2.000	0.90	1.4	5.7	0.3	0.90	1.0	
		负荷统计	145.89	0.0	0.0	58.46	-0.05	0.00	0.0	55.54	0.00
			145.89	0.00	5.21	90.35	0.0				
	新风(热)	参数	新风量m3/h	新风机送风状态点	热回收方式						
			9.50	20.0℃/60.0%	没有热回收						
		负荷统计	261.67	0.0	0.0	0.0	0.0	0.0	0.0	261.67	0.0
			0.0	0.0	0.0	0.0	0.0				
1022[卫生间]房间小计			785.45	0.00	99.17	361.14	0.0	0.0	0.0	604.75	0.0
			523.78	0.0	10.41	180.69	0.00				
1层小计			30707.99	0.00	65.55	11918.83	0.0	0.0	0.0	27785.70	0.0
			15773.75	0.0	243.45	2922.29	0.00				
2001[卫生间]	房间参数		面积(m2)	高度(m)	室内设计温度(℃)	室内设计相对湿度(%)	放大系数				
			7.92	3.0	20.00	60.00	1.00				
	西外墙	参数	长(m)	宽(高)(m)	外墙面积(m2)	外墙净面积(m2)	传热系数	温差修正系数			
			5.76	3.0	17.28	15.48	0.34	1.0			
		负荷统计	232.00	0.0	0.0	244.21	-0.05	0.00	0.0	232.00	0.00
			232.00	0.00	0.0	0.0	0.0				
	西外墙_嵌	参数	长(m)	宽(高)(m)	面积(m2)	传热系数	缝隙长度(m)	渗透系数	安装高度(m)	温差修正系数	
			0.45	2.000	0.90	1.4	5.7	0.3	0.90	1.0	
		负荷统计	131.01	0.0	0.0	58.46	-0.05	0.00	0.0	55.54	0.00
			131.01	0.00	4.35	75.47	0.0				
	西外墙_嵌	参数	长(m)	宽(高)(m)	面积(m2)	传热系数	缝隙长度(m)	渗透系数	安装高度(m)	温差修正系数	
			0.45	2.000	0.90	1.4	5.7	0.3	0.90	1.0	
		负荷统计	131.01	0.0	0.0	58.46	-0.05	0.00	0.0	55.54	0.00
			131.01	0.00	4.35	75.47	0.0				
	新风(热)	参数	新风量m3/h	新风机送风状态点	热回收方式						
			9.50	20.0℃/60.0%	没有热回收						
		负荷统计	261.67	0.0	0.0	0.0	0.0	0.0	0.0	261.67	0.0
			0.0	0.0	0.0	0.0	0.0				
2001[卫生间]房间小计			755.69	0.00	95.42	361.14	0.0	0.0	0.0	604.75	0.0
			494.03	0.0	8.70	150.94	0.00				
	房间参数		面积(m2)	高度(m)	室内设计温度(℃)	室内设计相对湿度(%)	放大系数				
			12.83	3.0	20.00	60.00	1.00				
		参数	长(m)	宽(高)(m)	外墙面积(m2)	外墙净面积(m2)	传热系数	温差修正系数			

2002[卧室]	西外墙		5.36	3.0	16.08	16.08	0.34	1.0	城建工程有限公司	乌孜施市	2026年08月			
		负荷统计	253.68	0.0	0.0	253.68	-0.05	0.00				0.05	253.68	0.00
			253.68	0.00	0.0	0.0	0.0							
	北外墙	参数	长(m)	宽(高)(m)	外墙面积(m2)	外墙净面积(m2)	传热系数	温差修正系数						
			5.60	3.0	16.80	13.65	0.34	1.0						
		负荷统计	247.64	0.0	0.0	215.34	0.10	0.00	0.05	247.64	0.00			
				247.64	0.00	0.0	0.0	0.0						
	北外墙_嵌	参数	长(m)	宽(高)(m)	面积(m2)	传热系数	缝隙长度(m)	渗透系数	安装高度(m)	温差修正系数				
			1.57	2.000	3.15	1.4	8.7	0.3	0.90	1.0				
		负荷统计	351.11	0.0	0.0	204.62	0.10	0.00	0.05	235.32	0.00			
				351.11	0.00	6.67	115.79	0.0						
	新风(热)	参数	新风量m3/h	新风机送风状态点	热回收方式									
			15.40	20.0℃/60.0%	没有热回收									
		负荷统计	424.18	0.0	0.0	0.0	0.0	0.0	0.0	424.18	0.0			
				0.0	0.0	0.0	0.0							
2002[卧室]房间小计			1276.61	0.00	99.50	673.64	0.0	0.0	0.0	1160.82	0.0			
			852.43	0.0	6.67	115.79	0.00							
2003[卧室]	房间参数		面积(m2)	高度(m)	室内设计温度(℃)	室内设计相对湿度(%)	放大系数							
			17.20	3.0	20.00	60.00	1.00							
	南外墙	参数	长(m)	宽(高)(m)	外墙面积(m2)	外墙净面积(m2)	传热系数	温差修正系数						
			5.60	3.0	16.80	13.65	0.34	1.0						
		负荷统计	183.04	0.0	0.0	215.34	-0.20	0.00	0.05	183.04	0.00			
				183.04	0.00	0.0	0.0	0.0						
	南外墙_嵌	参数	长(m)	宽(高)(m)	面积(m2)	传热系数	缝隙长度(m)	渗透系数	安装高度(m)	温差修正系数				
			1.57	2.000	3.15	1.4	8.7	0.3	0.90	1.0				
		负荷统计	295.39	0.0	0.0	204.62	-0.20	0.00	0.05	173.93	0.00			
				295.39	0.00	7.00	121.46	0.0						
	西外墙	参数	长(m)	宽(高)(m)	外墙面积(m2)	外墙净面积(m2)	传热系数	温差修正系数						
			7.12	3.0	21.36	21.36	0.34	1.0						
		负荷统计	336.98	0.0	0.0	336.98	-0.05	0.00	0.05	336.98	0.00			
				336.98	0.00	0.0	0.0	0.0						
	新风(热)	参数	新风量m3/h	新风机送风状态点	热回收方式									
			20.64	20.0℃/60.0%	没有热回收									
		负荷统计	568.51	0.0	0.0	0.0	0.0	0.0	0.0	568.51	0.0			
				0.0	0.0	0.0	0.0							
2003[卧室]房间小计			1383.92	0.00	80.46	756.94	0.0	0.0	0.0	1262.45	0.0			
			815.41	0.0	7.00	121.46	0.00							
2004[起居室]	房间参数		面积(m2)	高度(m)	室内设计温度(℃)	室内设计相对湿度(%)	放大系数							
			57.18	3.0	20.00	60.00	1.00							
	南外墙	参数	长(m)	宽(高)(m)	外墙面积(m2)	外墙净面积(m2)	传热系数	温差修正系数						
			12.08	3.0	36.24	27.69	0.34	1.0						
		负荷统计	371.31	0.0	0.0	436.84	-0.20	0.00	0.05	371.31	0.00			
				371.31	0.00	0.0	0.0	0.0						
	南外墙_嵌	参数	长(m)	宽(高)(m)	面积(m2)	传热系数	缝隙长度(m)	渗透系数	安装高度(m)	温差修正系数				
			2.70	2.000	5.40	1.4	11.4	0.3	0.60	1.0				
		负荷统计	459.97	0.0	0.0	350.78	-0.20	0.00	0.05	298.17	0.00			
				459.97	0.00	9.32	161.81	0.0						
	南外墙_嵌	参数	长(m)	宽(高)(m)	面积(m2)	传热系数	缝隙长度(m)	渗透系数	安装高度(m)	温差修正系数				
			1.57	2.000	3.15	1.4	8.7	0.3	0.90	1.0				

	HX	负荷统计	295.39	0.0	0.0	204.62	-0.20	0.00	城建工程有限公司	0.05	170.88	0.00
			295.39	0.00	7.00	121.46	0.0					
	东外墙	参数	长(m)	宽(高)(m)	外墙面积(m2)	外墙净面积(m2)	传热系数	温差修正系数		2026年08月		
			1.44	3.0	4.32	4.32	0.34	1.0				
		负荷统计	68.15	0.0	0.0	68.15	-0.05	0.00	0.05	68.15	0.00	
			68.15	0.00	0.0	0.0	0.0					
	新风(热)	参数	新风量m3/h	新风机送风状态点	热回收方式							
			68.62	20.0℃/60.0%	没有热回收							
		负荷统计	1890.07	0.0	0.0	0.0	0.0	0.0	0.0	1890.07	0.0	
			0.0	0.0	0.0	0.0	0.0					
2004[起居室]房间小计			3084.90	0.00	53.95	1060.40	0.0	0.0	0.0	2801.63	0.0	
			1194.83	0.0	16.32	283.27	0.00					
2005[厨房]	房间参数		面积(m2)	高度(m)	室内设计温度(℃)	室内设计相对湿度(%)	放大系数					
			11.47	3.0	16.00	60.00	1.00					
	北外墙	参数	长(m)	宽(高)(m)	外墙面积(m2)	外墙净面积(m2)	传热系数	温差修正系数				
			9.92	3.0	29.76	24.96	0.34	1.0				
		负荷统计	395.81	0.0	0.0	359.82	0.10	0.00	0.0	395.81	0.00	
			395.81	0.00	0.0	0.0	0.0					
	北外窗_嵌	参数	长(m)	宽(高)(m)	面积(m2)	传热系数	缝隙长度(m)	渗透系数	安装高度(m)	温差修正系数		
			1.50	2.000	3.00	1.4	8.5	0.3	0.90	1.0		
		负荷统计	299.26	0.0	0.0	178.08	0.10	0.00	0.0	195.89	0.00	
			299.26	0.00	6.52	103.38	0.0					
	北外窗_嵌	参数	长(m)	宽(高)(m)	面积(m2)	传热系数	缝隙长度(m)	渗透系数	安装高度(m)	温差修正系数		
			0.90	2.000	1.80	1.4	6.9	0.3	0.90	1.0		
		负荷统计	201.45	0.0	0.0	106.85	0.10	0.00	0.0	117.53	0.00	
			201.45	0.00	5.29	83.92	0.0					
	新风(热)	参数	新风量m3/h	新风机送风状态点	热回收方式							
			13.76	16.0℃/60.0%	没有热回收							
		负荷统计	329.96	0.0	0.0	0.0	0.0	0.0	0.0	329.96	0.0	
			0.0	0.0	0.0	0.0	0.0					
2005[厨房]房间小计			1226.48	0.00	106.93	644.75	0.0	0.0	0.0	1039.18	0.0	
			896.52	0.0	11.81	187.29	0.00					
2006[楼梯间]	房间参数		面积(m2)	高度(m)	室内设计温度(℃)	室内设计相对湿度(%)	放大系数					
			27.94	3.0	16.00	60.00	1.00					
	西外墙	参数	长(m)	宽(高)(m)	外墙面积(m2)	外墙净面积(m2)	传热系数	温差修正系数				
			2.24	3.0	6.72	6.72	0.34	1.0				
		负荷统计	96.88	0.0	0.0	96.88	-0.05	0.00	0.05	96.88	0.00	
			96.88	0.00	0.0	0.0	0.0					
	北外墙	参数	长(m)	宽(高)(m)	外墙面积(m2)	外墙净面积(m2)	传热系数	温差修正系数				
			4.32	3.0	12.96	10.71	0.34	1.0				
		负荷统计	177.55	0.0	0.0	154.40	0.10	0.00	0.05	177.55	0.00	
			177.55	0.00	0.0	0.0	0.0					
	北外窗_嵌	参数	长(m)	宽(高)(m)	面积(m2)	传热系数	缝隙长度(m)	渗透系数	安装高度(m)	温差修正系数		
			1.13	2.000	2.25	1.4	7.5	0.3	0.90	1.0		
		负荷统计	244.81	0.0	0.0	133.56	0.10	0.00	0.05	153.59	0.00	
			244.81	0.00	5.75	91.21	0.0					
	东外墙	参数	长(m)	宽(高)(m)	外墙面积(m2)	外墙净面积(m2)	传热系数	温差修正系数				
			2.24	3.0	6.72	6.72	0.34	1.0				
负荷		96.88	0.0	0.0	96.88	-0.05	0.00	0.05	96.88	0.00		

	新风 (热)	统计	96.88	0.00	0.0	0.0	0.0	城建工程 有限公司	乌设施审-2026	2026年08月	804.03	0.0		
		参数	新风量 m3/h	新风机送 风状态点	热回收方 式									
			33.53	16.0℃ /60.0%	没有热回 收									
		负荷 统计	804.03 0.0	0.0 0.0	0.0 0.0	0.0 0.0	0.0 0.0						0.0 0.0	
2006[楼梯间]房间小计			1420.14 616.11	0.00 0.0	50.83 5.75	481.71 91.21	0.0 0.00	0.0 0.0	0.0 0.0	1328.93	0.0			
2007[厨房]	房间参数		面积(m2)	高度(m)	室内设计 温度(℃)	室内设计 相对湿度 (%)	放大系数							
			11.47	3.0	16.00	60.00	1.00							
	北外墙	参数	长(m)	宽 (高)(m)	外墙面积 (m2)	外墙净面 积(m2)	传热系数	温差修正 系数						
			9.92	3.0	29.76	24.96	0.34	1.0						
		负荷 统计	395.81 395.81	0.0 0.00	0.0 0.0	359.82 0.0	0.10 0.0	0.00	0.0	395.81 0.00				
	北外窗_嵌	参数	长(m)	宽 (高)(m)	面积(m2)	传热系数	缝隙长度 (m)	渗透系数	安装高度 (m)	温差修正 系数				
			1.50	2.000	3.00	1.4	8.5	0.3	0.90	1.0				
		负荷 统计	299.26 299.26	0.0 0.00	0.0 6.52	178.08 103.38	0.10 0.0	0.00	0.0	195.89 0.00				
	北外窗_嵌	参数	长(m)	宽 (高)(m)	面积(m2)	传热系数	缝隙长度 (m)	渗透系数	安装高度 (m)	温差修正 系数				
			0.90	2.000	1.80	1.4	6.9	0.3	0.90	1.0				
		负荷 统计	201.45 201.45	0.0 0.00	0.0 5.29	106.85 83.92	0.10 0.0	0.00	0.0	117.53 0.00				
	新风 (热)	参数	新风量 m3/h	新风机送 风状态点	热回收方 式									
			13.76	16.0℃ /60.0%	没有热回 收									
		负荷 统计	329.96 0.0	0.0 0.0	0.0 0.0	0.0 0.0	0.0 0.0	0.0 0.0	0.0 0.0	329.96 0.0	0.0			
2007[厨房]房间小计			1226.48 896.52	0.00 0.0	106.93 11.81	644.75 187.29	0.0 0.00	0.0 0.0	0.0 0.0	1039.18	0.0			
2008[起居室]	房间参数		面积(m2)	高度(m)	室内设计 温度(℃)	室内设计 相对湿度 (%)	放大系数							
			57.18	3.0	20.00	60.00	1.00							
	南外墙	参数	长(m)	宽 (高)(m)	外墙面积 (m2)	外墙净面 积(m2)	传热系数	温差修正 系数						
			12.08	3.0	36.24	27.69	0.34	1.0						
		负荷 统计	371.31 371.31	0.0 0.00	0.0 0.0	436.84 0.0	-0.20 0.0	0.00	0.05	371.31 0.00				
	南外窗_嵌	参数	长(m)	宽 (高)(m)	面积(m2)	传热系数	缝隙长度 (m)	渗透系数	安装高度 (m)	温差修正 系数				
			1.57	2.000	3.15	1.4	8.7	0.3	0.90	1.0				
		负荷 统计	295.39 295.39	0.0 0.00	0.0 7.00	204.62 121.46	-0.20 0.0	0.00	0.05	173.93 0.00				
	南外窗_嵌	参数	长(m)	宽 (高)(m)	面积(m2)	传热系数	缝隙长度 (m)	渗透系数	安装高度 (m)	温差修正 系数				
			2.70	2.000	5.40	1.4	11.4	0.3	0.60	1.0				
		负荷 统计	459.97 459.97	0.0 0.00	0.0 9.32	350.78 161.81	-0.20 0.0	0.00	0.05	298.17 0.00				
	西外墙	参数	长(m)	宽 (高)(m)	外墙面积 (m2)	外墙净面 积(m2)	传热系数	温差修正 系数						
			1.44	3.0	4.32	4.32	0.34	1.0						
		负荷 统计	68.15 68.15	0.0 0.00	0.0 0.0	68.15 0.0	-0.05 0.0	0.00	0.05	68.15 0.00				
新风 (热)	参数	新风量 m3/h	新风机送 风状态点	热回收方 式										
		68.62	20.0℃ /60.0%	没有热回 收										
	负荷	1890.07	0.0	0.0	0.0	0.0	0.0	0.0	1890.07	0.0				

		统计		0.0	0.0	0.0	0.0	0.0	城建工程有限公司		2026年08月	
2008[起居室]房间小计				3084.90	0.00	53.95	1060.40	0.0	0.0	0.0	0.0	0.0
				1194.83	0.0	16.32	283.27	0.00				
2009[卧室]	房间参数			面积(m2)	高度(m)	室内设计温度(℃)	室内设计相对湿度(%)	放大系数				
				10.15	3.0	20.00	60.00	1.00				
	东外墙	参数	长(m)	宽(高)(m)	外墙面积(m2)	外墙净面积(m2)	传热系数	温差修正系数				
			5.36	3.0	16.08	16.08	0.34	1.0				
		负荷统计	253.68	0.0	0.0	253.68	-0.05	0.00	0.05	253.68	0.00	
	253.68		0.00	0.0	0.0	0.0						
	北外墙	参数	长(m)	宽(高)(m)	外墙面积(m2)	外墙净面积(m2)	传热系数	温差修正系数				
			4.32	3.0	12.96	10.26	0.34	1.0				
		负荷统计	186.14	0.0	0.0	161.86	0.10	0.00	0.05	186.14	0.00	
	186.14		0.00	0.0	0.0	0.0						
	北外窗_嵌	参数	长(m)	宽(高)(m)	面积(m2)	传热系数	缝隙长度(m)	渗透系数	安装高度(m)	温差修正系数		
			1.35	2.000	2.70	1.4	8.1	0.3	0.90	1.0		
		负荷统计	309.51	0.0	0.0	175.39	0.10	0.00	0.05	201.70	0.00	
	309.51		0.00	6.21	107.81	0.0						
	新风(热)	参数	新风量m3/h	新风机送风状态点	热回收方式							
			12.18	20.0℃/60.0%	没有热回收							
		负荷统计	335.49	0.0	0.0	0.0	0.0	0.0	0.0	335.49	0.0	
	0.0		0.0	0.0	0.0	0.0						
2009[卧室]房间小计				1084.81	0.00	106.88	590.93	0.0	0.0	0.0	977.01	0.0
				749.33	0.0	6.21	107.81	0.00				
2010[卧室]	房间参数			面积(m2)	高度(m)	室内设计温度(℃)	室内设计相对湿度(%)	放大系数				
				17.20	3.0	20.00	60.00	1.00				
	南外墙	参数	长(m)	宽(高)(m)	外墙面积(m2)	外墙净面积(m2)	传热系数	温差修正系数				
			5.60	3.0	16.80	13.65	0.34	1.0				
		负荷统计	172.27	0.0	0.0	215.34	-0.20	0.00	0.0	172.27	0.00	
	172.27		0.00	0.0	0.0	0.0						
	南外窗_嵌	参数	长(m)	宽(高)(m)	面积(m2)	传热系数	缝隙长度(m)	渗透系数	安装高度(m)	温差修正系数		
			1.57	2.000	3.15	1.4	8.7	0.3	0.90	1.0		
		负荷统计	285.16	0.0	0.0	204.62	-0.20	0.00	0.0	163.70	0.00	
	285.16		0.00	7.00	121.46	0.0						
	新风(热)	参数	新风量m3/h	新风机送风状态点	热回收方式							
			20.64	20.0℃/60.0%	没有热回收							
负荷统计		568.51	0.0	0.0	0.0	0.0	0.0	0.0	568.51	0.0		
	0.0	0.0	0.0	0.0	0.0							
2010[卧室]房间小计				1025.94	0.00	59.65	419.97	0.0	0.0	0.0	904.48	0.0
				457.44	0.0	7.00	121.46	0.00				
2011[卫生间]	房间参数			面积(m2)	高度(m)	室内设计温度(℃)	室内设计相对湿度(%)	放大系数				
				7.92	3.0	20.00	60.00	1.00				
	北外墙	参数	长(m)	宽(高)(m)	外墙面积(m2)	外墙净面积(m2)	传热系数	温差修正系数				
			1.28	3.0	3.84	3.16	0.34	1.0				
		负荷统计	54.84	0.0	0.0	49.85	0.10	0.00	0.0	54.84	0.00	
	54.84		0.00	0.0	0.0	0.0						
	北外窗_嵌	参数	长(m)	宽(高)(m)	面积(m2)	传热系数	缝隙长度(m)	渗透系数	安装高度(m)	温差修正系数		
			0.34	2.000	0.68	1.4	5.4	0.3	0.90	1.0		
负荷		120.46	0.0	0.0	44.17	0.10	0.00	0.0	48.59	0.00		

1
号
楼
2-
9
层
*8

	新风 (热)	统计	120.46	0.00	4.14	71.87	0.0	城建工程 有限公司	乌设施审 2026年08月				
		参数	新风量 m3/h	新风机送 风状态点	热回收方 式								
			9.50	20.0℃ /60.0%	没有热回 收								
		负荷 统计	261.67 0.0	0.0 0.0	0.0 0.0	0.0 0.0	0.0 0.0					0.0 0.0	0.0 0.0
2011[卫生间]房间小计			436.97 175.30	0.00 0.0	55.17 4.14	94.02 71.87	0.0 0.00	0.0 	0.0 	365.10 	0.0 		
2012[卫生间]	房间参数		面积(m2)	高度(m)	室内设计 温度(℃)	室内设计 相对湿度 (%)	放大系数						
			7.92	3.0	20.00	60.00	1.00						
	北外墙	参数	长(m)	宽 (高)(m)	外墙面积 (m2)	外墙净面 积(m2)	传热系数	温差修正 系数					
			1.28	3.0	3.84	3.16	0.34	1.0					
		负荷 统计	54.84 54.84	0.0 0.00	0.0 0.0	49.85 0.0	0.10 0.0	0.00 	0.0 	54.84 	0.00 		
	北外窗_嵌	参数	长(m)	宽 (高)(m)	面积(m2)	传热系数	缝隙长度 (m)	渗透系数	安装高度 (m)	温差修正 系数			
			0.34	2.000	0.68	1.4	5.4	0.3	0.90	1.0			
		负荷 统计	120.46 120.46	0.0 0.00	0.0 4.14	44.17 71.87	0.10 0.0	0.00 	0.0 	48.59 	0.00 		
	新风 (热)	参数	新风量 m3/h	新风机送 风状态点	热回收方 式								
			9.50	20.0℃ /60.0%	没有热回 收								
		负荷 统计	261.67 0.0	0.0 0.0	0.0 0.0	0.0 0.0	0.0 0.0	0.0 	0.0 	261.67 	0.0 		
	2012[卫生间]房间小计			436.97 175.30	0.00 0.0	55.17 4.14	94.02 71.87	0.0 0.00	0.0 	0.0 	365.10 	0.0 	
	2013[卧室]	房间参数		面积(m2)	高度(m)	室内设计 温度(℃)	室内设计 相对湿度 (%)	放大系数					
				17.20	3.0	20.00	60.00	1.00					
南外墙		参数	长(m)	宽 (高)(m)	外墙面积 (m2)	外墙净面 积(m2)	传热系数	温差修正 系数					
			5.60	3.0	16.80	13.65	0.34	1.0					
		负荷 统计	172.27 172.27	0.0 0.00	0.0 0.0	215.34 0.0	-0.20 0.0	0.00 	0.0 	172.27 	0.00 		
南外窗_嵌		参数	长(m)	宽 (高)(m)	面积(m2)	传热系数	缝隙长度 (m)	渗透系数	安装高度 (m)	温差修正 系数			
			1.57	2.000	3.15	1.4	8.7	0.3	0.90	1.0			
		负荷 统计	285.16 285.16	0.0 0.00	0.0 7.00	204.62 121.46	-0.20 0.0	0.00 	0.0 	163.70 	0.00 		
新风 (热)		参数	新风量 m3/h	新风机送 风状态点	热回收方 式								
			20.64	20.0℃ /60.0%	没有热回 收								
		负荷 统计	568.51 0.0	0.0 0.0	0.0 0.0	0.0 0.0	0.0 0.0	0.0 	0.0 	568.51 	0.0 		
2013[卧室]房间小计			1025.94 457.44	0.00 0.0	59.65 7.00	419.97 121.46	0.0 0.00	0.0 	0.0 	904.48 	0.0 		
2014[卧室]		房间参数		面积(m2)	高度(m)	室内设计 温度(℃)	室内设计 相对湿度 (%)	放大系数					
				10.15	3.0	20.00	60.00	1.00					
	西外墙	参数	长(m)	宽 (高)(m)	外墙面积 (m2)	外墙净面 积(m2)	传热系数	温差修正 系数					
			5.36	3.0	16.08	16.08	0.34	1.0					
		负荷 统计	253.68 253.68	0.0 0.00	0.0 0.0	253.68 0.0	-0.05 0.0	0.00 	0.05 	253.68 	0.00 		
	北外墙	参数	长(m)	宽 (高)(m)	外墙面积 (m2)	外墙净面 积(m2)	传热系数	温差修正 系数					
			4.32	3.0	12.96	10.26	0.34	1.0					

号楼	2014[卧室]			负荷统计	186.14	0.0	0.0	161.86	0.10	0.00	城有建有限公司 工程司	186.14	0.00					
					186.14	0.00	0.0	0.0	0.0	0.0				186.14	0.00			
		北外窗_嵌	参数	长(m)	宽(高)(m)	面积(m2)	传热系数	缝隙长度(m)	渗透系数	安装高度(m)						温差修正系数	26年08月	
				1.35	2.000	2.70	1.4	8.1	0.3	0.90						1.0		
			负荷统计	309.51	0.0	0.0	175.39	0.10	0.00	0.05						201.70		0.00
				309.51	0.00	6.21	107.81	0.0										
		新风(热)	参数	新风量m3/h	新风机送风状态点	热回收方式												
				12.18	20.0℃/60.0%	没有热回收												
			负荷统计	335.49	0.0	0.0	0.0	0.0	0.0	0.0						335.49	0.0	
				0.0	0.0	0.0	0.0	0.0										
	2014[卧室]房间小计				1084.81	0.00	106.88	590.93	0.0	0.0	0.0	977.01	0.0					
					749.33	0.0	6.21	107.81	0.00									
	2015[起居室]	房间参数		面积(m2)	高度(m)	室内设计温度(℃)	室内设计相对湿度(%)	放大系数										
				57.18	3.0	20.00	60.00	1.00										
		南外墙	参数	长(m)	宽(高)(m)	外墙面积(m2)	外墙净面积(m2)	传热系数	温差修正系数									
				12.08	3.0	36.24	27.69	0.34	1.0									
			负荷统计	371.31	0.0	0.0	436.84	-0.20	0.00	0.05	371.31	0.00						
				371.31	0.00	0.0	0.0	0.0										
		南外窗_嵌	参数	长(m)	宽(高)(m)	面积(m2)	传热系数	缝隙长度(m)	渗透系数	安装高度(m)	温差修正系数							
				1.57	2.000	3.15	1.4	8.7	0.3	0.90	1.0							
			负荷统计	295.39	0.0	0.0	204.62	-0.20	0.00	0.05	173.93	0.00						
				295.39	0.00	7.00	121.46	0.0										
		南外窗_嵌	参数	长(m)	宽(高)(m)	面积(m2)	传热系数	缝隙长度(m)	渗透系数	安装高度(m)	温差修正系数							
				2.70	2.000	5.40	1.4	11.4	0.3	0.60	1.0							
			负荷统计	459.97	0.0	0.0	350.78	-0.20	0.00	0.05	298.17	0.00						
				459.97	0.00	9.32	161.81	0.0										
		东外墙	参数	长(m)	宽(高)(m)	外墙面积(m2)	外墙净面积(m2)	传热系数	温差修正系数									
				1.44	3.0	4.32	4.32	0.34	1.0									
			负荷统计	68.15	0.0	0.0	68.15	-0.05	0.00	0.05	68.15	0.00						
				68.15	0.00	0.0	0.0	0.0										
		新风(热)	参数	新风量m3/h	新风机送风状态点	热回收方式												
				68.62	20.0℃/60.0%	没有热回收												
			负荷统计	1890.07	0.0	0.0	0.0	0.0	0.0	0.0	1890.07	0.0						
				0.0	0.0	0.0	0.0	0.0										
	2015[起居室]房间小计				3084.90	0.00	53.95	1060.40	0.0	0.0	0.0	2801.63	0.0					
					1194.83	0.0	16.32	283.27	0.00									
	2016[厨房]	房间参数		面积(m2)	高度(m)	室内设计温度(℃)	室内设计相对湿度(%)	放大系数										
				11.47	3.0	16.00	60.00	1.00										
		北外墙	参数	长(m)	宽(高)(m)	外墙面积(m2)	外墙净面积(m2)	传热系数	温差修正系数									
				9.92	3.0	29.76	24.96	0.34	1.0									
			负荷统计	395.81	0.0	0.0	359.82	0.10	0.00	0.0	395.81	0.00						
				395.81	0.00	0.0	0.0	0.0										
		北外窗_嵌	参数	长(m)	宽(高)(m)	面积(m2)	传热系数	缝隙长度(m)	渗透系数	安装高度(m)	温差修正系数							
				1.50	2.000	3.00	1.4	8.5	0.3	0.90	1.0							
			负荷统计	299.26	0.0	0.0	178.08	0.10	0.00	0.0	195.89	0.00						
				299.26	0.00	6.52	103.38	0.0										
		北外窗_嵌	参数	长(m)	宽(高)(m)	面积(m2)	传热系数	缝隙长度(m)	渗透系数	安装高度(m)	温差修正系数							
				0.90	2.000	1.80	1.4	6.9	0.3	0.90	1.0							
	负荷		201.45	0.0	0.0	106.85	0.10	0.00	0.0	117.53	0.00							

	新风 (热)	统计	201.45	0.00	5.29	83.92	0.0	城建工程 有限公司	乌设施审-2026	2026年08月			
		参数	新风量 m3/h	新风机送 风状态点	热回收方 式								
			13.76	16.0℃ /60.0%	没有热回 收								
		负荷 统计	329.96	0.0	0.0	0.0	0.0					0.0	0.0
2016[厨房]房间小计			1226.48	0.00	106.93	644.75	0.0	0.0	0.0	1039.18	0.0		
			896.52	0.0	11.81	187.29	0.00						
2017[楼 梯 间]	房间参数		面积(m2)	高度(m)	室内设计 温度(℃)	室内设计 相对湿度 (%)	放大系数						
			27.94	3.0	16.00	60.00	1.00						
	东外墙	参数	长(m)	宽 (高)(m)	外墙面积 (m2)	外墙净面 积(m2)	传热系数	温差修正 系数					
			2.24	3.0	6.72	6.72	0.34	1.0					
		负荷 统计	96.88	0.0	0.0	96.88	-0.05	0.00	0.05	96.88	0.00		
			96.88	0.00	0.0	0.0	0.0						
	北外墙	参数	长(m)	宽 (高)(m)	外墙面积 (m2)	外墙净面 积(m2)	传热系数	温差修正 系数					
			4.32	3.0	12.96	10.71	0.34	1.0					
		负荷 统计	177.55	0.0	0.0	154.40	0.10	0.00	0.05	177.55	0.00		
			177.55	0.00	0.0	0.0	0.0						
	北外窗_嵌	参数	长(m)	宽 (高)(m)	面积(m2)	传热系数	缝隙长度 (m)	渗透系数	安装高度 (m)	温差修正 系数			
			1.13	2.000	2.25	1.4	7.5	0.3	0.90	1.0			
		负荷 统计	244.81	0.0	0.0	133.56	0.10	0.00	0.05	153.59	0.00		
			244.81	0.00	5.75	91.21	0.0						
	西外墙	参数	长(m)	宽 (高)(m)	外墙面积 (m2)	外墙净面 积(m2)	传热系数	温差修正 系数					
			2.24	3.0	6.72	6.72	0.34	1.0					
		负荷 统计	96.88	0.0	0.0	96.88	-0.05	0.00	0.05	96.88	0.00		
96.88			0.00	0.0	0.0	0.0							
新风 (热)	参数	新风量 m3/h	新风机送 风状态点	热回收方 式									
		33.53	16.0℃ /60.0%	没有热回 收									
	负荷 统计	804.03	0.0	0.0	0.0	0.0	0.0	0.0	804.03	0.0			
		0.0	0.0	0.0	0.0	0.0							
2017[楼梯间]房间小计			1420.14	0.00	50.83	481.71	0.0	0.0	0.0	1328.93	0.0		
			616.11	0.0	5.75	91.21	0.00						
2018[厨 房]	房间参数		面积(m2)	高度(m)	室内设计 温度(℃)	室内设计 相对湿度 (%)	放大系数						
			11.47	3.0	16.00	60.00	1.00						
	北外墙	参数	长(m)	宽 (高)(m)	外墙面积 (m2)	外墙净面 积(m2)	传热系数	温差修正 系数					
			9.92	3.0	29.76	24.96	0.34	1.0					
		负荷 统计	395.81	0.0	0.0	359.82	0.10	0.00	0.0	395.81	0.00		
			395.81	0.00	0.0	0.0	0.0						
	北外窗_嵌	参数	长(m)	宽 (高)(m)	面积(m2)	传热系数	缝隙长度 (m)	渗透系数	安装高度 (m)	温差修正 系数			
			1.50	2.000	3.00	1.4	8.5	0.3	0.90	1.0			
		负荷 统计	299.26	0.0	0.0	178.08	0.10	0.00	0.0	195.89	0.00		
			299.26	0.00	6.52	103.38	0.0						
	北外窗_嵌	参数	长(m)	宽 (高)(m)	面积(m2)	传热系数	缝隙长度 (m)	渗透系数	安装高度 (m)	温差修正 系数			
			0.90	2.000	1.80	1.4	6.9	0.3	0.90	1.0			
		负荷 统计	201.45	0.0	0.0	106.85	0.10	0.00	0.0	117.53	0.00		
			201.45	0.00	5.29	83.92	0.0						
新风 (热)	参数	新风量 m3/h	新风机送 风状态点	热回收方 式									
		13.76	16.0℃ /60.0%	没有热回 收									
	负荷	329.96	0.0	0.0	0.0	0.0	0.0	0.0	329.96	0.0			

			统计	0.0	0.0	0.0	0.0	0.0	城建工程有限公司		乌市设施审		2024
2018[厨房]房间小计			1226.48	0.00	106.93	644.75	0.0	0.0	0.0	0.0	0.0	0.0	0.0
			896.52	0.0	11.81	187.29	0.00						
2019[起居 室]	房间参数		面积(m2)	高度(m)	室内设计 温度(℃)	室内设计 相对湿度 (%)	放大系数						
			57.18	3.0	20.00	60.00	1.00						
	南外墙	参数	长(m)	宽 (高)(m)	外墙面积 (m2)	外墙净面 积(m2)	传热系数	温差修正 系数					
			12.08	3.0	36.24	27.69	0.34	1.0					
		负荷统计	371.31	0.0	0.0	436.84	-0.20	0.00	0.05	371.31	0.00		
		371.31	0.00	0.0	0.0	0.0							
	南外窗_嵌	参数	长(m)	宽 (高)(m)	面积(m2)	传热系数	缝隙长度 (m)	渗透系数	安装高度 (m)	温差修正 系数			
			2.70	2.000	5.40	1.4	11.4	0.3	0.60	1.0			
		负荷统计	459.97	0.0	0.0	350.78	-0.20	0.00	0.05	298.17	0.00		
		459.97	0.00	9.32	161.81	0.0							
	南外窗_嵌	参数	长(m)	宽 (高)(m)	面积(m2)	传热系数	缝隙长度 (m)	渗透系数	安装高度 (m)	温差修正 系数			
			1.57	2.000	3.15	1.4	8.7	0.3	0.90	1.0			
		负荷统计	295.39	0.0	0.0	204.62	-0.20	0.00	0.05	173.93	0.00		
		295.39	0.00	7.00	121.46	0.0							
	西外墙	参数	长(m)	宽 (高)(m)	外墙面积 (m2)	外墙净面 积(m2)	传热系数	温差修正 系数					
			1.44	3.0	4.32	4.32	0.34	1.0					
		负荷统计	68.15	0.0	0.0	68.15	-0.05	0.00	0.05	68.15	0.00		
		68.15	0.00	0.0	0.0	0.0							
	新风 (热)	参数	新风量 m3/h	新风机送 风状态点	热回收方 式								
			68.62	20.0℃ /60.0%	没有热回 收								
		负荷统计	1890.07	0.0	0.0	0.0	0.0	0.0	0.0	1890.07	0.0		
		0.0	0.0	0.0	0.0	0.0							
2019[起居]房间小计			3084.90	0.00	53.95	1060.40	0.0	0.0	0.0	2801.63	0.0		
			1194.83	0.0	16.32	283.27	0.00						
2020[卧室]	房间参数		面积(m2)	高度(m)	室内设计 温度(℃)	室内设计 相对湿度 (%)	放大系数						
			12.83	3.0	20.00	60.00	1.00						
	东外墙	参数	长(m)	宽 (高)(m)	外墙面积 (m2)	外墙净面 积(m2)	传热系数	温差修正 系数					
			5.36	3.0	16.08	16.08	0.34	1.0					
		负荷统计	253.68	0.0	0.0	253.68	-0.05	0.00	0.05	253.68	0.00		
		253.68	0.00	0.0	0.0	0.0							
	北外墙	参数	长(m)	宽 (高)(m)	外墙面积 (m2)	外墙净面 积(m2)	传热系数	温差修正 系数					
			5.60	3.0	16.80	13.65	0.34	1.0					
		负荷统计	247.64	0.0	0.0	215.34	0.10	0.00	0.05	247.64	0.00		
		247.64	0.00	0.0	0.0	0.0							
	北外窗_嵌	参数	长(m)	宽 (高)(m)	面积(m2)	传热系数	缝隙长度 (m)	渗透系数	安装高度 (m)	温差修正 系数			
			1.57	2.000	3.15	1.4	8.7	0.3	0.90	1.0			
		负荷统计	351.11	0.0	0.0	204.62	0.10	0.00	0.05	235.32	0.00		
		351.11	0.00	6.67	115.79	0.0							
	新风 (热)	参数	新风量 m3/h	新风机送 风状态点	热回收方 式								
			15.40	20.0℃ /60.0%	没有热回 收								
		负荷统计	424.18	0.0	0.0	0.0	0.0	0.0	0.0	424.18	0.0		
		0.0	0.0	0.0	0.0	0.0							
2020[卧室]房间小计			1276.61	0.00	99.50	673.64	0.0	0.0	0.0	1160.82	0.0		
			852.43	0.0	6.67	115.79	0.00						
	房间参数		面积(m2)	高度(m)	室内设计 温度(℃)	室内设计 相对湿度 (%)	放大系数						

2021[卧室]	南外墙	参数	17.20	3.0	20.00	60.00	1.00	温差修正系数	1.0	183.04	0.00	
			长(m)	宽(高)(m)	外墙面积(m2)	外墙净面积(m2)	传热系数					
		负荷统计	5.60	3.0	16.80	13.65	0.34	0.00	0.05	173.93	0.00	
			183.04	0.0	0.0	215.34	-0.20	0.00	0.05	336.98	0.00	
	南外墙窗嵌	参数	183.04	0.00	0.0	0.0	0.0	缝隙长度(m)	渗透系数	安装高度(m)	温差修正系数	
			长(m)	宽(高)(m)	面积(m2)	传热系数						
		负荷统计	1.57	2.000	3.15	1.4	8.7	0.3	0.90	1.0		
			295.39	0.0	0.0	204.62	-0.20	0.00	0.05	173.93	0.00	
	东外墙	参数	295.39	0.00	7.00	121.46	0.0	缝隙长度(m)	渗透系数	安装高度(m)	温差修正系数	
			长(m)	宽(高)(m)	外墙面积(m2)	外墙净面积(m2)	传热系数					
		负荷统计	7.12	3.0	21.36	21.36	0.34	1.0				
			336.98	0.0	0.0	336.98	-0.05	0.00	0.05	336.98	0.00	
	新风(热)	参数	336.98	0.00	0.0	0.0	0.0	缝隙长度(m)	渗透系数	安装高度(m)	温差修正系数	
			新风量m3/h	新风机送风状态点	热回收方式							
		负荷统计	20.64	20.0℃/60.0%	没有热回收							
			568.51	0.0	0.0	0.0	0.0	0.0	0.0	0.0	568.51	0.0
2021[卧室]房间小计			0.0	0.0	80.46	756.94	0.0	0.0	0.0	1262.45	0.0	
2022[卫生间]	房间参数		1383.92	0.00	80.46	756.94	0.0	0.0	0.0	1262.45	0.0	
			815.41	0.0	7.00	121.46	0.00					
	东外墙	参数	面积(m2)	高度(m)	室内设计温度(℃)	室内设计相对湿度(%)	放大系数					
			7.92	3.0	20.00	60.00	1.00					
		负荷统计	长(m)	宽(高)(m)	外墙面积(m2)	外墙净面积(m2)	传热系数	温差修正系数				
			5.76	3.0	17.28	15.48	0.34	1.0				
	东外墙窗嵌	参数	232.00	0.0	0.0	244.21	-0.05	0.00	0.0	232.00	0.00	
			232.00	0.00	0.0	0.0	0.0					
		负荷统计	长(m)	宽(高)(m)	面积(m2)	传热系数	缝隙长度(m)	渗透系数	安装高度(m)	温差修正系数		
			0.45	2.000	0.90	1.4	5.7	0.3	0.90	1.0		
	东外墙窗嵌	参数	132.36	0.0	0.0	58.46	-0.05	0.00	0.0	55.54	0.00	
			132.36	0.00	4.43	76.82	0.0					
		负荷统计	长(m)	宽(高)(m)	面积(m2)	传热系数	缝隙长度(m)	渗透系数	安装高度(m)	温差修正系数		
			0.45	2.000	0.90	1.4	5.7	0.3	0.90	1.0		
	新风(热)	参数	132.36	0.0	0.0	58.46	-0.05	0.00	0.0	55.54	0.00	
			132.36	0.00	4.43	76.82	0.0					
负荷统计		新风量m3/h	新风机送风状态点	热回收方式								
		9.50	20.0℃/60.0%	没有热回收								
2022[卫生间]房间小计			0.0	0.0	95.76	361.14	0.0	0.0	0.0	604.75	0.0	
2-9层小计			496.71	0.0	8.85	153.63	0.00					
			32016.35	0.00	67.13	13577.31	0.0	0.0	0.0	28570.31	0.0	
			16688.17	0.0	203.60	3446.04	0.00					
	房间参数		面积(m2)	高度(m)	室内设计温度(℃)	室内设计相对湿度(%)	放大系数					
			7.92	3.0	20.00	60.00	1.00					
	西外墙	参数	长(m)	宽(高)(m)	外墙面积(m2)	外墙净面积(m2)	传热系数	温差修正系数				
			5.76	3.0	17.28	15.48	0.34	1.0				
		负荷统计	232.00	0.0	0.0	244.21	-0.05	0.00	0.0	232.00	0.00	
			232.00	0.00	0.0	0.0	0.0					
西外墙窗嵌	参数	长(m)	宽(高)(m)	面积(m2)	传热系数	缝隙长度(m)	渗透系数	安装高度(m)	温差修正系数			
		0.45	2.000	0.90	1.4	5.7	0.3	0.90	1.0			

10001[卫生间]	换气	负荷统计	55.54	0.0	0.0	58.46	-0.05	0.00	0.0	55.54	0.00
			55.54	0.00	0.00	0.00	0.0				
	西外墙_嵌	参数	长(m)	宽(高)(m)	面积(m2)	传热系数	缝隙长度(m)	渗透系数	安装高度(m)	温差修正系数	
			0.45	2.000	0.90	1.4	5.7	0.3	0.90	1.0	
		负荷统计	55.54	0.0	0.0	58.46	-0.05	0.00	0.0	55.54	0.00
			55.54	0.00	0.00	0.00	0.0				
	屋面	参数	长(m)	宽度(m)	面积(m2)	传热系数	温差修正系数				
			2.20	3.600	7.92	0.13	1.0				
		负荷统计	47.77	0.0	0.0	47.77	0.00	0.00	0.0	47.77	0.00
			47.77	0.00	0.0	0.0	0.0				
	新风(热)	参数	新风量m3/h	新风机送风状态点	热回收方式						
			9.50	20.0℃/60.0%	没有热回收						
		负荷统计	261.67	0.0	0.0	0.0	0.0	0.0	0.0	261.67	0.0
			0.0	0.0	0.0	0.0	0.0				
	10001[卫生间]房间小计		652.52	0.00	82.39	408.91	0.0	0.0	0.0	652.52	0.0
			390.86	0.0	0.00	0.00	0.00				
10002[卧室]	房间参数		面积(m2)	高度(m)	室内设计温度(℃)	室内设计相对湿度(%)	放大系数				
			12.83	3.0	20.00	60.00	1.00				
	西外墙	参数	长(m)	宽(高)(m)	外墙面积(m2)	外墙净面积(m2)	传热系数	温差修正系数			
			5.36	3.0	16.08	16.08	0.34	1.0			
		负荷统计	253.68	0.0	0.0	253.68	-0.05	0.00	0.05	253.68	0.00
			253.68	0.00	0.0	0.0	0.0				
	北外墙	参数	长(m)	宽(高)(m)	外墙面积(m2)	外墙净面积(m2)	传热系数	温差修正系数			
			5.60	3.0	16.80	13.65	0.34	1.0			
		负荷统计	247.64	0.0	0.0	215.34	0.10	0.00	0.05	247.64	0.00
			247.64	0.00	0.0	0.0	0.0				
	北外墙_嵌	参数	长(m)	宽(高)(m)	面积(m2)	传热系数	缝隙长度(m)	渗透系数	安装高度(m)	温差修正系数	
			1.57	2.000	3.15	1.4	8.7	0.3	0.90	1.0	
		负荷统计	235.32	0.0	0.0	204.62	0.10	0.00	0.05	235.32	0.00
			235.32	0.00	0.00	0.00	0.0				
	屋面	参数	长(m)	宽度(m)	面积(m2)	传热系数	温差修正系数				
			3.50	3.666	12.83	0.13	1.0				
		负荷统计	77.39	0.0	0.0	77.39	0.00	0.00	0.0	77.39	0.00
			77.39	0.00	0.0	0.0	0.0				
	新风(热)	参数	新风量m3/h	新风机送风状态点	热回收方式						
			15.40	20.0℃/60.0%	没有热回收						
		负荷统计	424.18	0.0	0.0	0.0	0.0	0.0	0.0	424.18	0.0
			0.0	0.0	0.0	0.0	0.0				
	10002[卧室]房间小计		1238.21	0.00	96.51	751.04	0.0	0.0	0.0	1238.21	0.0
			814.03	0.0	0.00	0.00	0.00				
	房间参数		面积(m2)	高度(m)	室内设计温度(℃)	室内设计相对湿度(%)	放大系数				
			17.20	3.0	20.00	60.00	1.00				
	南外墙	参数	长(m)	宽(高)(m)	外墙面积(m2)	外墙净面积(m2)	传热系数	温差修正系数			
			5.60	3.0	16.80	13.65	0.34	1.0			
		负荷统计	183.04	0.0	0.0	215.34	-0.20	0.00	0.05	183.04	0.00
			183.04	0.00	0.0	0.0	0.0				
	南外墙_嵌	参数	长(m)	宽(高)(m)	面积(m2)	传热系数	缝隙长度(m)	渗透系数	安装高度(m)	温差修正系数	
		负荷	173.93	0.0	0.0	204.62	-0.20	0.00	0.05	173.93	0.00

10003[卧室]	统计		173.93	0.00	0.00	0.00	0.0				
	西外墙	参数	长(m)	宽(高)(m)	外墙面积(m2)	外墙净面积(m2)	传热系数	温差修正系数			
			7.12	3.0	21.36	21.36	0.34	1.0			
		负荷统计	336.98	0.0	0.0	336.98	-0.05	0.00			
			336.98	0.00	0.0	0.0	0.0				
	屋面	参数	长(m)	宽度(m)	面积(m2)	传热系数	温差修正系数				
			3.50	4.914	17.20	0.13	1.0				
		负荷统计	103.75	0.0	0.0	103.75	0.00	0.00	0.0	103.75	0.00
			103.75	0.00	0.0	0.0	0.0				
	新风(热)	参数	新风量m3/h	新风机送风状态点	热回收方式						
			20.64	20.0℃/60.0%	没有热回收						
		负荷统计	568.51	0.0	0.0	0.0	0.0	0.0	0.0	568.51	0.0
			0.0	0.0	0.0	0.0	0.0				
10003[卧室]房间小计			1366.21	0.00	79.43	860.69	0.0	0.0	0.0	1366.21	0.0
			797.70	0.0	0.00	0.00	0.00				
10004[起居室]	房间参数		面积(m2)	高度(m)	室内设计温度(℃)	室内设计相对湿度(%)	放大系数				
			57.18	3.0	20.00	60.00	1.00				
	南外墙	参数	长(m)	宽(高)(m)	外墙面积(m2)	外墙净面积(m2)	传热系数	温差修正系数			
			12.08	3.0	36.24	27.69	0.34	1.0			
		负荷统计	371.31	0.0	0.0	436.84	-0.20	0.00	0.05	371.31	0.00
			371.31	0.00	0.0	0.0	0.0				
	南外墙_嵌	参数	长(m)	宽(高)(m)	面积(m2)	传热系数	缝隙长度(m)	渗透系数	安装高度(m)	温差修正系数	
			2.70	2.000	5.40	1.4	11.4	0.3	0.60	1.0	
		负荷统计	298.17	0.0	0.0	350.78	-0.20	0.00	0.05	298.17	0.00
			298.17	0.00	0.00	0.00	0.0				
	南外墙_嵌	参数	长(m)	宽(高)(m)	面积(m2)	传热系数	缝隙长度(m)	渗透系数	安装高度(m)	温差修正系数	
			1.57	2.000	3.15	1.4	8.7	0.3	0.90	1.0	
		负荷统计	173.93	0.0	0.0	204.62	-0.20	0.00	0.05	173.93	0.00
			173.93	0.00	0.00	0.00	0.0				
	东外墙	参数	长(m)	宽(高)(m)	外墙面积(m2)	外墙净面积(m2)	传热系数	温差修正系数			
			1.44	3.0	4.32	4.32	0.34	1.0			
		负荷统计	68.15	0.0	0.0	68.15	-0.05	0.00	0.05	68.15	0.00
			68.15	0.00	0.0	0.0	0.0				
	屋面	参数	长(m)	宽度(m)	面积(m2)	传热系数	温差修正系数				
			8.85	6.461	57.18	0.13	1.0				
		负荷统计	344.91	0.0	0.0	344.91	0.00	0.00	0.0	344.91	0.00
			344.91	0.00	0.0	0.0	0.0				
	新风(热)	参数	新风量m3/h	新风机送风状态点	热回收方式						
			68.62	20.0℃/60.0%	没有热回收						
		负荷统计	1890.07	0.0	0.0	0.0	0.0	0.0	0.0	1890.07	0.0
			0.0	0.0	0.0	0.0	0.0				
10004[起居室]房间小计			3146.54	0.00	55.03	1405.31	0.0	0.0	0.0	3146.54	0.0
			1256.47	0.0	0.00	0.00	0.00				
	房间参数		面积(m2)	高度(m)	室内设计温度(℃)	室内设计相对湿度(%)	放大系数				
			11.47	3.0	16.00	60.00	1.00				
	北外墙	参数	长(m)	宽(高)(m)	外墙面积(m2)	外墙净面积(m2)	传热系数	温差修正系数			
			9.92	3.0	29.76	24.96	0.34	1.0			
		负荷统计	395.81	0.0	0.0	359.82	0.10	0.00	0.0	395.81	0.00
			395.81	0.00	0.0	0.0	0.0				

10005[厨房]	北外窗_嵌	参数	长(m)	宽(高)(m)	面积(m2)	传热系数	缝隙长度(m)	渗透系数	安装高度(m)	温差修正系数	
			1.50	2.000	3.00	1.4	8.5	0.3	0.90	1.0	
		负荷统计	195.89	0.0	0.0	178.08	0.10	0.00	0.0	192.89	0.00
			195.89	0.00	0.00	0.00	0.0				
	北外窗_嵌	参数	长(m)	宽(高)(m)	面积(m2)	传热系数	缝隙长度(m)	渗透系数	安装高度(m)	温差修正系数	
			0.90	2.000	1.80	1.4	6.9	0.3	0.90	1.0	
		负荷统计	117.53	0.0	0.0	106.85	0.10	0.00	0.0	117.53	0.00
			117.53	0.00	0.00	0.00	0.0				
	屋面	参数	长(m)	宽度(m)	面积(m2)	传热系数	温差修正系数				
			6.20	1.850	11.47	0.13	1.0				
		负荷统计	63.22	0.0	0.0	63.22	0.00	0.00	0.0	63.22	0.00
			63.22	0.00	0.0	0.0	0.0				
新风(热)	参数	新风量m3/h	新风机送风状态点	热回收方式							
		13.76	16.0℃/60.0%	没有热回收							
	负荷统计	329.96	0.0	0.0	0.0	0.0	0.0	0.0	329.96	0.0	
		0.0	0.0	0.0	0.0	0.0					
10005[厨房]房间小计			1102.40	0.00	96.11	707.97	0.0	0.0	0.0	1102.40	0.0
			772.45	0.0	0.00	0.00	0.00				
10006[楼梯间]	房间参数		面积(m2)	高度(m)	室内设计温度(℃)	室内设计相对湿度(%)	放大系数				
			27.94	3.0	16.00	60.00	1.00				
	西外墙	参数	长(m)	宽(高)(m)	外墙面积(m2)	外墙净面积(m2)	传热系数	温差修正系数			
			2.24	3.0	6.72	6.72	0.34	1.0			
		负荷统计	96.88	0.0	0.0	96.88	-0.05	0.00	0.05	96.88	0.00
			96.88	0.00	0.0	0.0	0.0				
	北外墙	参数	长(m)	宽(高)(m)	外墙面积(m2)	外墙净面积(m2)	传热系数	温差修正系数			
			4.32	3.0	12.96	10.71	0.34	1.0			
		负荷统计	177.55	0.0	0.0	154.40	0.10	0.00	0.05	177.55	0.00
			177.55	0.00	0.0	0.0	0.0				
	北外窗_嵌	参数	长(m)	宽(高)(m)	面积(m2)	传热系数	缝隙长度(m)	渗透系数	安装高度(m)	温差修正系数	
			1.13	2.000	2.25	1.4	7.5	0.3	0.90	1.0	
		负荷统计	153.59	0.0	0.0	133.56	0.10	0.00	0.05	153.59	0.00
			153.59	0.00	0.00	0.00	0.0				
	东外墙	参数	长(m)	宽(高)(m)	外墙面积(m2)	外墙净面积(m2)	传热系数	温差修正系数			
			2.24	3.0	6.72	6.72	0.34	1.0			
		负荷统计	96.88	0.0	0.0	96.88	-0.05	0.00	0.05	96.88	0.00
			96.88	0.00	0.0	0.0	0.0				
	屋面	参数	长(m)	宽度(m)	面积(m2)	传热系数	温差修正系数				
			6.70	4.170	27.94	0.13	1.0				
负荷统计		154.01	0.0	0.0	154.01	0.00	0.00	0.0	154.01	0.00	
		154.01	0.00	0.0	0.0	0.0					
新风(热)	参数	新风量m3/h	新风机送风状态点	热回收方式							
		33.53	16.0℃/60.0%	没有热回收							
	负荷统计	804.03	0.0	0.0	0.0	0.0	0.0	0.0	804.03	0.0	
		0.0	0.0	0.0	0.0	0.0					
10006[楼梯间]房间小计			1482.93	0.00	53.08	635.71	0.0	0.0	0.0	1482.93	0.0
			678.90	0.0	0.00	0.00	0.00				
	房间参数		面积(m2)	高度(m)	室内设计温度(℃)	室内设计相对湿度(%)	放大系数				
			11.47	3.0	16.00	60.00	1.00				

10007[厨房]	北外墙	参数	长(m)	宽(高)(m)	外墙面积(m2)	外墙净面积(m2)	传热系数	温差修正系数	安装高度(m)	温差修正系数		
			9.92	3.0	29.76	24.96	0.34	1.0				
		负荷统计	395.81	0.0	0.0	359.82	0.10	0.00	0.00	395.81	0.00	
			395.81	0.00	0.0	0.0	0.0					
	北外墙_嵌	参数	长(m)	宽(高)(m)	面积(m2)	传热系数	缝隙长度(m)	渗透系数	安装高度(m)	温差修正系数		
			1.50	2.000	3.00	1.4	8.5	0.3				0.90
		负荷统计	195.89	0.0	0.0	178.08	0.10	0.00	0.0	195.89	0.00	
			195.89	0.00	0.00	0.00	0.0					
	北外墙_嵌	参数	长(m)	宽(高)(m)	面积(m2)	传热系数	缝隙长度(m)	渗透系数	安装高度(m)	温差修正系数		
			0.90	2.000	1.80	1.4	6.9	0.3	0.90	1.0		
		负荷统计	117.53	0.0	0.0	106.85	0.10	0.00	0.0	117.53	0.00	
			117.53	0.00	0.00	0.00	0.0					
	屋面	参数	长(m)	宽度(m)	面积(m2)	传热系数	温差修正系数					
			6.20	1.850	11.47	0.13	1.0					
		负荷统计	63.22	0.0	0.0	63.22	0.00	0.00	0.0	63.22	0.00	
			63.22	0.00	0.0	0.0	0.0					
	新风(热)	参数	新风量m3/h	新风机送风状态点	热回收方式							
			13.76	16.0℃/60.0%	没有热回收							
		负荷统计	329.96	0.0	0.0	0.0	0.0	0.0	0.0	329.96	0.0	
			0.0	0.0	0.0	0.0	0.0					
	10007[厨房]房间小计			1102.40	0.00	96.11	707.97	0.0	0.0	0.0	1102.40	0.0
				772.45	0.0	0.00	0.00	0.00				
	10008[起居室]	房间参数		面积(m2)	高度(m)	室内设计温度(℃)	室内设计相对湿度(%)	放大系数				
				57.18	3.0	20.00	60.00	1.00				
南外墙		参数	长(m)	宽(高)(m)	外墙面积(m2)	外墙净面积(m2)	传热系数	温差修正系数				
			12.08	3.0	36.24	27.69	0.34	1.0				
		负荷统计	371.31	0.0	0.0	436.84	-0.20	0.00	0.05	371.31	0.00	
			371.31	0.00	0.0	0.0	0.0					
南外墙_嵌		参数	长(m)	宽(高)(m)	面积(m2)	传热系数	缝隙长度(m)	渗透系数	安装高度(m)	温差修正系数		
			1.57	2.000	3.15	1.4	8.7	0.3	0.90	1.0		
		负荷统计	173.93	0.0	0.0	204.62	-0.20	0.00	0.05	173.93	0.00	
			173.93	0.00	0.00	0.00	0.0					
南外墙_嵌		参数	长(m)	宽(高)(m)	面积(m2)	传热系数	缝隙长度(m)	渗透系数	安装高度(m)	温差修正系数		
			2.70	2.000	5.40	1.4	11.4	0.3	0.60	1.0		
		负荷统计	298.17	0.0	0.0	350.78	-0.20	0.00	0.05	298.17	0.00	
			298.17	0.00	0.00	0.00	0.0					
西外墙		参数	长(m)	宽(高)(m)	外墙面积(m2)	外墙净面积(m2)	传热系数	温差修正系数				
			1.44	3.0	4.32	4.32	0.34	1.0				
		负荷统计	68.15	0.0	0.0	68.15	-0.05	0.00	0.05	68.15	0.00	
			68.15	0.00	0.0	0.0	0.0					
屋面		参数	长(m)	宽度(m)	面积(m2)	传热系数	温差修正系数					
			8.85	6.461	57.18	0.13	1.0					
		负荷统计	344.91	0.0	0.0	344.91	0.00	0.00	0.0	344.91	0.00	
			344.91	0.00	0.0	0.0	0.0					
新风(热)		参数	新风量m3/h	新风机送风状态点	热回收方式							
			68.62	20.0℃/60.0%	没有热回收							
	负荷统计	1890.07	0.0	0.0	0.0	0.0	0.0	0.0	1890.07	0.0		
		0.0	0.0	0.0	0.0	0.0						
10008[起居室]房间小计			3146.54	0.00	55.03	1405.31	0.0	0.0	0.0	3146.54	0.0	
			1256.47	0.0	0.00	0.00	0.00					

10009[卧室]	房间参数		面积(m2)	高度(m)	室内设计温度(℃)	室内设计相对湿度(%)	放大系数	城 建 工 程 有 限 公 司	乌设施审 - 2026年08月		
			10.15	3.0	20.00	60.00	1.00				
	东外墙	参数	长(m)	宽(高)(m)	外墙面积(m2)	外墙净面积(m2)	传热系数	温差修正系数			
			5.36	3.0	16.08	16.08	0.34	1.0			
		负荷统计	253.68	0.0	0.0	253.68	-0.05	0.00	0.05	253.68	0.00
			253.68	0.00	0.0	0.0	0.0				
	北外墙	参数	长(m)	宽(高)(m)	外墙面积(m2)	外墙净面积(m2)	传热系数	温差修正系数			
			4.32	3.0	12.96	10.26	0.34	1.0			
		负荷统计	186.14	0.0	0.0	161.86	0.10	0.00	0.05	186.14	0.00
			186.14	0.00	0.0	0.0	0.0				
	北外窗_嵌	参数	长(m)	宽(高)(m)	面积(m2)	传热系数	缝隙长度(m)	渗透系数	安装高度(m)	温差修正系数	
			1.35	2.000	2.70	1.4	8.1	0.3	0.90	1.0	
		负荷统计	201.70	0.0	0.0	175.39	0.10	0.00	0.05	201.70	0.00
			201.70	0.00	0.00	0.00	0.0				
	屋面	参数	长(m)	宽度(m)	面积(m2)	传热系数	温差修正系数				
			2.70	3.759	10.15	0.13	1.0				
		负荷统计	61.22	0.0	0.0	61.22	0.00	0.00	0.0	61.22	0.00
			61.22	0.00	0.0	0.0	0.0				
	新风(热)	参数	新风量m3/h	新风机送风状态点	热回收方式						
			12.18	20.0℃/60.0%	没有热回收						
		负荷统计	335.49	0.0	0.0	0.0	0.0	0.0	0.0	335.49	0.0
			0.0	0.0	0.0	0.0	0.0				
10009[卧室]房间小计			1038.23	0.00	102.29	652.16	0.0	0.0	0.0	1038.23	0.0
			702.74	0.0	0.00	0.00	0.00				
10010[卧室]	房间参数		面积(m2)	高度(m)	室内设计温度(℃)	室内设计相对湿度(%)	放大系数				
			17.20	3.0	20.00	60.00	1.00				
	南外墙	参数	长(m)	宽(高)(m)	外墙面积(m2)	外墙净面积(m2)	传热系数	温差修正系数			
			5.60	3.0	16.80	13.65	0.34	1.0			
		负荷统计	172.27	0.0	0.0	215.34	-0.20	0.00	0.0	172.27	0.00
			172.27	0.00	0.0	0.0	0.0				
	南外窗_嵌	参数	长(m)	宽(高)(m)	面积(m2)	传热系数	缝隙长度(m)	渗透系数	安装高度(m)	温差修正系数	
			1.57	2.000	3.15	1.4	8.7	0.3	0.90	1.0	
		负荷统计	163.70	0.0	0.0	204.62	-0.20	0.00	0.0	163.70	0.00
			163.70	0.00	0.00	0.00	0.0				
	屋面	参数	长(m)	宽度(m)	面积(m2)	传热系数	温差修正系数				
			3.50	4.914	17.20	0.13	1.0				
		负荷统计	103.75	0.0	0.0	103.75	0.00	0.00	0.0	103.75	0.00
			103.75	0.00	0.0	0.0	0.0				
	新风(热)	参数	新风量m3/h	新风机送风状态点	热回收方式						
			20.64	20.0℃/60.0%	没有热回收						
		负荷统计	568.51	0.0	0.0	0.0	0.0	0.0	0.0	568.51	0.0
			0.0	0.0	0.0	0.0	0.0				
10010[卧室]房间小计			1008.23	0.00	58.62	523.72	0.0	0.0	0.0	1008.23	0.0
			439.72	0.0	0.00	0.00	0.00				
	房间参数		面积(m2)	高度(m)	室内设计温度(℃)	室内设计相对湿度(%)	放大系数				
			7.92	3.0	20.00	60.00	1.00				
		参数	长(m)	宽(高)(m)	外墙面积(m2)	外墙净面积(m2)	传热系数	温差修正系数			

1
号
楼
10
层

10011[卫生间]	北外墙		1.28	3.0	3.84	3.16	0.34	1.0	0.0	0.0	0.0
		负荷	54.84	0.0	0.0	49.85	0.10	0.00	0.0	54.84	0.00
		统计	54.84	0.00	0.0	0.0	0.0				
	北外墙_嵌	参数	长(m)	宽(高)(m)	面积(m2)	传热系数	缝隙长度(m)	渗透系数	安装高度(m)	温差修正系数	
			0.34	2.000	0.68	1.4	5.4	0.3	0.90	1.0	
		负荷	48.59	0.0	0.0	44.17	0.10	0.00	0.0	48.59	0.00
	屋面	统计	48.59	0.00	0.00	0.00	0.0				
		参数	长(m)	宽度(m)	面积(m2)	传热系数	温差修正系数				
			2.20	3.600	7.92	0.13	1.0				
	新风(热)	负荷	47.77	0.0	0.0	47.77	0.00	0.00	0.0	47.77	0.00
		统计	47.77	0.00	0.0	0.0	0.0				
		参数	新风量m3/h	新风机送风状态点	热回收方式						
	新风(热)		9.50	20.0℃/60.0%	没有热回收						
		负荷	261.67	0.0	0.0	0.0	0.0	0.0	0.0	261.67	0.0
		统计	0.0	0.0	0.0	0.0	0.0				
10011[卫生间]房间小计			412.87	0.00	52.13	141.80	0.0	0.0	0.0	412.87	0.0
			151.20	0.0	0.00	0.00	0.00				
10012[卫生间]	房间参数		面积(m2)	高度(m)	室内设计温度(℃)	室内设计相对湿度(%)	放大系数				
			7.92	3.0	20.00	60.00	1.00				
	北外墙	参数	长(m)	宽(高)(m)	外墙面积(m2)	外墙净面积(m2)	传热系数	温差修正系数			
			1.28	3.0	3.84	3.16	0.34	1.0			
		负荷	54.84	0.0	0.0	49.85	0.10	0.00	0.0	54.84	0.00
	北外墙_嵌	统计	54.84	0.00	0.0	0.0	0.0				
		参数	长(m)	宽(高)(m)	面积(m2)	传热系数	缝隙长度(m)	渗透系数	安装高度(m)	温差修正系数	
			0.34	2.000	0.68	1.4	5.4	0.3	0.90	1.0	
	屋面	负荷	48.59	0.0	0.0	44.17	0.10	0.00	0.0	48.59	0.00
		统计	48.59	0.00	0.00	0.00	0.0				
		参数	长(m)	宽度(m)	面积(m2)	传热系数	温差修正系数				
	新风(热)		2.20	3.600	7.92	0.13	1.0				
		负荷	47.77	0.0	0.0	47.77	0.00	0.00	0.0	47.77	0.00
		统计	47.77	0.00	0.0	0.0	0.0				
10012[卫生间]房间小计			412.87	0.00	52.13	141.80	0.0	0.0	0.0	412.87	0.0
			151.20	0.0	0.00	0.00	0.00				
10013[卧室]	房间参数		面积(m2)	高度(m)	室内设计温度(℃)	室内设计相对湿度(%)	放大系数				
			17.20	3.0	20.00	60.00	1.00				
	南外墙	参数	长(m)	宽(高)(m)	外墙面积(m2)	外墙净面积(m2)	传热系数	温差修正系数			
			5.60	3.0	16.80	13.65	0.34	1.0			
		负荷	172.27	0.0	0.0	215.34	-0.20	0.00	0.0	172.27	0.00
	南外墙_嵌	统计	172.27	0.00	0.0	0.0	0.0				
		参数	长(m)	宽(高)(m)	面积(m2)	传热系数	缝隙长度(m)	渗透系数	安装高度(m)	温差修正系数	
			1.57	2.000	3.15	1.4	8.7	0.3	0.90	1.0	
	屋面	负荷	163.70	0.0	0.0	204.62	-0.20	0.00	0.0	163.70	0.00
		统计	163.70	0.00	0.00	0.00	0.0				
		参数	长(m)	宽度(m)	面积(m2)	传热系数	温差修正系数				
	屋面		3.50	4.914	17.20	0.13	1.0				
		统计									

10015[
起居
室]

	屋面	统计	68.15	0.00	0.0	0.0	0.0		城建工程有限公司	乌设施审-2026	2026年08月	
		参数	长(m)	宽度(m)	面积(m2)	传热系数	温差修正系数					
			8.85	6.461	57.18	0.13	1.0					
		负荷统计	344.91	0.0	0.0	344.91	0.00	0.00				
	新风(热)	参数	新风量 m3/h	新风机送风状态点	热回收方式							
			68.62	20.0℃ /60.0%	没有热回收							
		负荷统计	1890.07	0.0	0.0	0.0	0.0	0.0	0.0	1890.07	0.0	
			0.0	0.0	0.0	0.0	0.0					
	10015[起居室]房间小计		3146.54	0.00	55.03	1405.31	0.0	0.0	0.0	3146.54	0.0	
			1256.47	0.0	0.00	0.00	0.00					
10016[厨房]	房间参数		面积(m2)	高度(m)	室内设计温度(℃)	室内设计相对湿度(%)	放大系数					
			11.47	3.0	16.00	60.00	1.00					
	北外墙	参数	长(m)	宽(高)(m)	外墙面积(m2)	外墙净面积(m2)	传热系数	温差修正系数				
			9.92	3.0	29.76	24.96	0.34	1.0				
		负荷统计	395.81	0.0	0.0	359.82	0.10	0.00	0.0	395.81	0.00	
			395.81	0.00	0.0	0.0	0.0					
	北外窗_嵌	参数	长(m)	宽(高)(m)	面积(m2)	传热系数	缝隙长度(m)	渗透系数	安装高度(m)	温差修正系数		
			1.50	2.000	3.00	1.4	8.5	0.3	0.90	1.0		
		负荷统计	195.89	0.0	0.0	178.08	0.10	0.00	0.0	195.89	0.00	
			195.89	0.00	0.00	0.00	0.0					
	北外窗_嵌	参数	长(m)	宽(高)(m)	面积(m2)	传热系数	缝隙长度(m)	渗透系数	安装高度(m)	温差修正系数		
			0.90	2.000	1.80	1.4	6.9	0.3	0.90	1.0		
		负荷统计	117.53	0.0	0.0	106.85	0.10	0.00	0.0	117.53	0.00	
			117.53	0.00	0.00	0.00	0.0					
	屋面	参数	长(m)	宽度(m)	面积(m2)	传热系数	温差修正系数					
			6.20	1.850	11.47	0.13	1.0					
		负荷统计	63.22	0.0	0.0	63.22	0.00	0.00	0.0	63.22	0.00	
			63.22	0.00	0.0	0.0	0.0					
	新风(热)	参数	新风量 m3/h	新风机送风状态点	热回收方式							
			13.76	16.0℃ /60.0%	没有热回收							
负荷统计		329.96	0.0	0.0	0.0	0.0	0.0	0.0	329.96	0.0		
		0.0	0.0	0.0	0.0	0.0						
10016[厨房]房间小计		1102.40	0.00	96.11	707.97	0.0	0.0	0.0	1102.40	0.0		
		772.45	0.0	0.00	0.00	0.00						
10017[楼梯间]	房间参数		面积(m2)	高度(m)	室内设计温度(℃)	室内设计相对湿度(%)	放大系数					
			27.94	3.0	16.00	60.00	1.00					
	东外墙	参数	长(m)	宽(高)(m)	外墙面积(m2)	外墙净面积(m2)	传热系数	温差修正系数				
			2.24	3.0	6.72	6.72	0.34	1.0				
		负荷统计	96.88	0.0	0.0	96.88	-0.05	0.00	0.05	96.88	0.00	
			96.88	0.00	0.0	0.0	0.0					
	北外墙	参数	长(m)	宽(高)(m)	外墙面积(m2)	外墙净面积(m2)	传热系数	温差修正系数				
			4.32	3.0	12.96	10.71	0.34	1.0				
		负荷统计	177.55	0.0	0.0	154.40	0.10	0.00	0.05	177.55	0.00	
			177.55	0.00	0.0	0.0	0.0					
	北外窗_嵌	参数	长(m)	宽(高)(m)	面积(m2)	传热系数	缝隙长度(m)	渗透系数	安装高度(m)	温差修正系数		
			1.13	2.000	2.25	1.4	7.5	0.3	0.90	1.0		
		负荷统计	153.59	0.0	0.0	133.56	0.10	0.00	0.05	153.59	0.00	
			153.59	0.00	0.00	0.00	0.0					

10017[楼梯间]	西外墙	参数	长(m)	宽(高)(m)	外墙面积(m2)	外墙净面积(m2)	传热系数	温差修正系数			
			2.24	3.0	6.72	6.72	0.34	1.0			
		负荷统计	96.88	0.0	0.0	96.88	-0.05	0.00	0.05	96.88	0.00
	屋面	参数	长(m)	宽度(m)	面积(m2)	传热系数	温差修正系数				
			6.70	4.170	27.94	0.13	1.0				
		负荷统计	154.01	0.0	0.0	154.01	0.00	0.00	0.0	154.01	0.00
	新风(热)	参数	新风量m3/h	新风机送风状态点	热回收方式						
			33.53	16.0℃/60.0%	没有热回收						
		负荷统计	804.03	0.0	0.0	0.0	0.0	0.0	0.0	804.03	0.0
	10017[楼梯间]房间小计		1482.93	0.00	53.08	635.71	0.0	0.0	0.0	1482.93	0.0
			678.90	0.0	0.00	0.00	0.00				
10018[厨房]	房间参数		面积(m2)	高度(m)	室内设计温度(℃)	室内设计相对湿度(%)	放大系数				
			11.47	3.0	16.00	60.00	1.00				
	北外墙	参数	长(m)	宽(高)(m)	外墙面积(m2)	外墙净面积(m2)	传热系数	温差修正系数			
			9.92	3.0	29.76	24.96	0.34	1.0			
		负荷统计	395.81	0.0	0.0	359.82	0.10	0.00	0.0	395.81	0.00
	北外窗_嵌	参数	长(m)	宽(高)(m)	面积(m2)	传热系数	缝隙长度(m)	渗透系数	安装高度(m)	温差修正系数	
			1.50	2.000	3.00	1.4	8.5	0.3	0.90	1.0	
		负荷统计	195.89	0.0	0.0	178.08	0.10	0.00	0.0	195.89	0.00
	北外窗_嵌	参数	长(m)	宽(高)(m)	面积(m2)	传热系数	缝隙长度(m)	渗透系数	安装高度(m)	温差修正系数	
			0.90	2.000	1.80	1.4	6.9	0.3	0.90	1.0	
		负荷统计	117.53	0.0	0.0	106.85	0.10	0.00	0.0	117.53	0.00
	屋面	参数	长(m)	宽度(m)	面积(m2)	传热系数	温差修正系数				
			6.20	1.850	11.47	0.13	1.0				
		负荷统计	63.22	0.0	0.0	63.22	0.00	0.00	0.0	63.22	0.00
	新风(热)	参数	新风量m3/h	新风机送风状态点	热回收方式						
			13.76	16.0℃/60.0%	没有热回收						
		负荷统计	329.96	0.0	0.0	0.0	0.0	0.0	0.0	329.96	0.0
	10018[厨房]房间小计		1102.40	0.00	96.11	707.97	0.0	0.0	0.0	1102.40	0.0
			772.45	0.0	0.00	0.00	0.00				
	房间参数		面积(m2)	高度(m)	室内设计温度(℃)	室内设计相对湿度(%)	放大系数				
			57.18	3.0	20.00	60.00	1.00				
	南外墙	参数	长(m)	宽(高)(m)	外墙面积(m2)	外墙净面积(m2)	传热系数	温差修正系数			
			12.08	3.0	36.24	27.69	0.34	1.0			
		负荷统计	371.31	0.0	0.0	436.84	-0.20	0.00	0.05	371.31	0.00
	南外窗_嵌	参数	长(m)	宽(高)(m)	面积(m2)	传热系数	缝隙长度(m)	渗透系数	安装高度(m)	温差修正系数	
			2.70	2.000	5.40	1.4	11.4	0.3	0.60	1.0	
		负荷统计	298.17	0.0	0.0	350.78	-0.20	0.00	0.05	298.17	0.00

10019[起居室]	南外窗_嵌	参数	长(m)	宽(高)(m)	面积(m2)	传热系数	缝隙长度(m)	渗透系数	安装高度(m)	温差修正系数	
			1.57	2.000	3.15	1.4	8.7	0.3	0.90	1.0	
		负荷统计	173.93	0.0	0.0	204.62	-0.20	0.00	0.05	173.93	0.00
	西外墙	参数	长(m)	宽(高)(m)	外墙面积(m2)	外墙净面积(m2)	传热系数	温差修正系数			
			1.44	3.0	4.32	4.32	0.34	1.0			
		负荷统计	68.15	0.0	0.0	68.15	-0.05	0.00	0.05	68.15	0.00
	屋面	参数	长(m)	宽度(m)	面积(m2)	传热系数	温差修正系数				
			8.85	6.461	57.18	0.13	1.0				
		负荷统计	344.91	0.0	0.0	344.91	0.00	0.00	0.0	344.91	0.00
	新风(热)	参数	新风量m3/h	新风机送风状态点	热回收方式						
			68.62	20.0℃/60.0%	没有热回收						
		负荷统计	1890.07	0.0	0.0	0.0	0.0	0.0	0.0	1890.07	0.0
10019[起居室]房间小计			3146.54	0.00	55.03	1405.31	0.0	0.0	0.0	3146.54	0.0
			1256.47	0.0	0.00	0.00	0.00				
10020[卧室]	房间参数		面积(m2)	高度(m)	室内设计温度(℃)	室内设计相对湿度(%)	放大系数				
			12.83	3.0	20.00	60.00	1.00				
	东外墙	参数	长(m)	宽(高)(m)	外墙面积(m2)	外墙净面积(m2)	传热系数	温差修正系数			
			5.36	3.0	16.08	16.08	0.34	1.0			
		负荷统计	253.68	0.0	0.0	253.68	-0.05	0.00	0.05	253.68	0.00
	北外墙	参数	长(m)	宽(高)(m)	外墙面积(m2)	外墙净面积(m2)	传热系数	温差修正系数			
			5.60	3.0	16.80	13.65	0.34	1.0			
		负荷统计	247.64	0.0	0.0	215.34	0.10	0.00	0.05	247.64	0.00
	北外窗_嵌	参数	长(m)	宽(高)(m)	面积(m2)	传热系数	缝隙长度(m)	渗透系数	安装高度(m)	温差修正系数	
			1.57	2.000	3.15	1.4	8.7	0.3	0.90	1.0	
		负荷统计	235.32	0.0	0.0	204.62	0.10	0.00	0.05	235.32	0.00
	屋面	参数	长(m)	宽度(m)	面积(m2)	传热系数	温差修正系数				
			3.50	3.666	12.83	0.13	1.0				
		负荷统计	77.39	0.0	0.0	77.39	0.00	0.00	0.0	77.39	0.00
	新风(热)	参数	新风量m3/h	新风机送风状态点	热回收方式						
			15.40	20.0℃/60.0%	没有热回收						
		负荷统计	424.18	0.0	0.0	0.0	0.0	0.0	0.0	424.18	0.0
10020[卧室]房间小计			1238.21	0.00	96.51	751.04	0.0	0.0	0.0	1238.21	0.0
			814.03	0.0	0.00	0.00	0.00				
	房间参数		面积(m2)	高度(m)	室内设计温度(℃)	室内设计相对湿度(%)	放大系数				
			17.20	3.0	20.00	60.00	1.00				
	南外墙	参数	长(m)	宽(高)(m)	外墙面积(m2)	外墙净面积(m2)	传热系数	温差修正系数			
			5.60	3.0	16.80	13.65	0.34	1.0			
		负荷统计	183.04	0.0	0.0	215.34	-0.20	0.00	0.05	183.04	0.00
			183.04	0.00	0.0	0.0	0.0				

10021[卧室]	南外窗_嵌	参数	长(m)	宽(高)(m)	面积(m2)	传热系数	缝隙长度(m)	渗透系数	安装高度(m)	温差修正系数		
			1.57	2.000	3.15	1.4	8.7	0.3	1.0			
		负荷统计	173.93	0.0	0.0	204.62	-0.20	0.00	0.05	173.93	0.00	
			173.93	0.00	0.00	0.00	0.0					
		东外墙	参数	长(m)	宽(高)(m)	外墙面积(m2)	外墙净面积(m2)	传热系数	温差修正系数			
				7.12	3.0	21.36	21.36	0.34	1.0			
	负荷统计		336.98	0.0	0.0	336.98	-0.05	0.00	0.05	336.98	0.00	
			336.98	0.00	0.0	0.0	0.0					
	屋面		参数	长(m)	宽度(m)	面积(m2)	传热系数	温差修正系数				
				3.50	4.914	17.20	0.13	1.0				
		负荷统计	103.75	0.0	0.0	103.75	0.00	0.00	0.0	103.75	0.00	
			103.75	0.00	0.0	0.0	0.0					
		新风(热)	参数	新风量m3/h	新风机送风状态点	热回收方式						
				20.64	20.0℃/60.0%	没有热回收						
	负荷统计		568.51	0.0	0.0	0.0	0.0	0.0	0.0	568.51	0.0	
			0.0	0.0	0.0	0.0	0.0					
	10021[卧室]房间小计		1366.21	0.00	79.43	860.69	0.0	0.0	0.0	1366.21	0.0	
			797.70	0.0	0.00	0.00	0.00					
	10022[卫生间]	房间参数		面积(m2)	高度(m)	室内设计温度(℃)	室内设计相对湿度(%)	放大系数				
				7.92	3.0	20.00	60.00	1.00				
		东外墙	参数	长(m)	宽(高)(m)	外墙面积(m2)	外墙净面积(m2)	传热系数	温差修正系数			
				5.76	3.0	17.28	15.48	0.34	1.0			
			负荷统计	232.00	0.0	0.0	244.21	-0.05	0.00	0.0	232.00	0.00
				232.00	0.00	0.0	0.0	0.0				
		东外窗_嵌	参数	长(m)	宽(高)(m)	面积(m2)	传热系数	缝隙长度(m)	渗透系数	安装高度(m)	温差修正系数	
				0.45	2.000	0.90	1.4	5.7	0.3	0.90	1.0	
			负荷统计	55.54	0.0	0.0	58.46	-0.05	0.00	0.0	55.54	0.00
				55.54	0.00	0.00	0.00	0.0				
		东外窗_嵌	参数	长(m)	宽(高)(m)	面积(m2)	传热系数	缝隙长度(m)	渗透系数	安装高度(m)	温差修正系数	
				0.45	2.000	0.90	1.4	5.7	0.3	0.90	1.0	
			负荷统计	55.54	0.0	0.0	58.46	-0.05	0.00	0.0	55.54	0.00
				55.54	0.00	0.00	0.00	0.0				
		屋面	参数	长(m)	宽度(m)	面积(m2)	传热系数	温差修正系数				
2.20				3.600	7.92	0.13	1.0					
负荷统计			47.77	0.0	0.0	47.77	0.00	0.00	0.0	47.77	0.00	
			47.77	0.00	0.0	0.0	0.0					
新风(热)		参数	新风量m3/h	新风机送风状态点	热回收方式							
			9.50	20.0℃/60.0%	没有热回收							
		负荷统计	261.67	0.0	0.0	0.0	0.0	0.0	0.0	261.67	0.0	
	0.0		0.0	0.0	0.0	0.0						
10022[卫生间]房间小计		652.52	0.00	82.39	408.91	0.0	0.0	0.0	652.52	0.0		
		390.86	0.0	0.00	0.00	0.00						
10层小计		31394.18	0.00	65.83	16401.18	0.0	0.0	0.0	31394.18	0.0		
		16066.00	0.0	0.00	0.00	0.00						
1号楼小计		318232.96	0.00	66.84	136938.48	0.0	0.0	0.0	287742.36	0.0		
		165345.09	0.0	1872.22	30490.60	0.00						
工程合计		318232.96	0.00	66.84	136938.48	0.0	0.0	0.0	287742.36	0.0		
		165345.09	0.0	1872.22	30490.60	0.00						

新疆设计审查有限公司
新疆维吾尔自治区
施工图审查专用章

乌设施审-2026-260-3
2026年08月31日


低区地暖干管水力计算												
系统压力为			10000	Pa	+	13962	Pa	=	23962	Pa	-2026-2030-3	
供水管段	热负荷		管径 d mm	计算管径	管长 L m	单位摩阻 R Pa/m	摩损 RxL Pa	速度 V m/s	局部阻力损失 Z=hw (pa)	总阻力 RL+Z Pa	末端压力 ΔP2 (Pa)	
	W	Kg/h										
1~2	24000	2064	DN40	41	3	74	221	0.43	110	331	10000	
2~3	48000	4128	DN50	53	3	76	227	0.52	113	340		
3~4	72000	6192	DN70	68	3	46	139	0.47	69	208		
4~5	96000	8256	DN80	81	3	33	99	0.45	49	148		
5~6	120000	10320	DN80	81	3	51	152	0.56	76	228		
6~7	144000	12384	DN80	81	3	72	217	0.67	109	326		
7~8	168000	14448	DN100	106	3	25	74	0.45	37	110		
8~9	192000	16512	DN100	106	3	32	95	0.52	48	143		
9~10	216000	18576	DN100	106	3	40	120	0.58	60	180		
11~12	240000	20640	DN100	106	3	49	147	0.65	74	221		
13~14	480000	41280	DN125	131	22	64	1403	0.85	701	2104		
					24					1834		
地暖系统水力平衡计算：						末端压力	10000	Pa				
序号	热负荷		管径 d mm	计算管径	管长 L m	单位摩阻 R Pa/m	摩损 RxL Pa	速度 V m/s	末端压力	总阻力 RL+Z Pa	资用压力	不平衡率
	W	Kg/h							Δ P2(Pa)		Δ P2(Pa)	
Ng-1	240000	20640	DN100	106	22	49	1079	0.65	10000	11079	11079	0.1
Ng-2	240000	20640	DN100	106	12	49	588	0.65	10000	10588	10588	0.06
结论 由计算可以得出，最不利环路和最有利环路之间的不平衡率为10.1%，满足规范要求。												

新疆
设计
审查
有限
公司
工程


施工图审查专用章
乌设施审 - 2026-260-3
2026年08月31日


内走道机械排烟系统单个风口风量计算书

防烟分区：地下1层、地下2层内走道						程	
计算部位：内走道风口排烟量计算							
储烟仓高度(m)						1.45	
排烟区域净高H' (m)						2.90	
清晰高度H _q (m) （空间净高>3m时，≦1.6+0.1·H'；空间净高≤3m时，≦1/2净高）						1.45	
火灾热释放速率Q (kw) = α t ² （取值不小于表4.6.7注意单位）						1500.00	
热释放速率的对流部分Q _c (kw) =0.7Q						1050.00	
燃料面到烟层底部的高度Z (m) （取值应≥H _q 与燃料面高度之差）						1.45	
火焰极限高度Z ₁ (m)						2.68	
轴对称型烟羽流： (kg/s) M _p						3.01	
Z>Z ₁ 时		M _p =0.071Q _c ^{1/3} Z ^{5/3} +0.0018Q _c					
Z≤Z ₁ 时		M _p =0.032Q _c ^{3/5} Z					
自然排烟或机械排烟时K取值（自排，K=0.5，机械排，K=1.0）						1.00	
烟层平均温度 (T) 与环境温度 (T ₀) 的差ΔT (K) =KQ _c /M _p C _p						344.85	
防火分区计算排烟量 V (m ³ /s) =（不应小于规范4.6.3-4当公共建筑房间内与走道或回廊均需设置排烟时，其走道或回廊的机械排烟量可按60m3/（h·m2）计算且不小于13000m3/h条规定）						13000.00	
按60m3/（h·m2）计算单个防烟分区排烟量（m3/s）				面积(m2)	90	5400.00	
单个排烟口最大排烟量计算（m ³ /s）：							
排烟位置系数 γ						0.50	
排烟系统吸入口最低点之下烟气层厚度（m） d _b （储烟仓是否在梁下，管道是否在梁下）						1.25	
烟层的平均绝对温度（K） T						638.00	
V _{max} =4.16·γ·d _b ^{5/2} ·[(T-T ₀)/T ₀] ^{1/2}						14187.77	
单个排烟口设计排烟量（m3/s）						3.94	

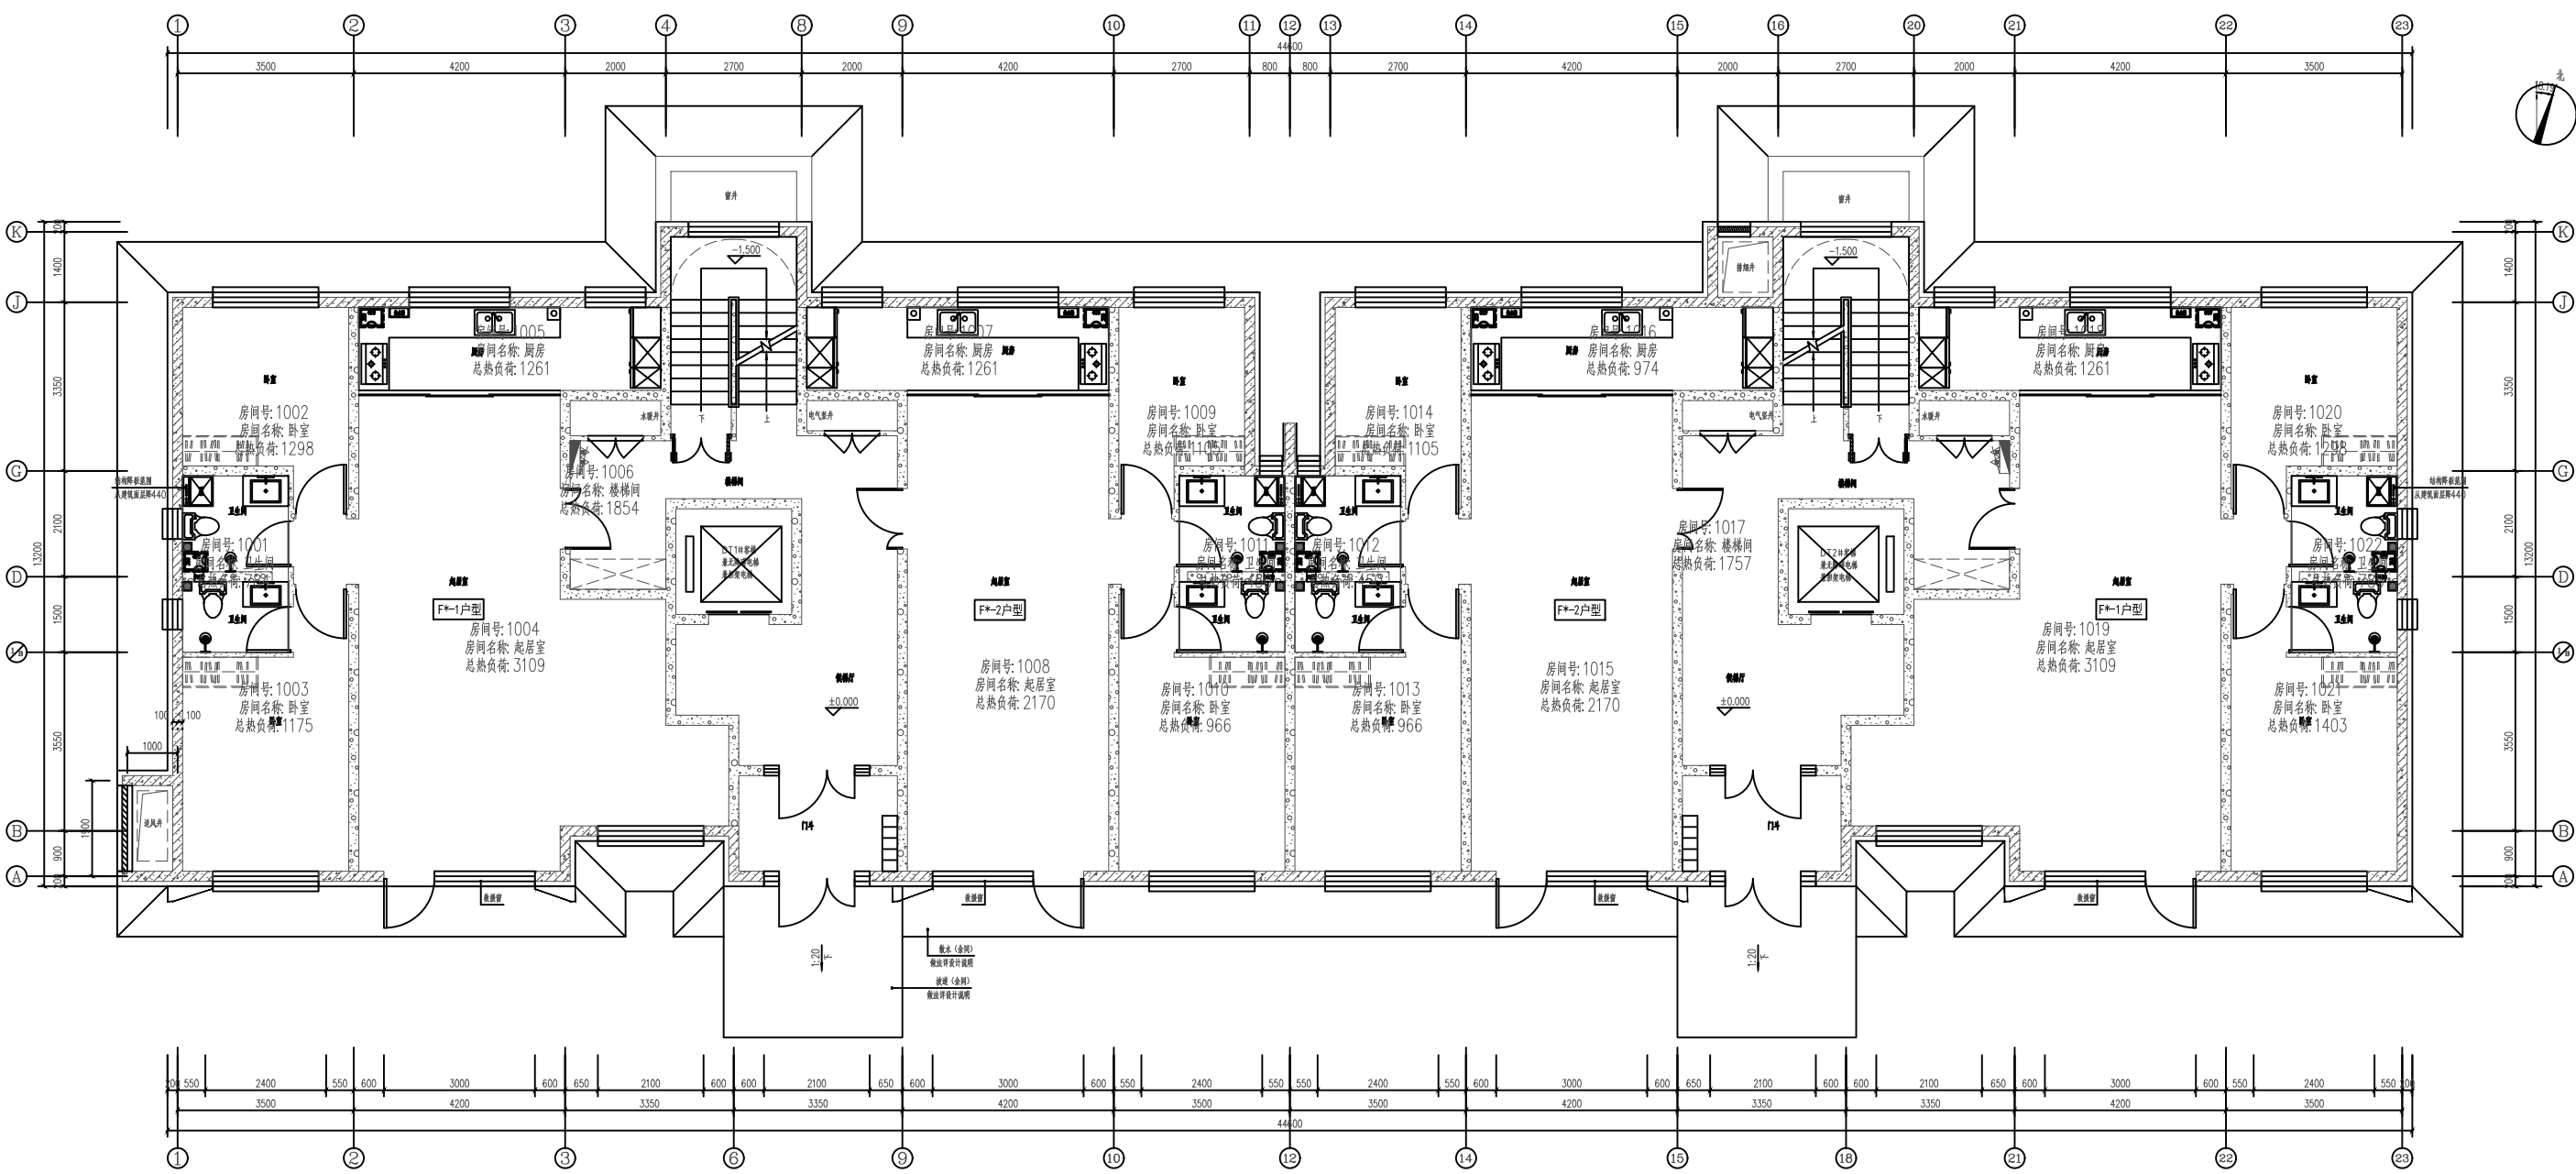

一层采暖负荷计算平面图 1:50
本层建筑面积: 525.63m²
总建筑面积: 6248.29m²
地上建筑面积: 5251.33m²
地下建筑面积: 996.96m²

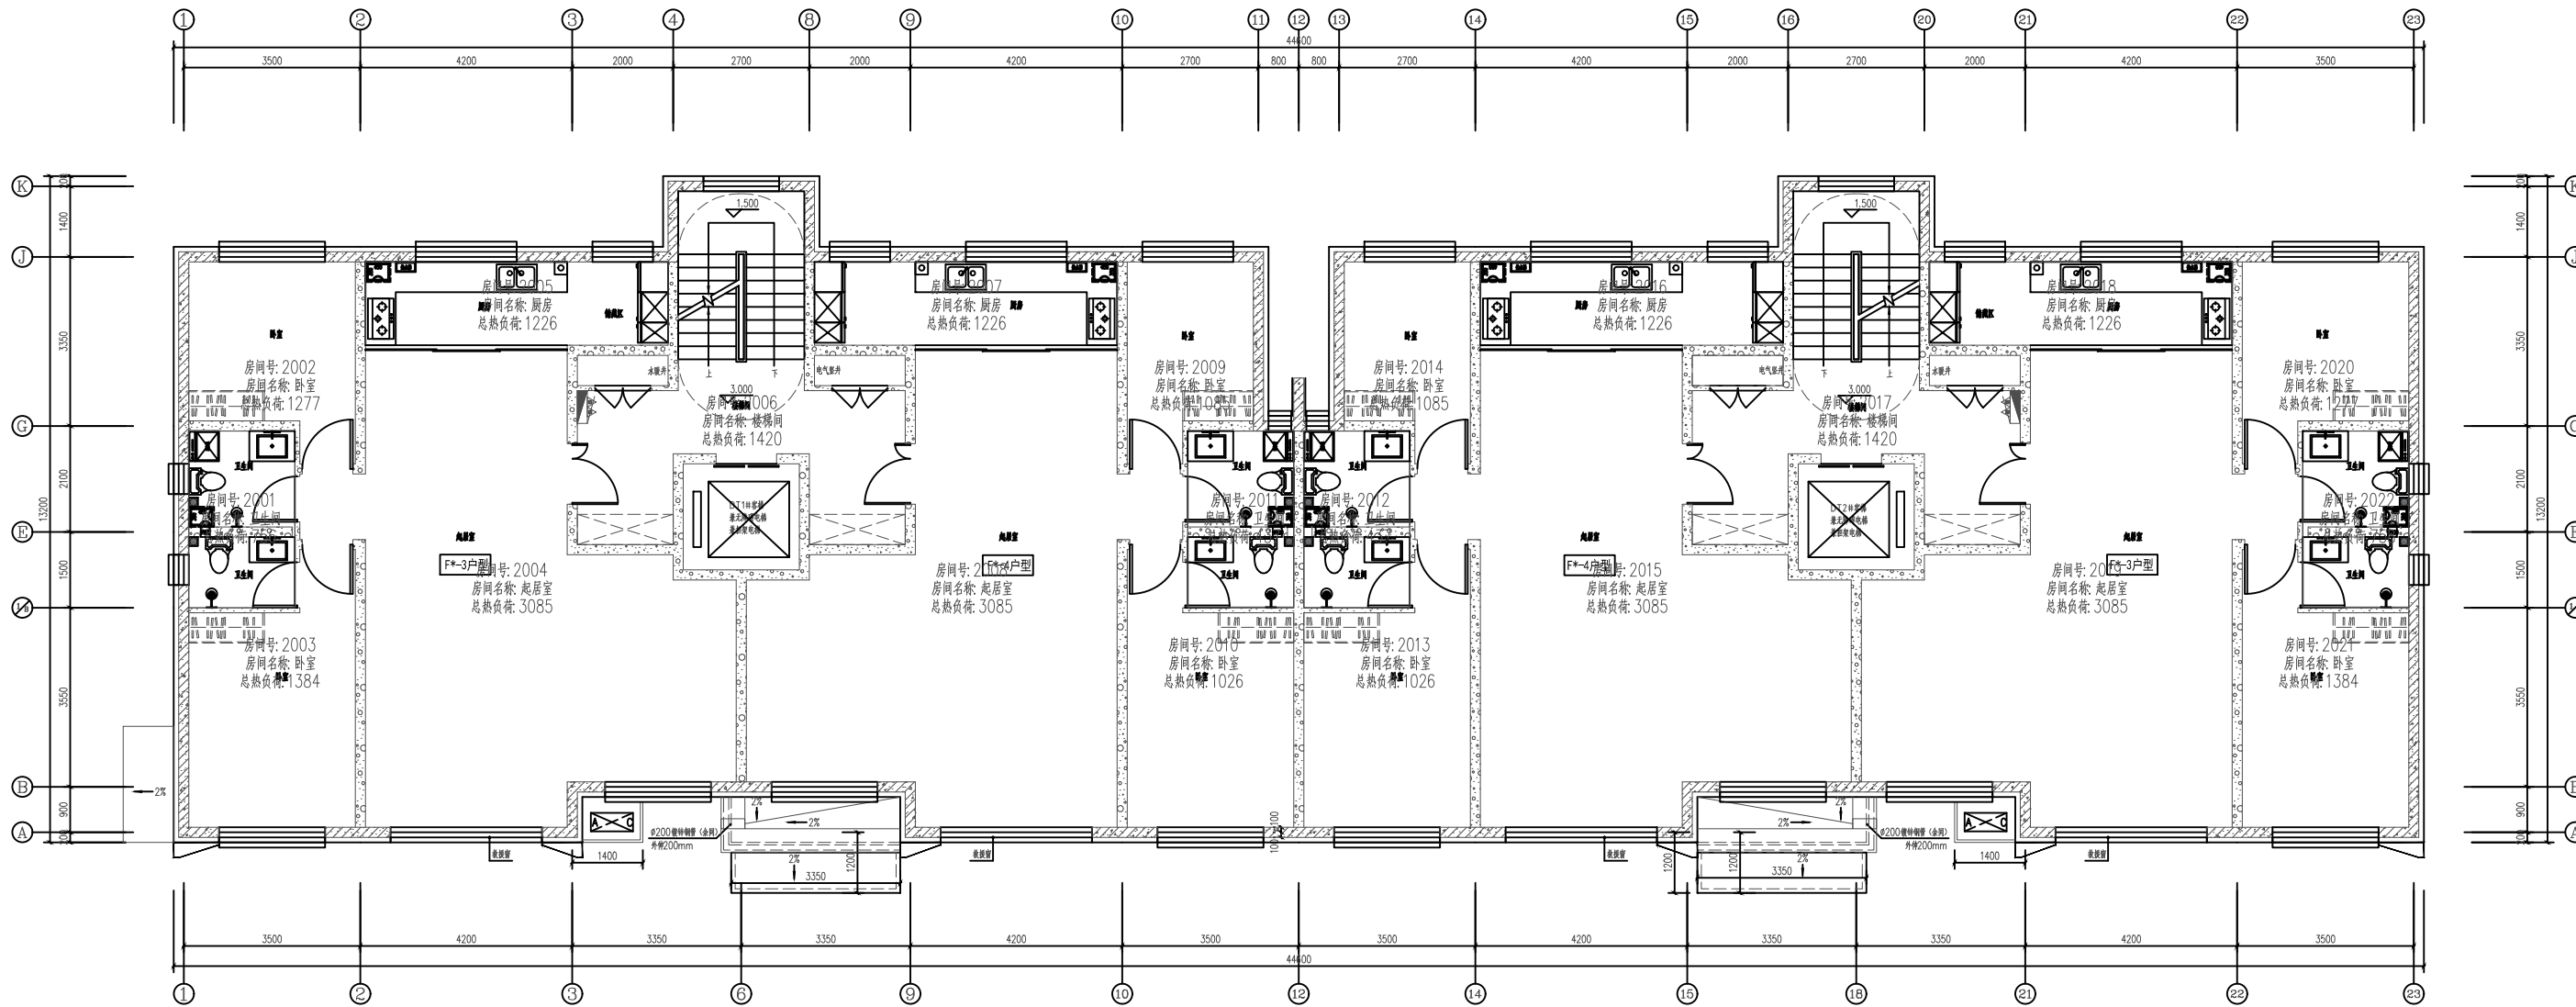

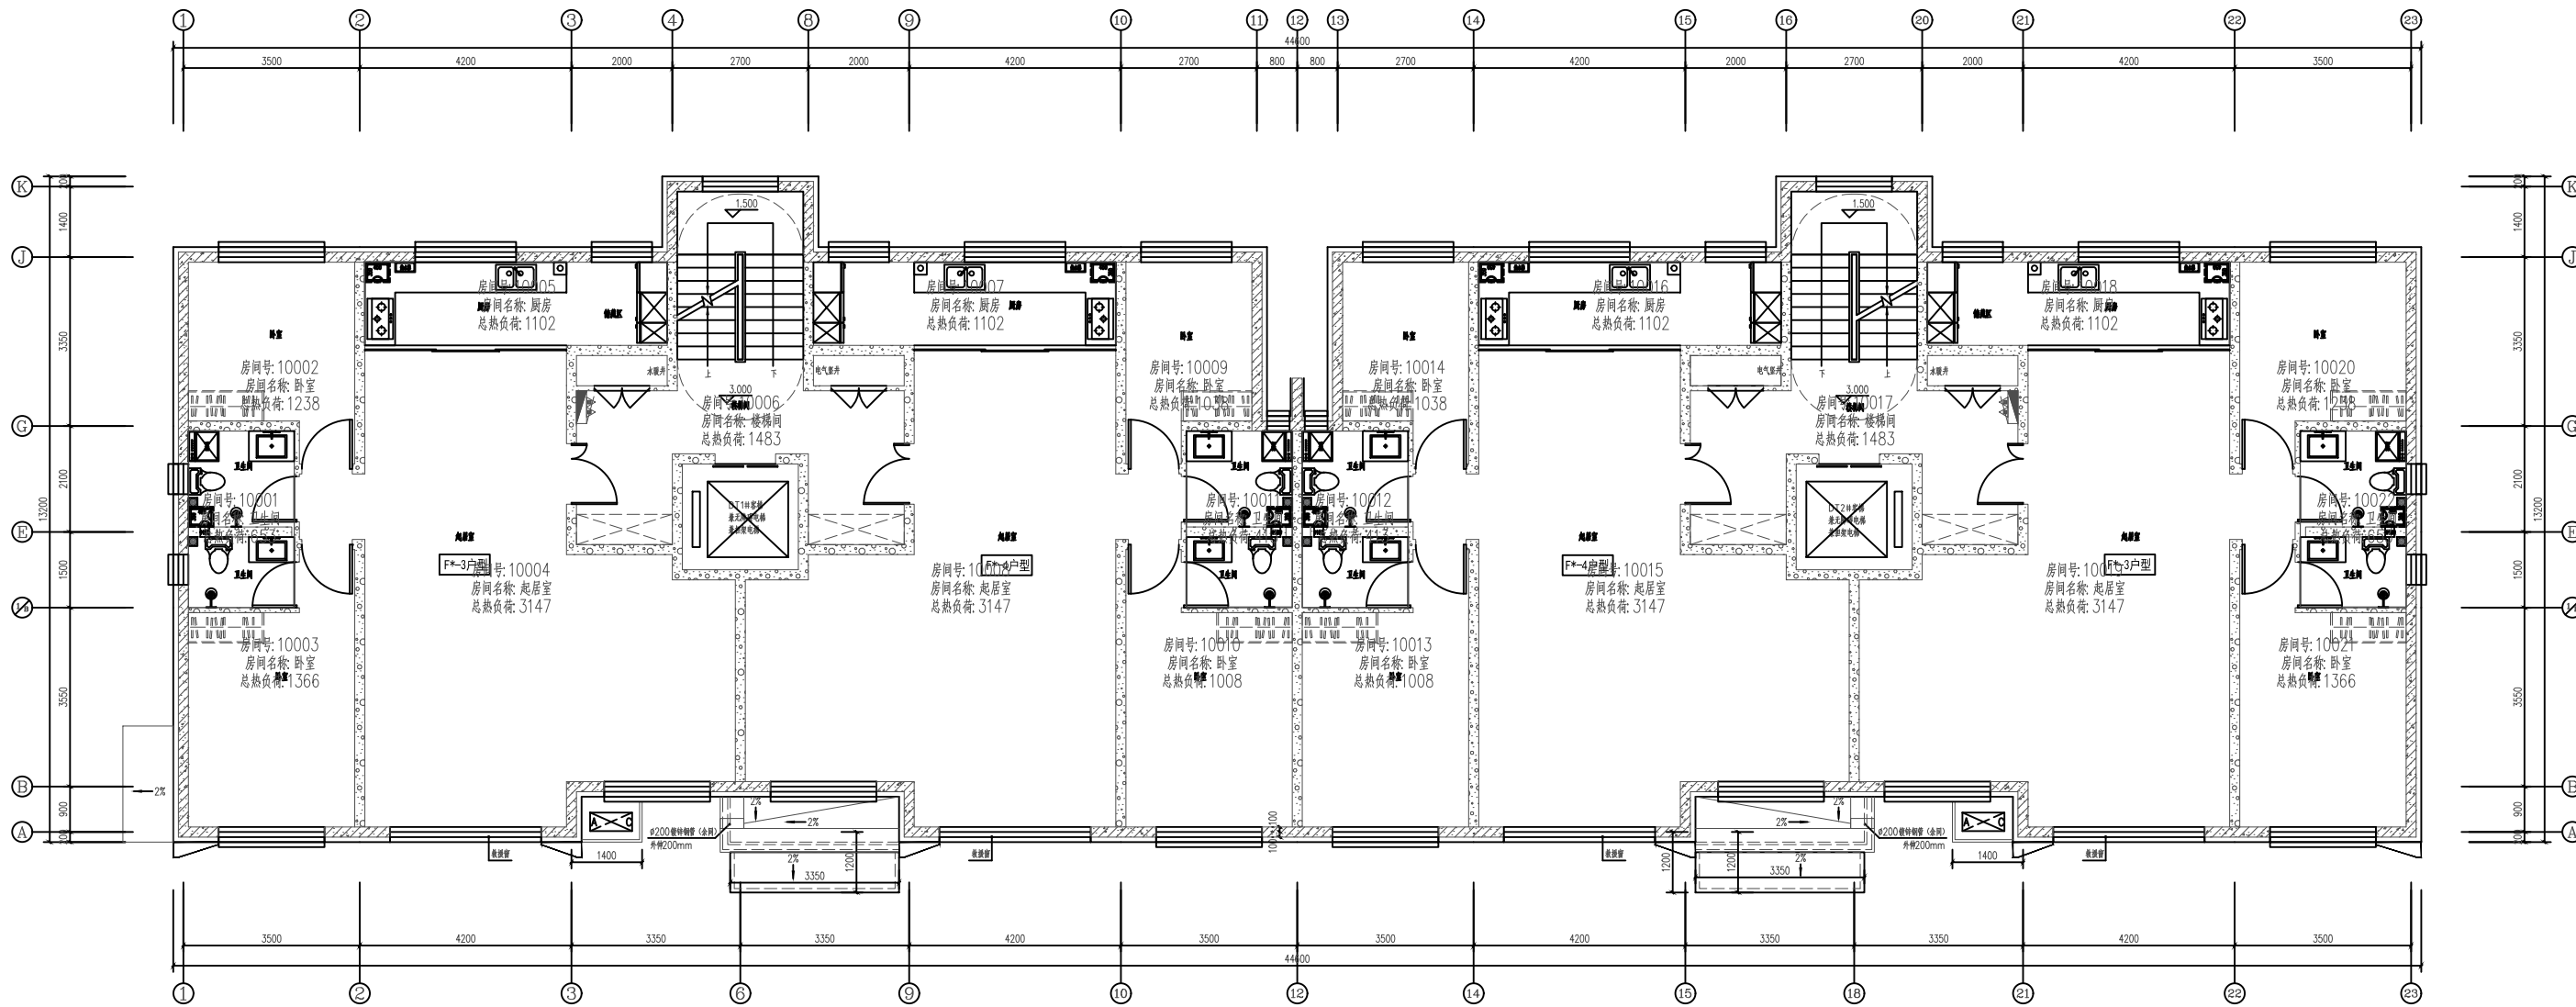

十层采暖负荷计算平面图 1:50
本层建筑面积: 519.60m²
总建筑面积: 6248.29m²