

永忠工程管理(集团)有限公司  
Yong Zhong Engineering Management (Group) Co., Ltd.  
甲级工程设计证书编号: A151027583

合作设计-顾问单位 CONSULTING ARCHITECT  
设计部门 新疆分公司

电 话 18999878562

说明:  
1、本图版权为本设计院拥有, 任何人士如未获允许不得翻印任何部分。  
2、所有尺寸均以标注为准, 图上自行量取无效。  
3、本图需加盖本设计院工程设计出图专用章及注册章方有效。  
4、本套图纸需经国家有关部门批准方可施工。

图例及主要设备表(一)

| 图 例 设 备 表 |    |                   |               |    |                                   |
|-----------|----|-------------------|---------------|----|-----------------------------------|
| 序号        | 图例 | 名称                | 型号规格          | 单位 | 备注                                |
| 1         |    | 单芯LED支架灯(应急)      | 1x18W(应急型)    | 套  | 内置蓄电池, 吸顶安装(风机房中距墙2.6m)壁挂         |
| 2         |    | 双芯LED支架灯(应急)      | 2x18W(应急型)    | 套  | 连续供电时间t>180min 吸顶安装(风机房中距墙2.6m)壁挂 |
| 3         |    | LED灯              | 1x12W         | 套  | 壁挂, 竖井门上距墙2.6m                    |
| 4         |    | LED节能灯            | 1x12W(带红外感应)  | 套  | 带红外感应控制开关 吸顶安装                    |
| 5         |    | LED节能灯            | 1x25W         | 个  | 吸顶安装                              |
| 6         |    | 防水防尘节能灯           | 1x25W         | 个  | 吸顶安装                              |
| 7         |    | 排气扇               | 86SH60/GB 双速型 | 套  | 吸顶安装                              |
| 8         |    | 洗衣机插座(3极带开关)      | 16A 250V      | 个  | 安全型 带防溅盒(满足[P54]) 底距地1.3m         |
| 9         |    | 厨房插座(2+3极带开关)     | 10A 250V      | 个  | 安全型 带防溅盒(满足[P54]) 底距地1.3m         |
| 10        |    | 排油烟机插座(3极)        | 16A 250V      | 个  | 安全型 带防溅盒(满足[P54]) 底距地2.1m         |
| 11        |    | 冰箱插座(2+3极,<2kW)   | 10A 250V      | 个  | 安全型 带防溅盒(满足[P54]) 底距地0.4m         |
| 12        |    | 燃气报警插座(2+3极)      | 10A 250V      | 个  | 安全型 带防溅盒(满足[P54]) 底距地1.8m         |
| 13        |    | 卫生间插座(2+3极)       | 10A 250V      | 个  | 安全型 带防溅盒(满足[P54]) 底距地1.3m         |
| 14        |    | 热水器插座(3极带开关,<2kW) | 16A 250V      | 个  | 安全型 带防溅盒(满足[P54]) 底距地2.3m         |
| 15        |    | 智能电表插座(2+3极)      | 10A 250V      | 个  | 安全型 带防溅盒(满足[P54]) 底距地0.4m         |
| 16        |    | 空调器插座(3极带开关,<2kW) | 10A 250V      | 个  | 安全型 底边距地2.1m                      |
| 17        |    | 空调器插座(3极带开关,<2kW) | 16A 250V      | 个  | 安全型 底边距地0.4m                      |
| 18        |    | 普通插座(2+3极)        | 10A 250V      | 个  | 安全型 底边距地0.4m                      |
| 19        |    | 家居配线箱接线盒          | 86SH60/GB     | 个  | 暗装, 底距地0.4m                       |
| 20        |    | 单联单控跷板开关          | 10A 250V      | 只  | 底距地1.3m                           |
| 21        |    | 双联单控跷板开关          | 10A 250V      | 只  | 底距地1.3m                           |
| 22        |    | 三联单控跷板开关          | 10A 250V      | 只  | 底距地1.3m                           |
| 23        |    | 全热交换新风机控制开关       | 10A 250V 设备自带 | 只  | 底距地1.3m                           |
| 24        |    | 残疾人控制开关           | 10A 250V      | 只  | 底距地1.0m                           |
| 25        |    | 电度表箱              | 详系统图          | 台  | 明装, 底距地1.4m                       |
| 26        |    | 照明配电箱             | 详系统图          | 台  | 暗装, 公区底距地1.5m, 户内1.6m             |
| 27        |    | 风电源动力配电箱          | 详系统图          | 台  | 明装, 底距地1.5m                       |
| 28        |    | 消防电源箱             | 详系统图          | 台  | 明装, 底距地1.5m                       |
| 29        |    | 动力配电箱             | 详系统图          | 台  | 明装, 底距地1.5m                       |
| 30        |    | 低压柜               | GGD           | 台  | 配电室安装, 底边距地2m                     |
| 31        |    | 总等电位端子箱           |               | 个  | 暗装, 底距地0.5m                       |
| 32        |    | 局部等电位端子箱          |               | 个  | 暗装, 底距地0.5m                       |
| 33        |    | 86接线盒             | 86SH60/GB     | 个  | 暗装                                |
| 34        |    |                   |               |    |                                   |
| 35        |    |                   |               |    |                                   |
| 36        |    |                   |               |    |                                   |

注: 住户内起居室、通道和卫生间的照明开关, 选用夜间有灯显示的面板。

图例及主要设备表(二)

| 图 例 设 备 表 |    |                 |                    |    |                           |
|-----------|----|-----------------|--------------------|----|---------------------------|
| 序号        | 图例 | 名称              | 型号规格               | 单位 | 备注                        |
| 1         |    | 门禁可视对讲机户外机      | 详系统图               | 个  | 接线盒下沿距地1.3m               |
| 2         |    | 电磁锁             | 详系统图               | 个  | 门上安装                      |
| 3         |    | 电锁开门按钮          | 详系统图               | 个  | 暗装, 下沿距地1.3m              |
| 4         |    | 门禁可视对讲系统主机      |                    | 个  | 明装, 下沿距地2.2m              |
| 5         |    | 可视对讲室内分机        | 带紧急按钮及报警功能         | 个  | 明装, 下沿距地1.3m              |
| 6         |    | 家居配线箱           | 86SH60/GB          | 个  | 暗装, 下沿距地0.5m              |
| 7         |    | 电话插座            | 型号甲方自定             | 个  | 暗装, 下沿距地0.4m              |
| 8         |    | 网络插座            | 型号甲方自定             | 个  | 暗装, 下沿距地0.4m              |
| 9         |    | 电视插座            | 型号甲方自定             | 个  | 暗装, 下沿距地0.4m              |
| 10        |    | 燃气报警器           | 燃气报警网带声光报警功能       | 个  | 吸顶安装                      |
| 11        |    | 家居紧急呼叫按钮        |                    | 个  | 暗装, 下沿距地0.75m             |
| 12        |    | 有线电视分支分配器箱      | 40x40x100mm        | 个  | 电气竖井内明装, 底距地0.5m          |
| 13        |    | 层对讲模块解码分配器箱     | 40x40x100mm        | 个  | 电气竖井内明装, 底距地0.8m          |
| 14        |    | 光纤分路接线箱         | 40x40x100mm        | 个  | 电气竖井内明装, 底距地1.5m          |
| 15        |    | 总光纤分路配线箱        | 40x40x100mm        | 个  | 位于地下一层 弱电间明装, 底距地1.2m     |
| 16        |    | 有线电视前端箱         | 40x40x100mm        | 个  | 位于地下一层 弱电间明装, 底距地1.2m     |
| 17        |    | 监控分机箱           | 40x40x100mm        | 个  | 位于地下一层电井 电气竖井内明装, 底距地1.2m |
| 18        |    | 半球型彩色摄像机400万像素  | PDE 供电型            | 个  | 吸顶/吊顶安装                   |
| 19        |    | 五方对讲电话/专用消防对讲电话 | 型号甲方自定             | 个  | 电梯轿厢安装、电梯机房安装             |
| 20        |    | 无线网络1对1一对使用     | PDE 供电, 10/100M自适应 | 个  | 电梯轿厢吸顶、电梯机房距地2.4m         |
| 21        |    |                 |                    |    |                           |
| 22        |    |                 |                    |    |                           |
| 23        |    |                 |                    |    |                           |

附表 导线穿管表

| 电线线芯截面<br>S(mm) <sup>2</sup> | 热镀锌焊接钢管(SC)<br>(管内导线根数) |    |    |    |    |    | 电线管(JDG)(PVC)<br>(管内导线根数) |    |    |    |    |    |    |    |
|------------------------------|-------------------------|----|----|----|----|----|---------------------------|----|----|----|----|----|----|----|
|                              | 2                       | 3  | 4  | 5  | 6  | 7  | 8                         | 2  | 3  | 4  | 5  | 6  | 7  | 8  |
| 1.0                          | 20                      | 20 | 20 | 20 | 20 | 20 | 20                        | 20 | 20 | 20 | 25 | 25 | 25 | 25 |
| 1.5                          | 20                      | 20 | 20 | 20 | 20 | 25 | 25                        | 20 | 20 | 20 | 25 | 25 | 32 | 32 |
| 2.5                          | 20                      | 20 | 20 | 20 | 20 | 25 | 25                        | 20 | 20 | 25 | 25 | 25 | 32 | 32 |
| 4.0                          | 20                      | 20 | 20 | 25 | 25 | 25 | 25                        | 20 | 25 | 25 | 25 | 32 | 32 | 32 |
| 6.0                          | 20                      | 20 | 20 | 25 | 25 | 25 | 32                        | 20 | 25 | 25 | 32 | 32 | 32 | 40 |
| 10.0                         | 20                      | 25 | 25 | 32 | 32 | 40 | 40                        | 25 | 32 | 32 | 32 | 40 | 40 |    |
| 16.0                         | 25                      | 25 | 32 | 40 |    |    |                           | 25 | 32 | 40 | 40 |    |    |    |
| 25.0                         | 25                      | 32 | 40 | 40 |    |    |                           | 32 | 40 | 50 | 50 |    |    |    |
| 35.0                         | 32                      | 40 | 50 | 50 |    |    |                           | 40 | 50 | 50 | 70 |    |    |    |
| 50.0                         | 32                      | 50 | 50 | 70 |    |    |                           | 50 | 50 | 70 | 80 |    |    |    |

导线穿阻燃型硬质塑料管(PC)


| 导线截面               | 导 线 根 数 |   |      |      |   |      |   |
|--------------------|---------|---|------|------|---|------|---|
| (mm <sup>2</sup> ) | 2       | 3 | 4    | 5    | 6 | 7    | 8 |
| 2.5                | PC16    |   |      |      |   |      |   |
| 4                  | PC20    |   | PC25 |      |   | PC32 |   |
| 6                  |         |   |      | PC40 |   |      |   |

导线穿镀锌钢管JDG管或采用热镀锌焊接钢管SC

| 导线截面               | 导 线 根 数           |   |   |   |   |   |   |
|--------------------|-------------------|---|---|---|---|---|---|
| (mm <sup>2</sup> ) | 2                 | 3 | 4 | 5 | 6 | 7 | 8 |
| 2.5                | JDG20 JDG25 JDG32 |   |   |   |   |   |   |
| 4                  |                   |   |   |   |   |   |   |
| 6                  |                   |   |   |   |   |   |   |


导线敷设方式简写表

| 代号 | 敷设方式       | 代号  | 敷设方式      |
|----|------------|-----|-----------|
| CT | 电缆桥架敷设     | WC  | 暗敷设在墙内    |
| MR | 金属线槽敷设     | WS  | 沿墙面敷设     |
| CC | 暗敷设在屋面或顶板内 | CE  | 沿天棚或顶板面敷设 |
| FC | 地板或地下敷设    | SCE | 吊顶内敷设     |
| F  | 地板及地坪下     | CLC | 暗敷设在柱内    |

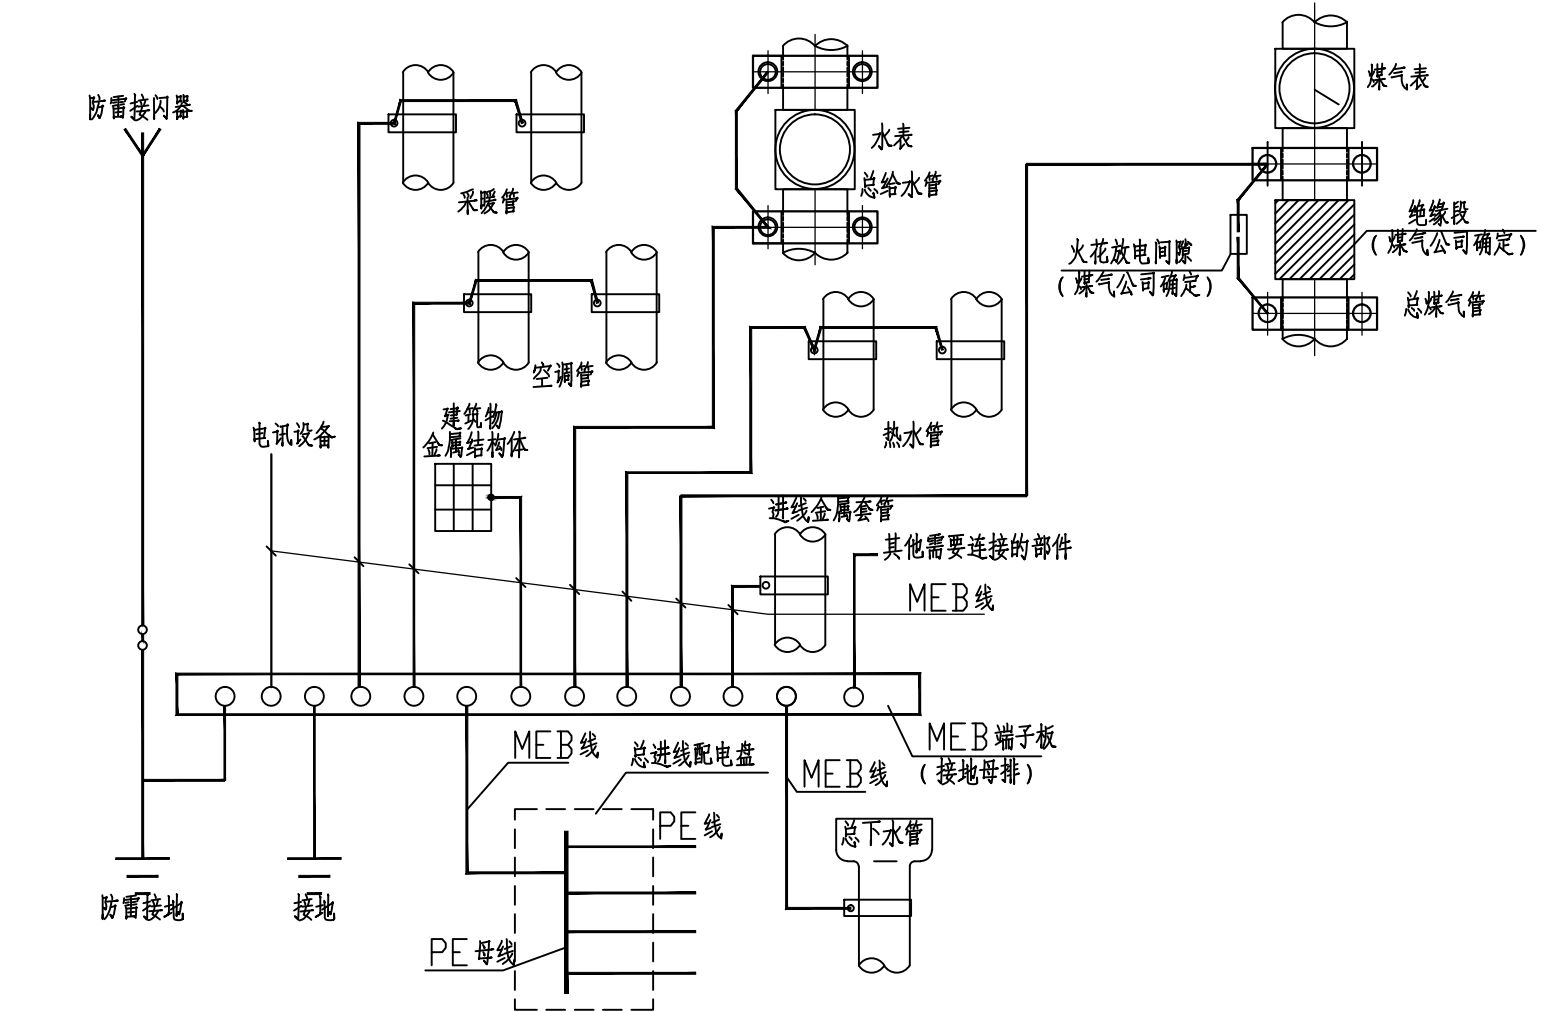


总等电位联结示意图

说明:  
1.MEB端子板宜设置在电源进线或进线配电箱处, 并加罩, 防止无关人员触动。  
2.相邻近管道及金属结构允许用一根MEB线连接。  
3.当防雷设施利用建筑物金属体和基础钢筋作引下线 and 接地极时, 引下线应与等电位联结系统连通以实现等电位。

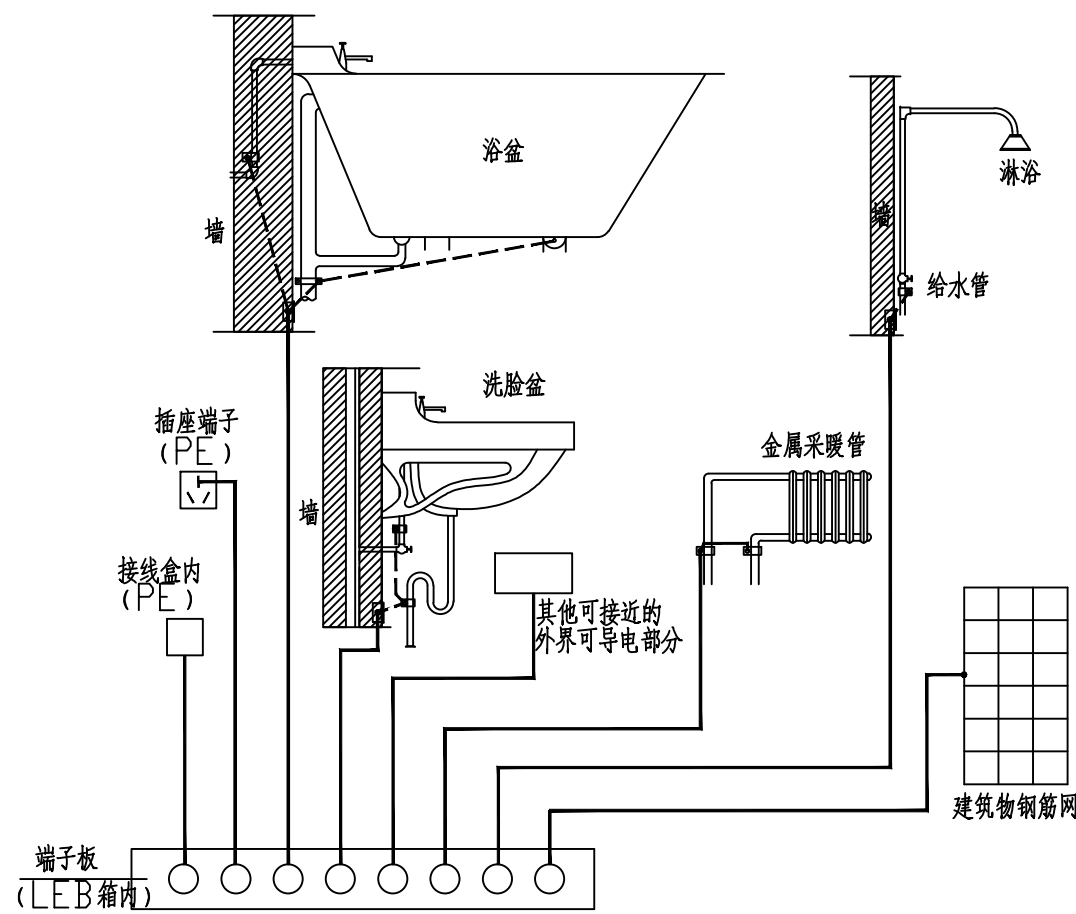

卫生间局部等电位连接做法

说明:  
1.地面内钢筋网应做等电位联结, 墙内若有钢筋网与等电位联结线连通。  
2.图中LEB线均采用BV-1x2.5mm导线穿PC20管暗敷。  
3.卫生间辅助等电位端子板的设置位置应方便检测, 具体做法见大样图。  
4.卫生间辅助等电位联结具体做法详见图集《新22D6》P75、76。

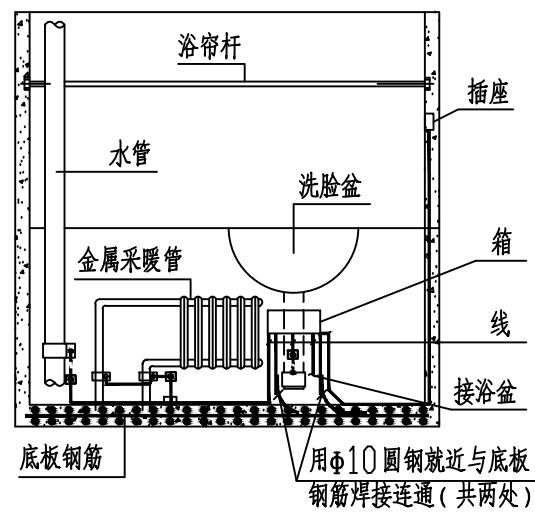

卫生间局部等电位剖面

平面示意: KEY PLAN

| 注册执业章                      |                              |
|----------------------------|------------------------------|
| REGISTERED PRACTICE SIGNET |                              |
| 姓名: 张 丽 丽                  | NAME                         |
| 注册证书号码: DG125300097        | REGISTRATION CERTIFICATE NO. |
| 注册印章号码: 5102758-DG004      | REGISTERED SIGNET NO.        |
| 建设单位: 新疆如茂房地产开发有限公司        | CLIENT                       |
| 工程名称: 阿勒泰市御景园商住一期建设项目      | PROJECT                      |
| 子项名称: 10#住宅楼               | SUB ITEM                     |
| 设计号: YZXJ-2023-07-10       | PROJECT NO.                  |
| 图 名:                       | FIG. TITLE                   |
| 电气材料表                      |                              |
| 项目负责人<br>PROJECT LEADER    | 李 亮                          |
| 审 定<br>APPROVED BY         | 黎 晨                          |
| 审 核<br>AUDIT               | 黎 晨                          |
| 专业负责人<br>SPECIAL ENGINEER  | 张 丽 丽                        |
| 校 对<br>CHECKED BY          | 张 丽 丽                        |
| 设 计<br>DESIGNED BY         | 张 杰                          |

中华人民共和国注册电气工程师(供配电)  
姓 名: 张 丽 丽  
注册号: 5102758-DG004  
有效期至: 至2027年12月

四川省建设工程设计出图专用章  
永忠工程管理(集团)有限公司  
资质等级: 水利行业(河道整治、引调水、城市防洪、灌溉排涝)专业乙级;  
建筑行业(建筑工程)甲级  
注册证号: A151A02463 有效期至: 2031年02月11日

比例: 1:100 SCALE 图号: 电施-03 FIG. NO.

版本号: 第一版 VERSION