

永忠工程管理（集团）有限公司
Yong Zhong Engineering Management (Group) Co., Ltd.
甲级工程设计证书编号:A151027583

合作设计-顾问单位 CONSULTING ARCHITECT
设计部门 新疆分公司

电 话 18999878562

说明:
1、本图版权为本设计院拥有, 任何人士如未获允许不得翻印任何部分。
2、所有尺寸均以标注为准, 图上自行量取无效。
3、本图需加盖本设计院工程设计出图专用章及注册章方有效。
4、本套图纸需经国家有关部门批准方可施工。

平面示意: 001 PLAN

注册执业章
REGISTERED PRACTICE SIGNET
姓名: 张 丽 丽
注册证书号码: DG125300097
注册印章号码: 5102758-DG004
建设单位: 新疆如茂房地产开发有限公司
工程名称: 阿勒泰市御景园商住一期建设项目
子项名称: 10#住宅楼
设计号: YZXJ-2023-07-10
图 名: 配电箱系统图




项目负责人 PROJECT LEADER 李 亮
审 定 黎 晨
审 核 黎 晨
专业负责人 SENI ENGINEER 张 丽 丽
校 对 张 丽 丽
设 计 张 杰

中华人民共和国注册电气工程师(供配电)
姓名: 张 丽 丽
注册号: 5102758-DG004
有效期: 至2027年12月

四川省建设工程设计出图专用章
永忠工程管理（集团）有限公司
资质等级: 水利行业（河道整治、引调水、城市防洪、灌溉排涝）专业乙级；
建筑行业（建筑工程）甲级
章编号: A151A02463 有效期至: 2031年02月11日

比例: 1:100 SCALE 图号: 电施-07 DWG NO.

版本号: 第一版 VERSION

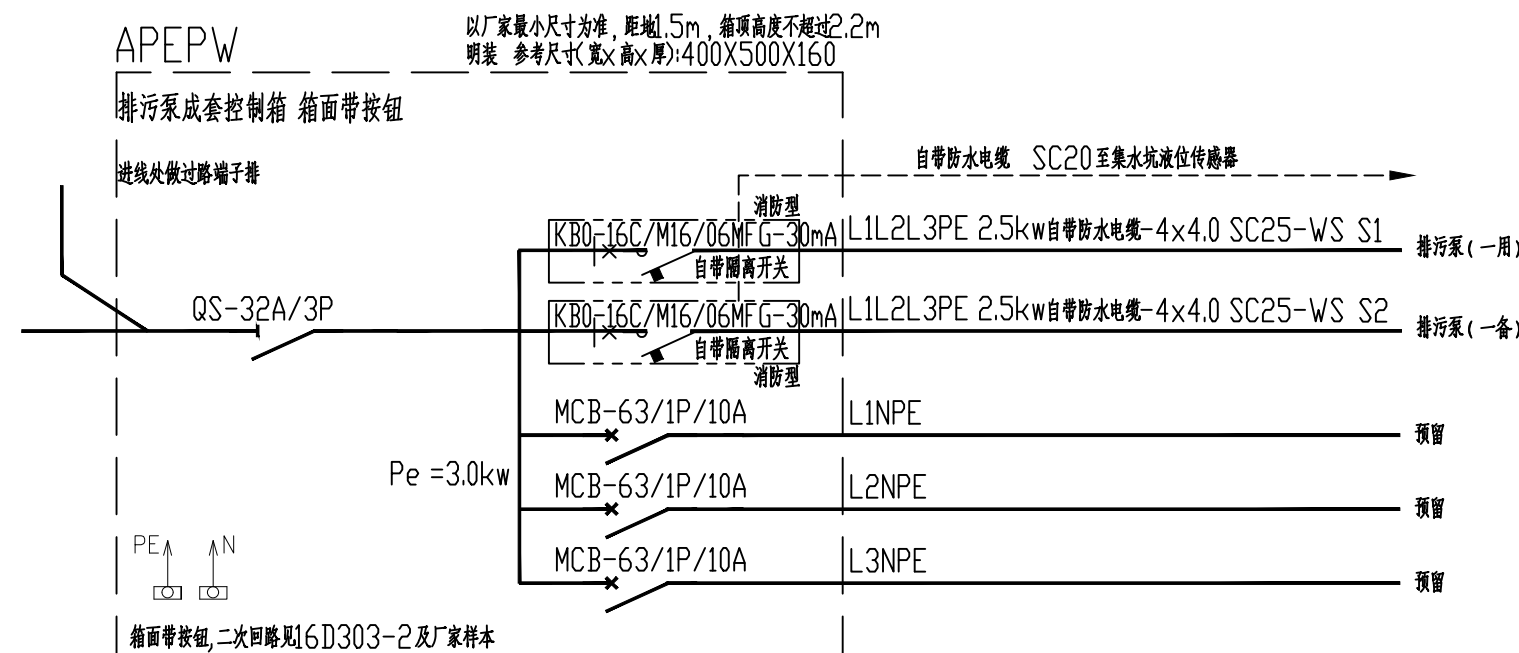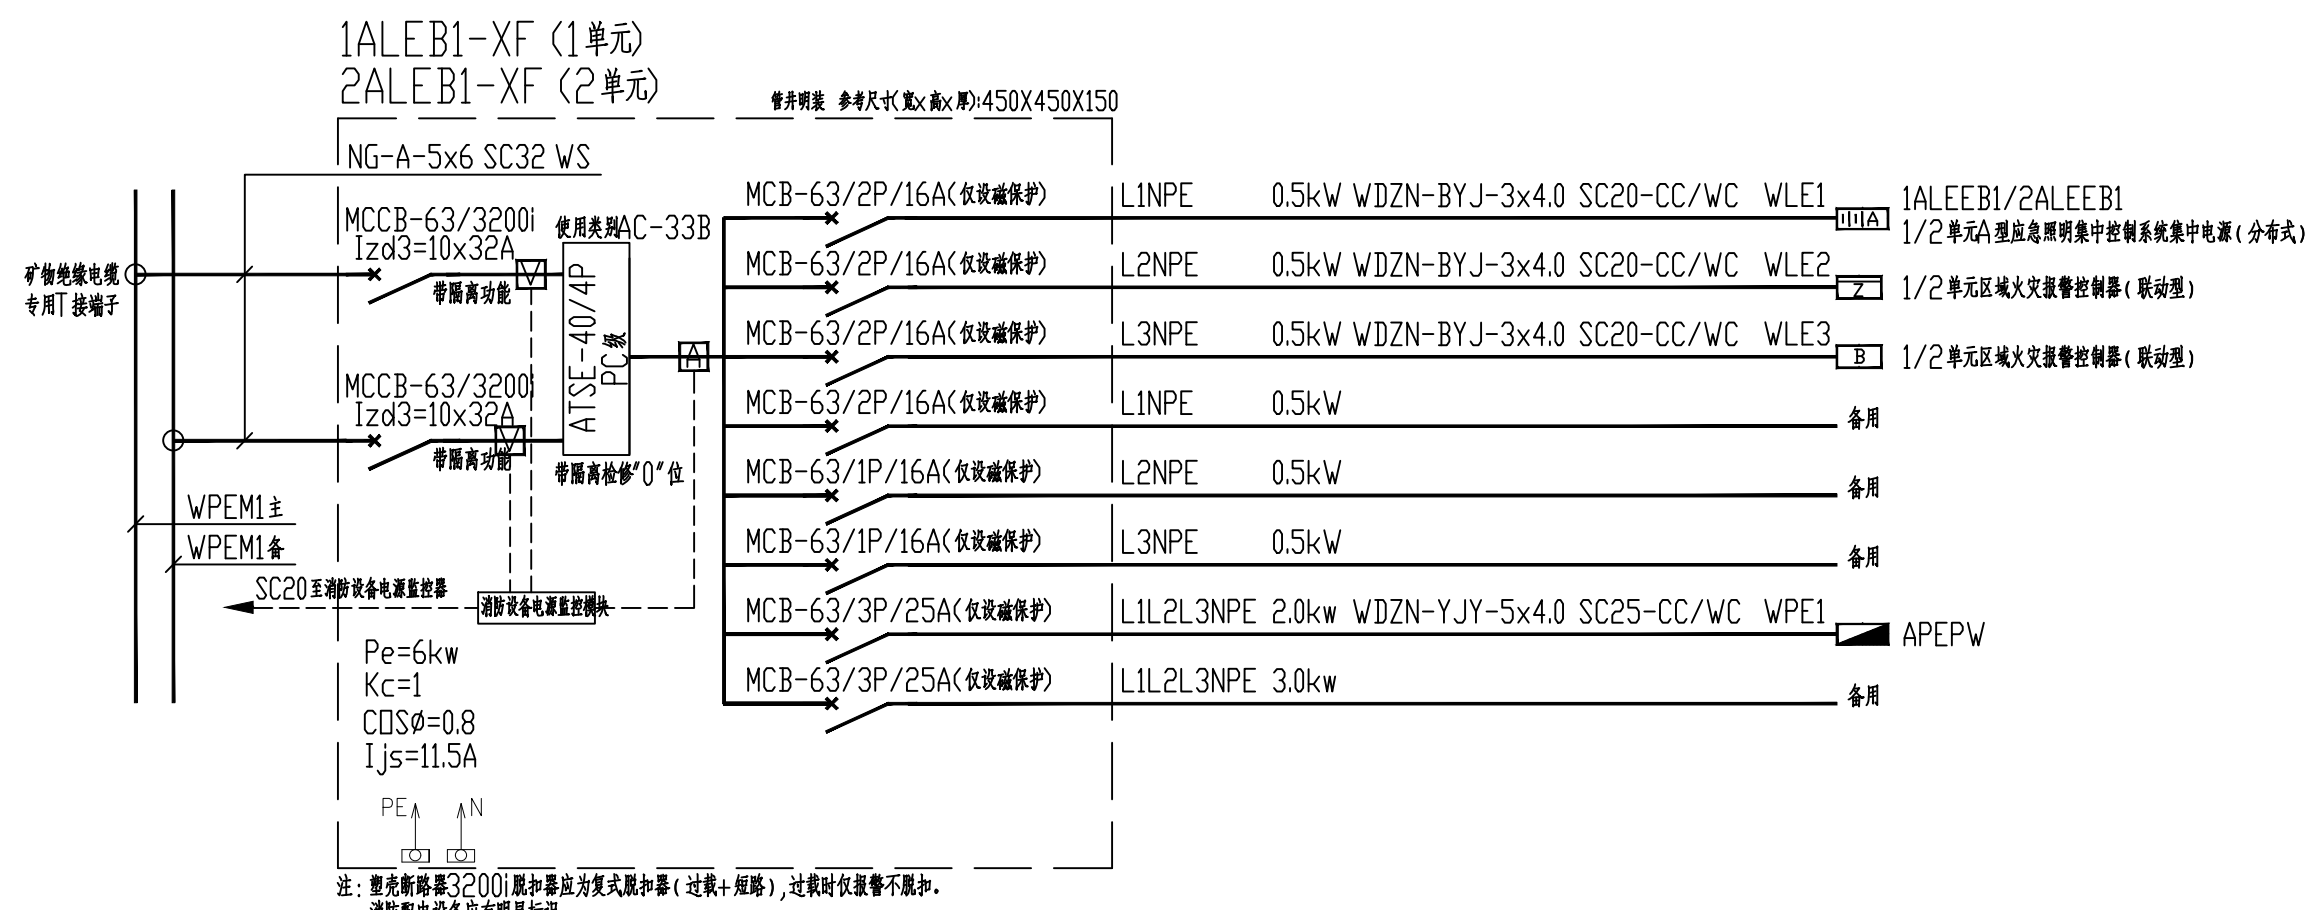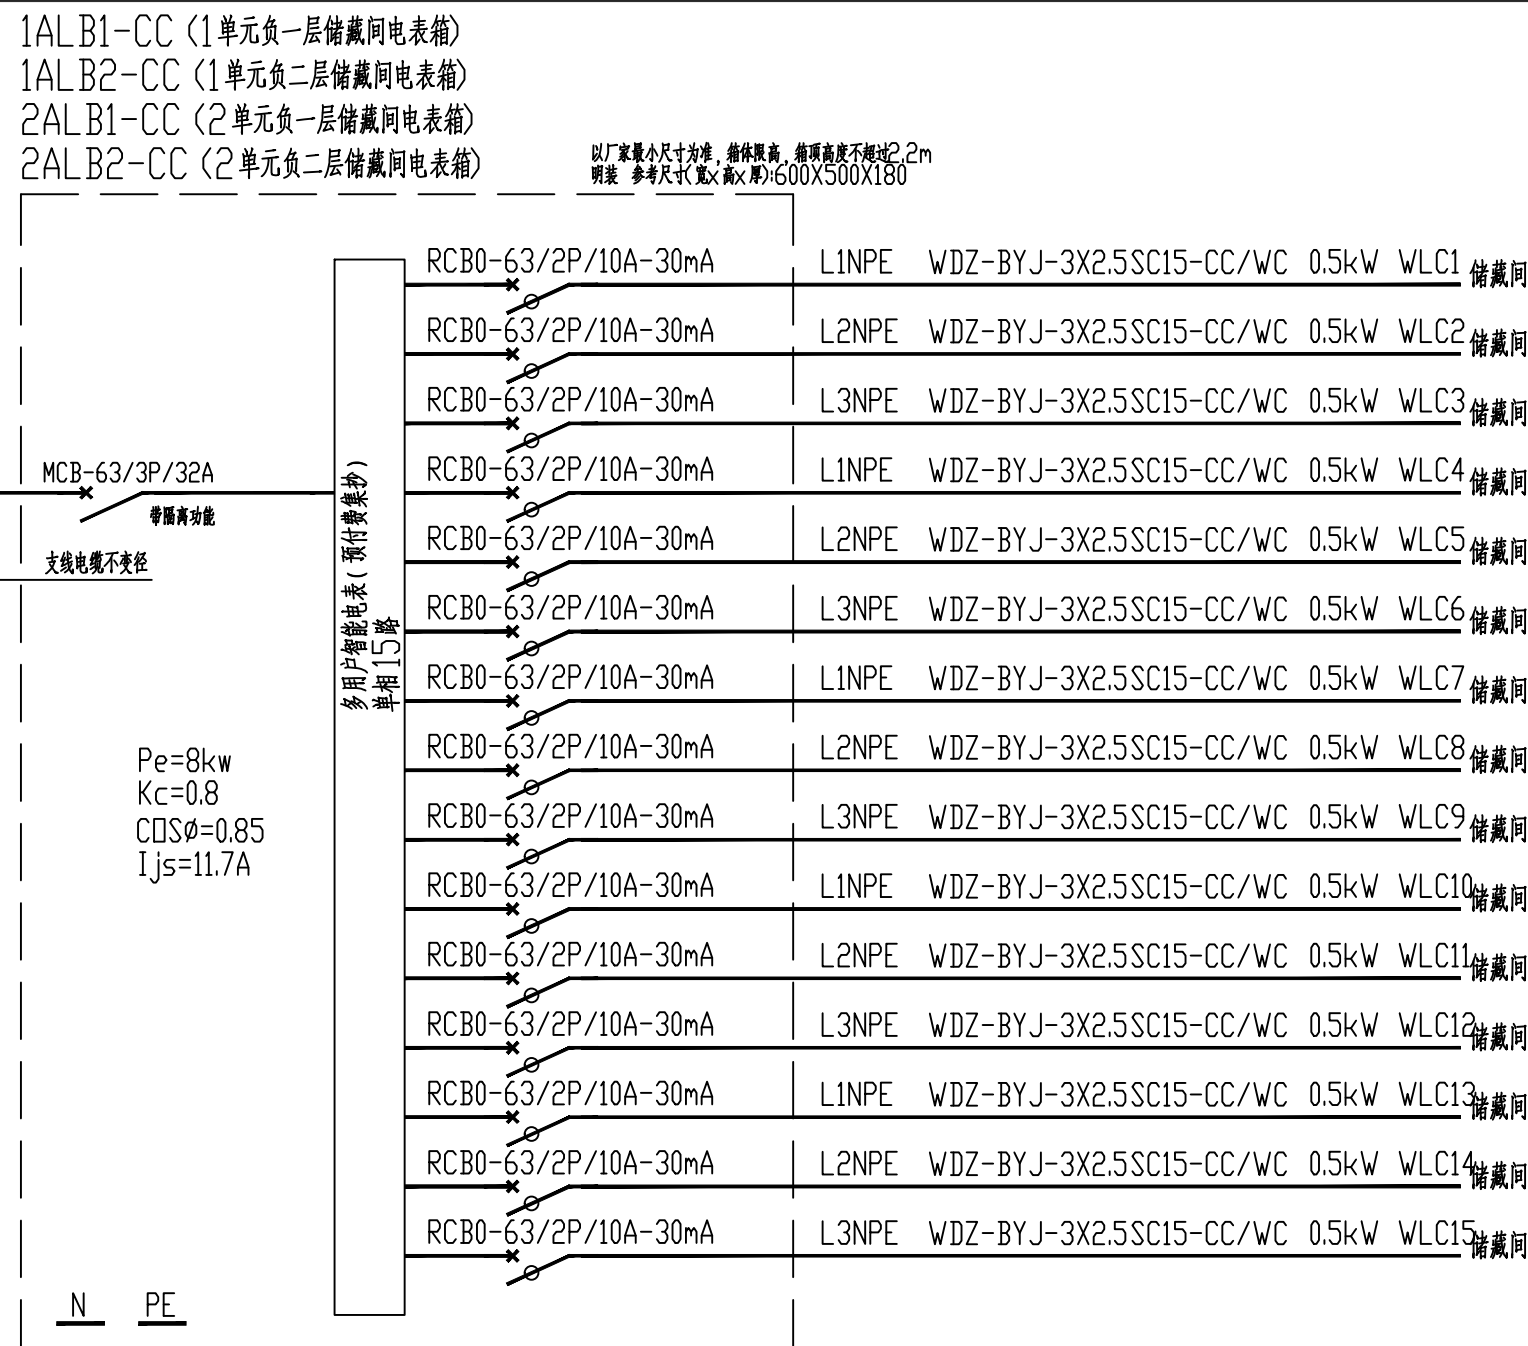

1.CPS电机保护器采用带漏电保护型, 内带隔离开关, 剩余电流值为30mA, 仅报警不断电。
2. 瞬动过电流脱扣器或过电流继电器瞬时动作的额定电流, 取电动机启动电流的2~2.5倍。
3. 水泵控制二次原理图附16DJ303-3图及厂家手册, 箱面带按钮。
4. 液位测量与控制附1703-1~2(2011版)图及厂家手册, 箱面带液位高度显示。
5. 双台水泵高水位报警, 低水位报警, 溢流水位及泵故障报警, 手动自动开关, 备用泵自动投入。

