


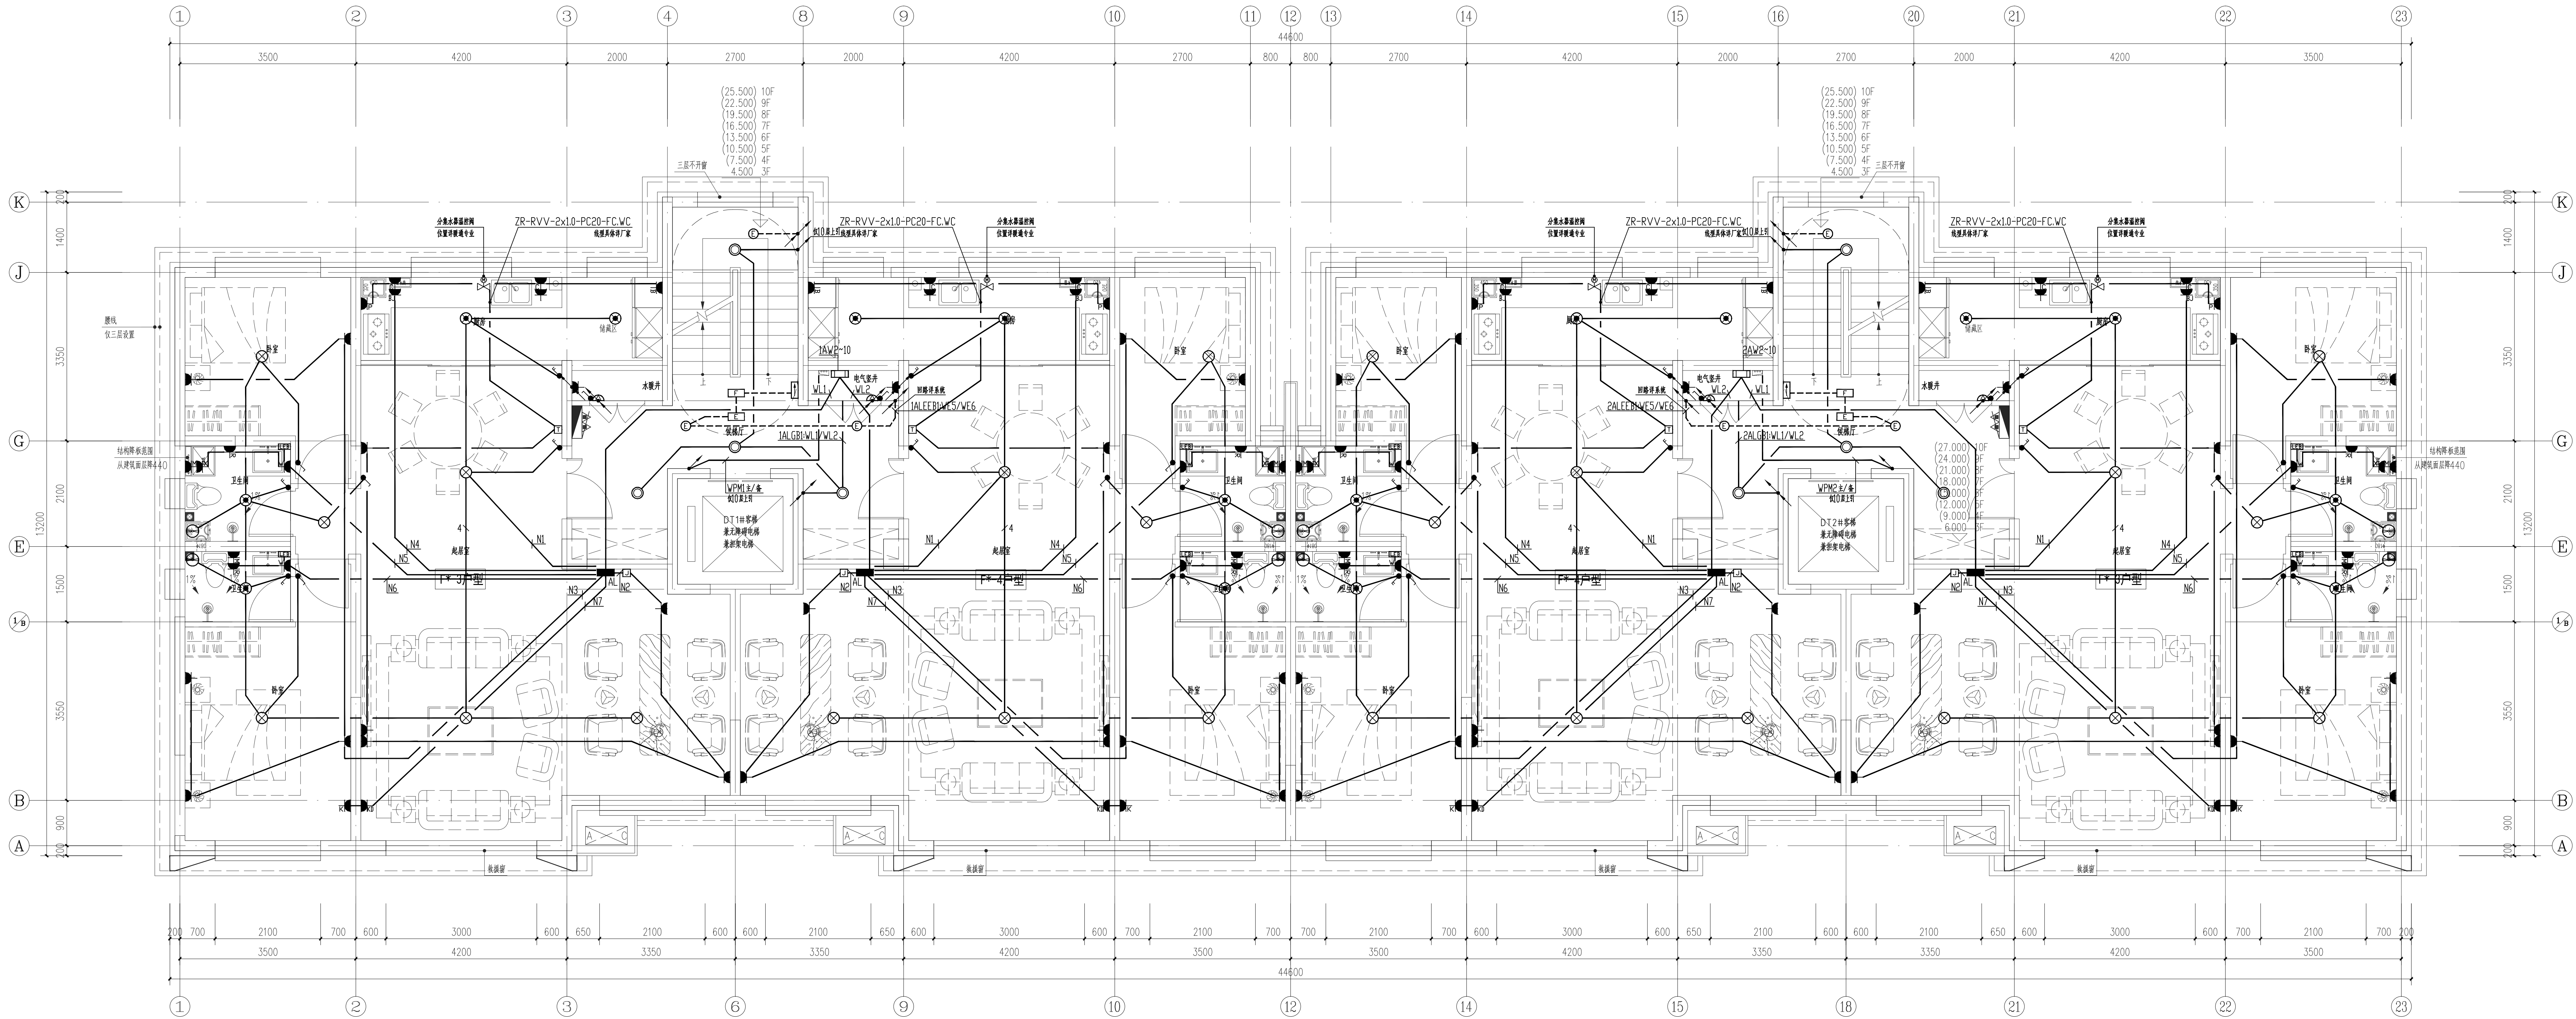

标准层照明及应急照明平面图 1:50

- 图例:
1. 照明开关及其控制线
2. 灯具及其安装位置
3. 应急照明及其控制线
4. 插座及其安装位置

注册执业章	
姓名	张丽丽
注册证书号码	DC125300097
注册印章号码	5102758-DG004
建设单位	新疆知房房地产开发有限公司
工程名称	阿勒泰市御景园商住一期建设项目
子项名称	10#住宅楼
设计号	YXJ-2023-07-10
图名	标准层照明及应急照明平面图
项目负责人	李亮
审定	黎晨
审核	黎晨
专业负责人	张丽丽
校对	张丽丽
设计	张杰

中华人民共和国注册电气工程师(供配电)
姓名: 张丽丽
注册号: 6102758-DG004
有效期至: 2027年12月

四川省建设工程设计出图专用章
永忠工程管理（集团）有限公司
资质等级: 水利行业（河道整治、引调水、城市防洪、灌溉排涝）专业乙级、建筑行业（建筑工程）甲级
资质证书编号: A151A02463 有效期至: 2031年02月11日