


永忠工程管理（集团）有限公司  
Tong Zhong Engineering Management (Group) Co., Ltd.  
甲级工程设计证书编号: A151027583

合作设计-顾问单位 CONSULTING ARCHITECT  
设计部门 新疆分公司  
电话 18999878562

说明:  
1、本图版权为本设计院所有, 任何人士如未获允许, 不得翻印任何部分。  
2、所有尺寸均以标注为准, 图上自行标注无效。  
3、本图需加基本设计院工程设计出图专用章及注册章方有效。  
4、本套图纸需经国家有关部门批准方可施工。

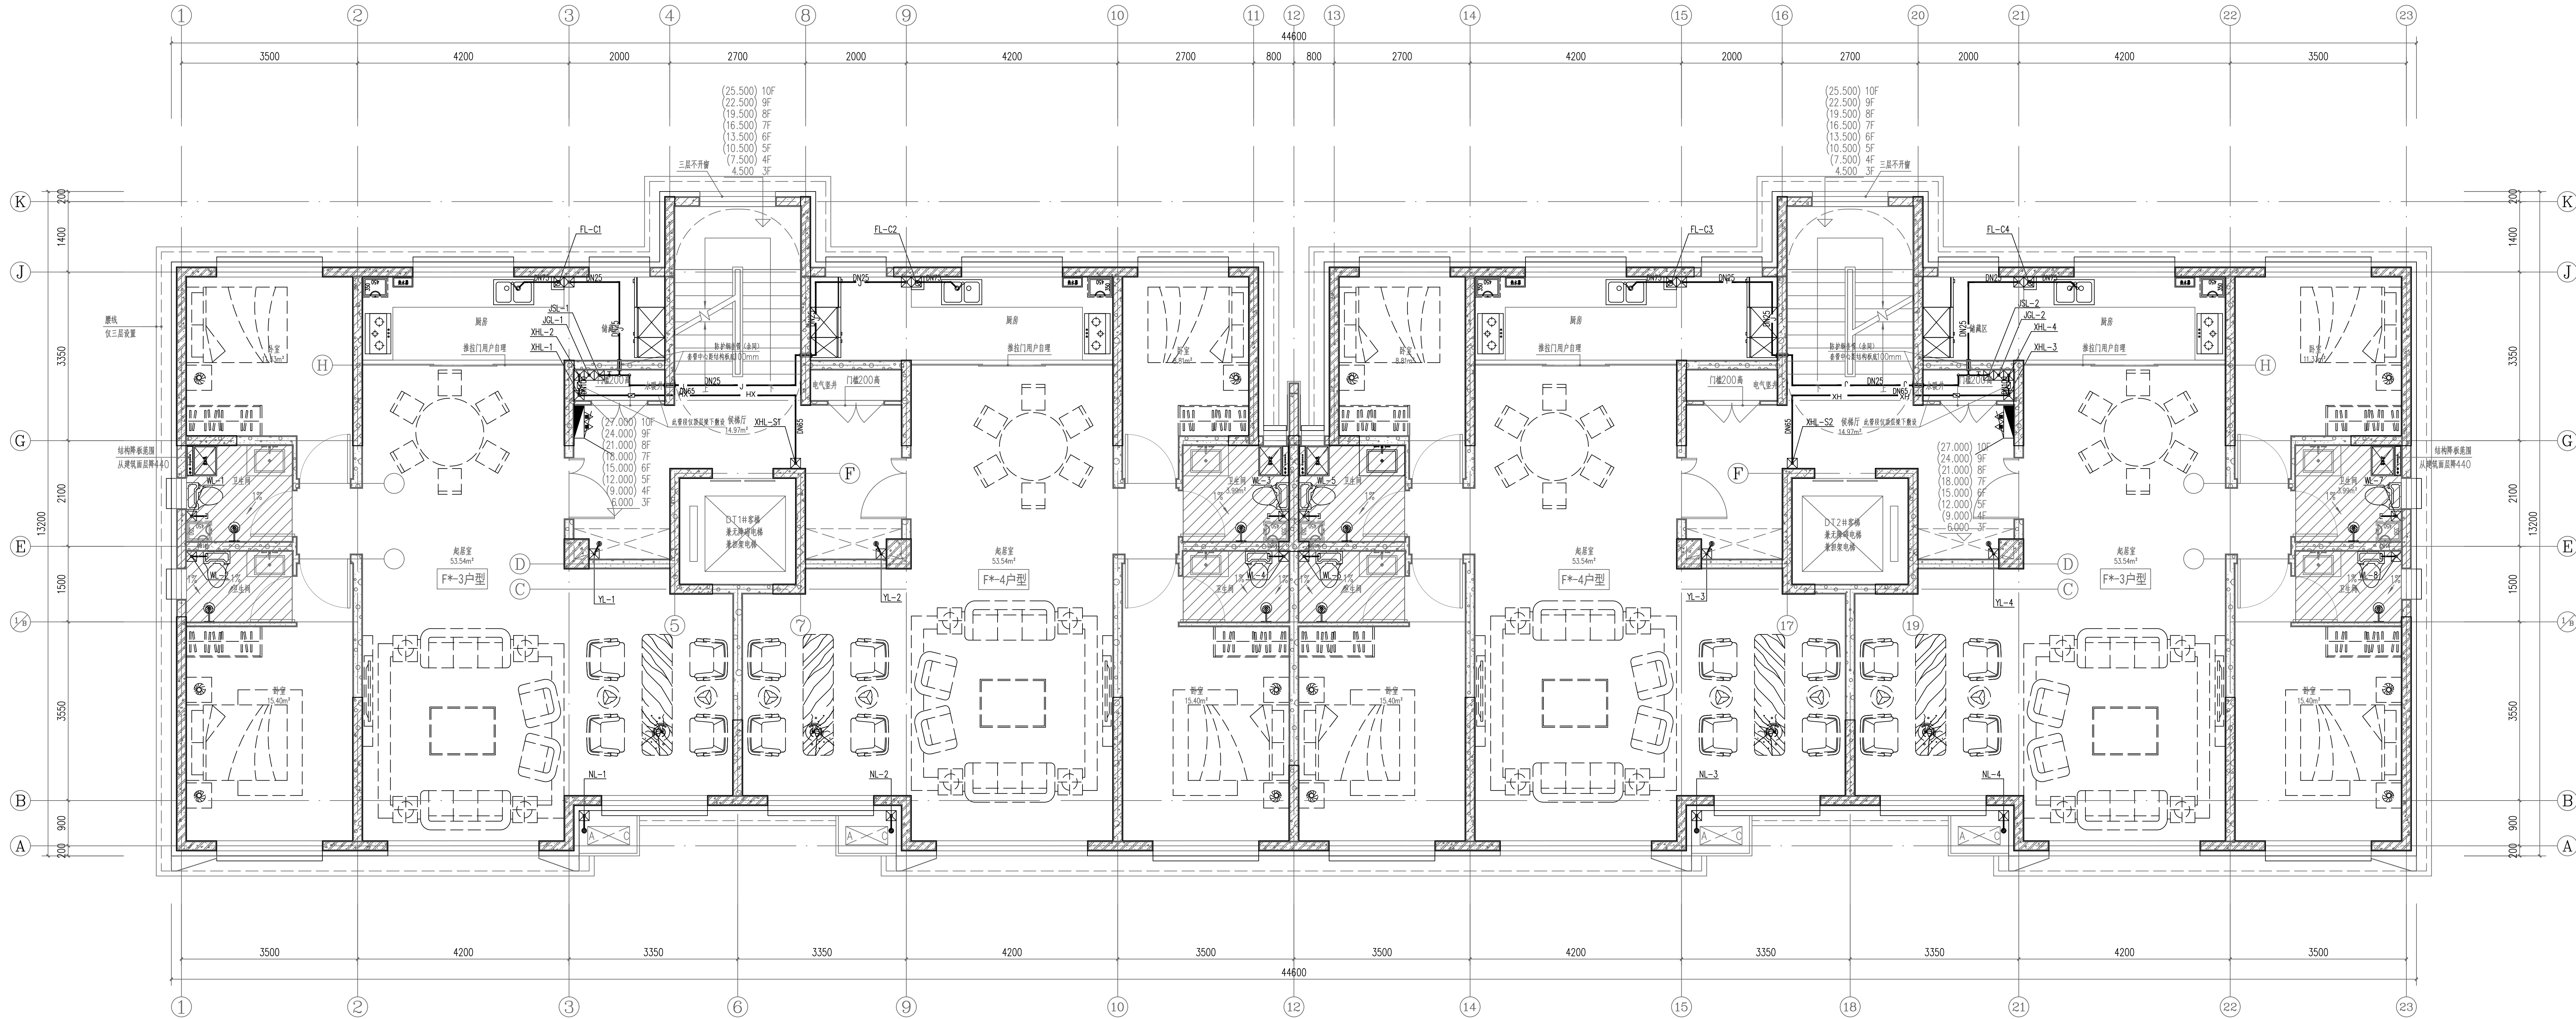

三层至十层给排水平面图 1:50  
本层建筑面积: 519.60m<sup>2</sup>

平面示意图: 注册执业章  
姓名: 杨辉  
注册证书号码: CS14320072  
注册印章号码: 5102758-CS004  
建设单位: 新疆如茂房地产开发有限公司  
工程名称: 阿勒泰市御景园商住一期建设项目  
子项名称: 10#住宅楼  
设计号: YZJ-2023-07-10  
图名: 三层至十层给排水平面图

|       |     |
|-------|-----|
| 项目负责人 | 李亮  |
| 审核    | 刘海龙 |
| 审核    | 肖伟  |
| 专业负责人 | 杨辉  |
| 校对    | 蒙琳琳 |
| 设计    | 何薇  |

注册专用章  
中华人民共和国注册公用设备工程师(给水排水)  
姓名: 杨辉  
注册号: 5102758-CS004  
有效期: 至2026年12月

四川省建设工程设计施工图审查  
大忠工程管理（集团）有限公司  
甲级资质: 水利行业（河道整治、引调水、城市防洪、灌溉排涝）专业已获  
建筑行业（建筑工程）甲级  
注册编号: A161A02463 有效期至: 2026年02月11日